

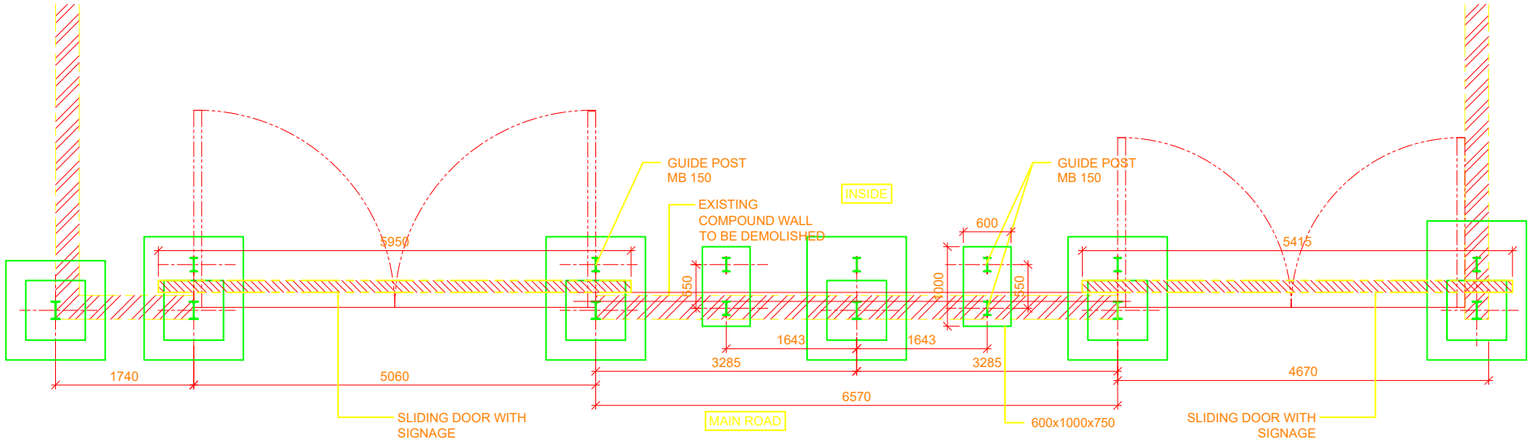


PLAN SHOWING COLUMN LOCATIONS

SCALE 1:50

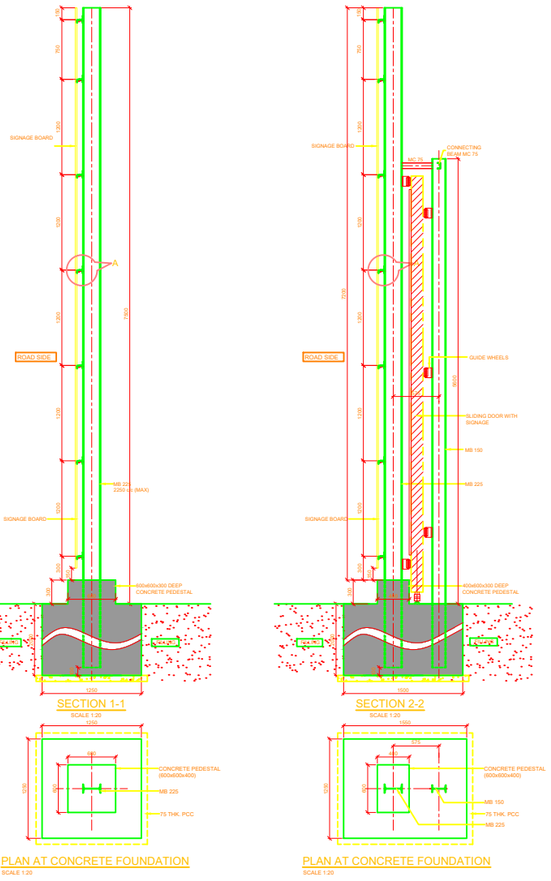


STRUCTURAL STEEL DETAIL FOR TEMPORARY BARRICADING

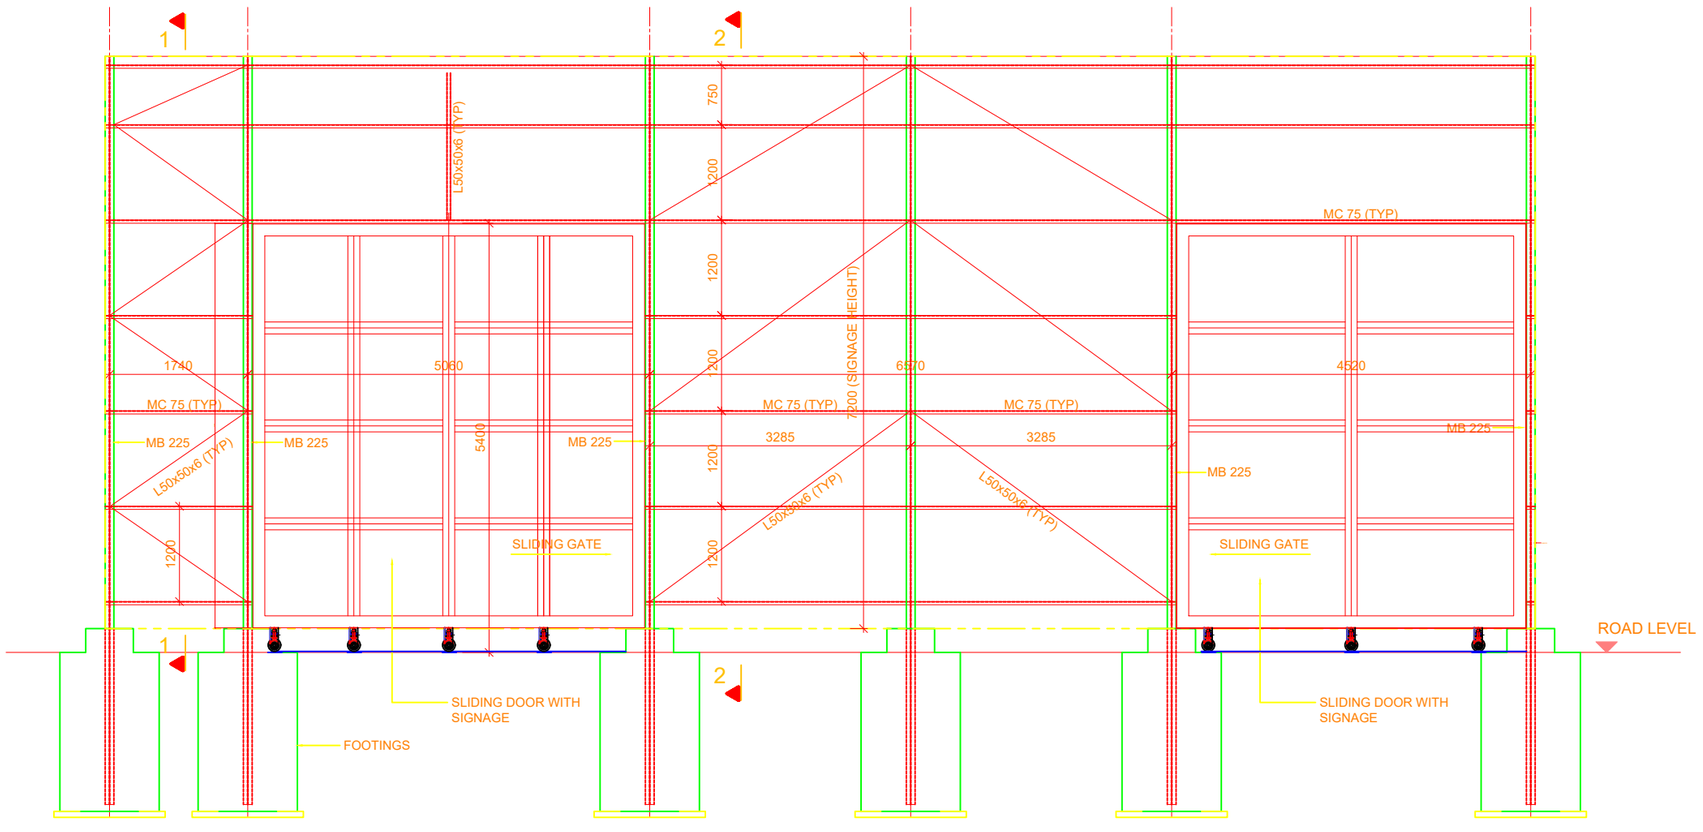


ELEVATION OF SIGNAGE


SCALE 1:50

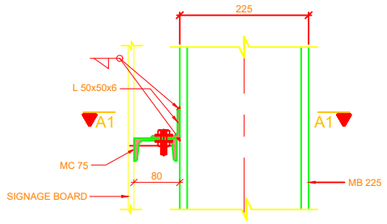


DETAIL 'A'
SCALE 1:5

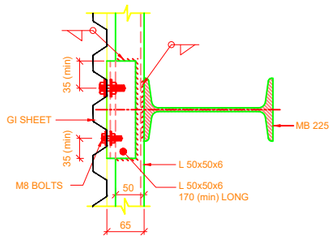


SECTION A1-A1
SCALE 1:5

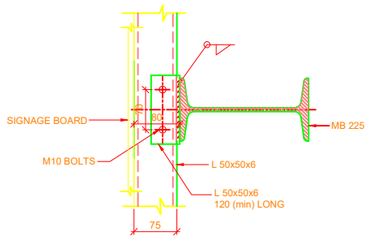


SECTION A1-A1
SCALE 1:5

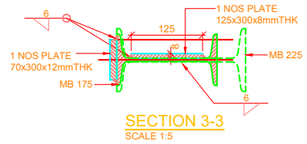


SECTION 3-3
SCALE 1:5

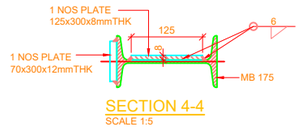


SECTION 4-4
SCALE 1:5

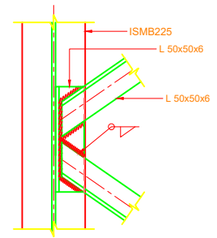


SECTION A1-A1
SCALE 1:5

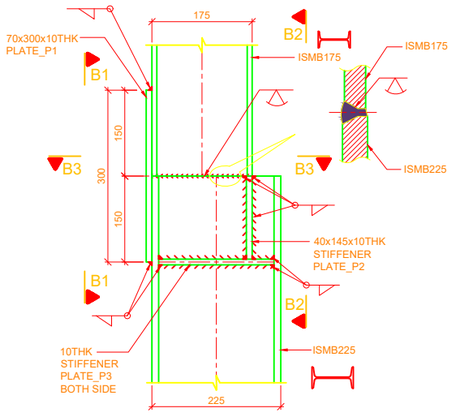


DETAIL 'B'
SCALE 1:5

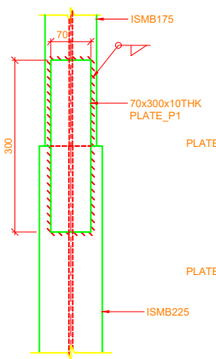

SECTION B1-B1
SCALE 1:5

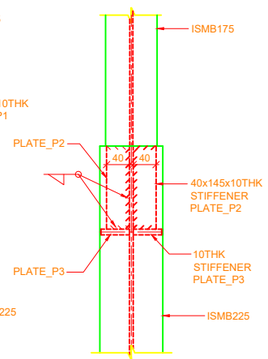

SECTION B2-B2
SCALE 1:5

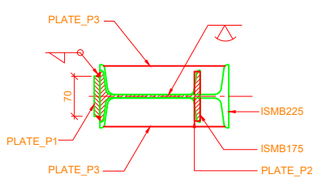

SECTION B3-B3
SCALE 1:5