

DRAWING

CLOSE VIEW

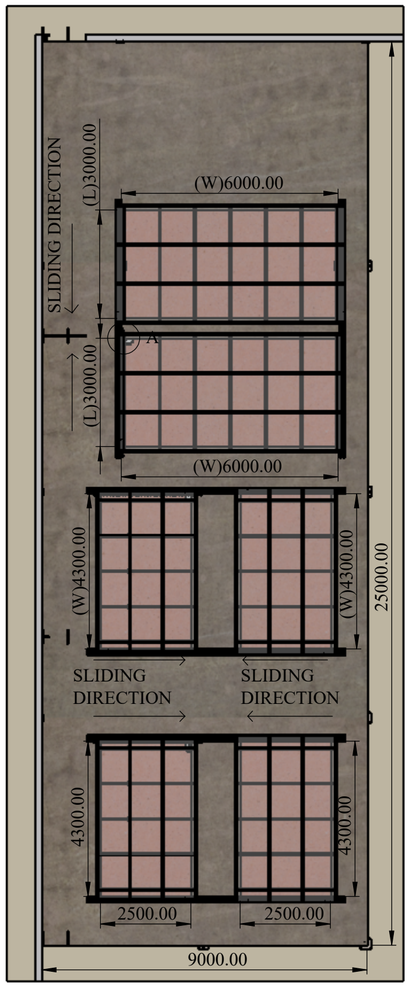


T.V.

OPEN VIEW

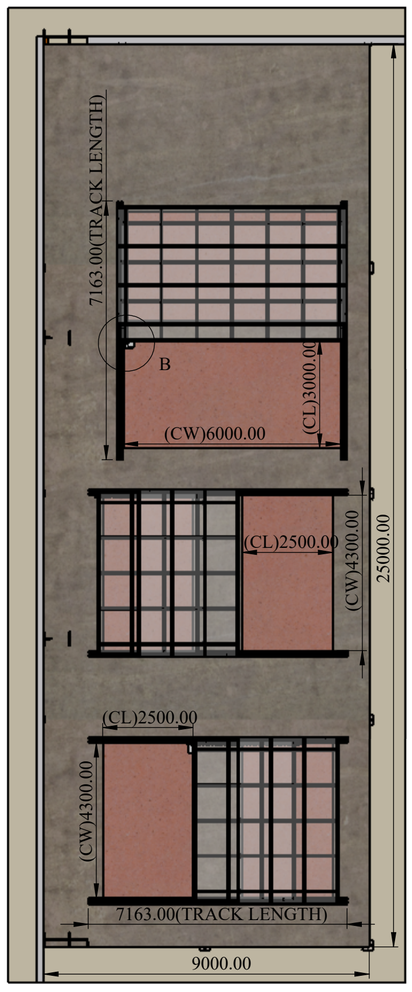


T.V.

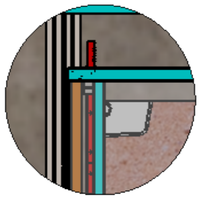


DETAIL A
SCALE 1 : 20

MOTOR
ARRAGEMENT

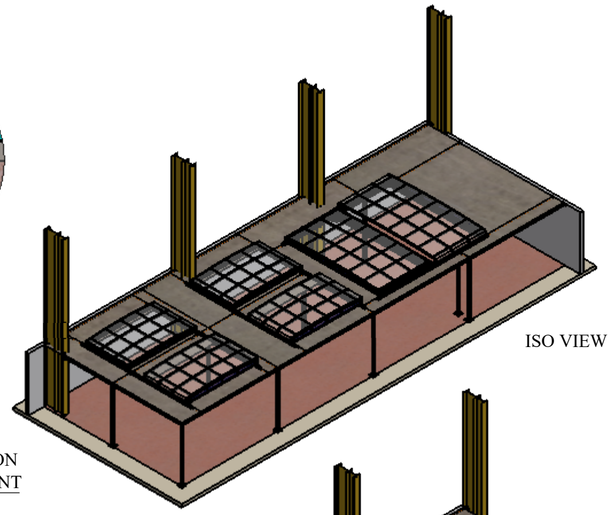


ISO VIEW

RACK+PINION
ARRAGEMENT

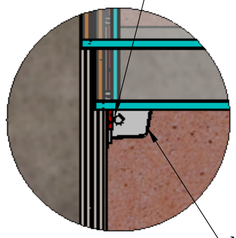


DETAIL B
SCALE 1 : 30

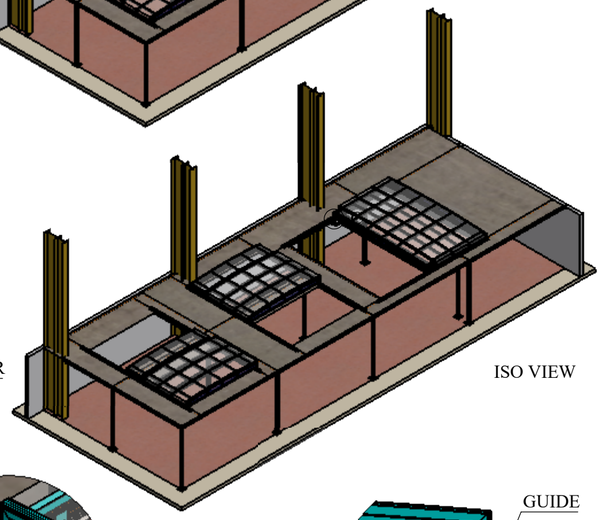


ISO VIEW

RACK+PINION
ARRAGEMENT

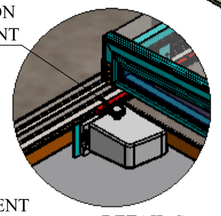


MOTOR
ARRAGEMENT

DETAIL C
SCALE 1 : 20

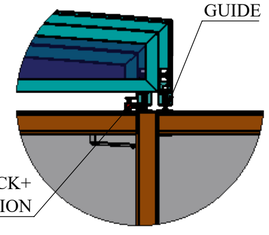


MOTOR
ARRAGEMENT

DETAIL D
SCALE 1 : 20

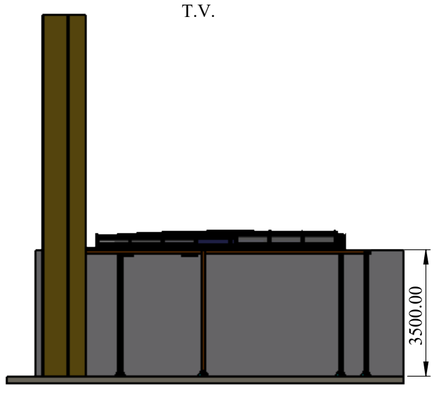

F.V.

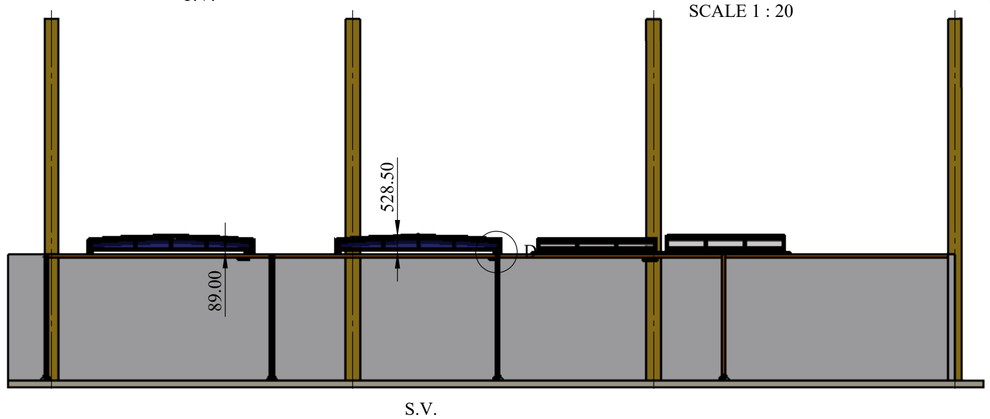

S.V.

REV DESCRIPTION	DATE	REV NO
	13-10-2026	REV 00
1.		

NOTE :

GA DRAWING
THIS DRAWING IS ONLY FOR CLIENT APPROVAL.

SPECIAL INSTRUCTION'S :

This drawing & design is the property of NIHVA TECHONOLOGIES PVT. LTD. Not to be sold or copied to any other concern

TITLE - ROOF AUTOMATION


DWG NO - NTPL-

NIHVA TECHNOLOGIES PVT.LTD.PUNE
Website - www.nihva.com


	NAME	SIGNATURE	DATE
DRAWN	V.W.		13-10-2026
CHK'D	S.P.		15-10-2026
APPV'D	V.T.		15-10-2026

PRODUCT - C SHAPE RECTRACTABLE ROOF
CLIENT NAME - MANGAL ELECTRICALS.
SITE LOCATION - JAIPUR.
MATRIAL - QTY - 1
If any queries contact - info@nihva.com
PROJECTION METHOD:
SCALE :
ALL DIMENSION ARE IN mm A2


DRAWING

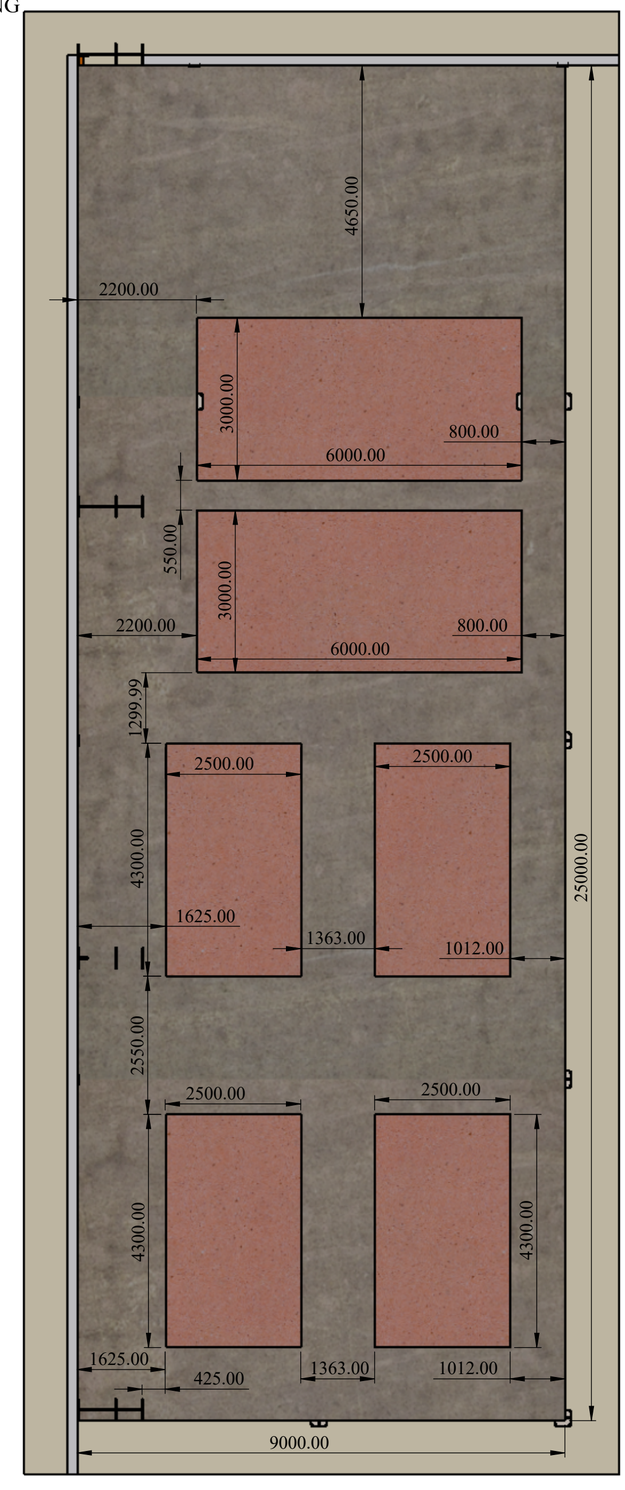


T.V.

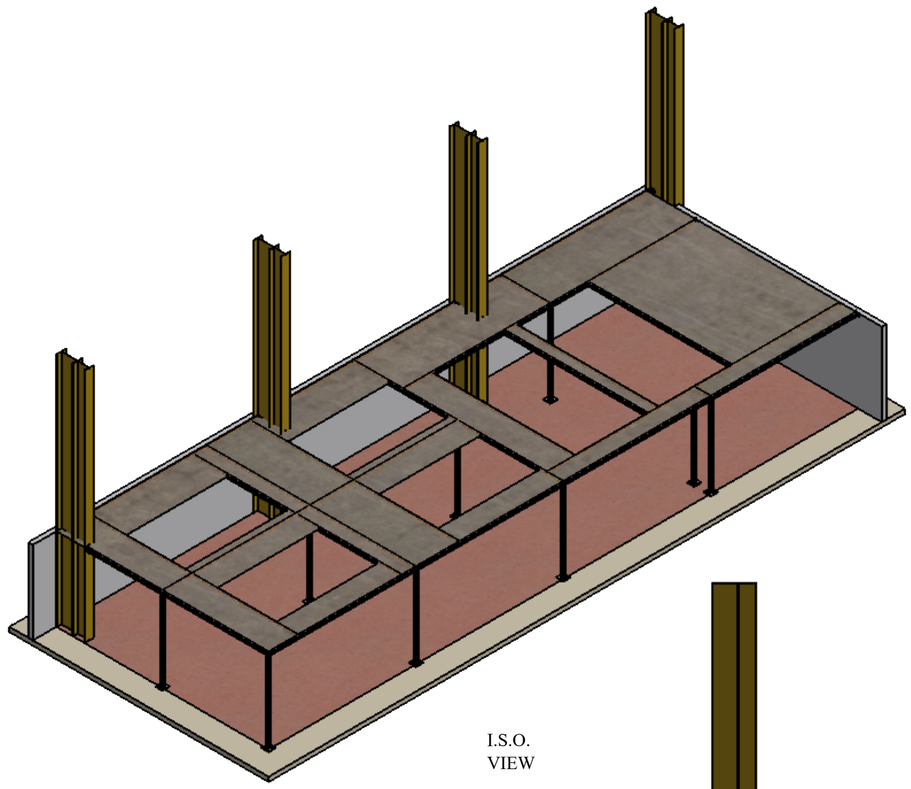

I.S.O.
VIEW

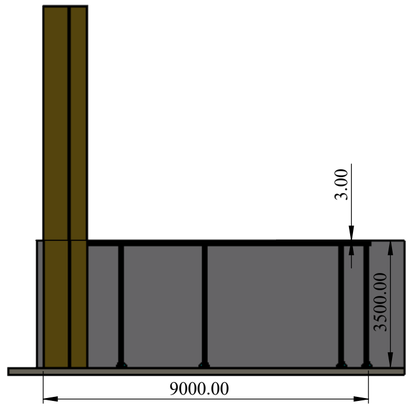

F.V.

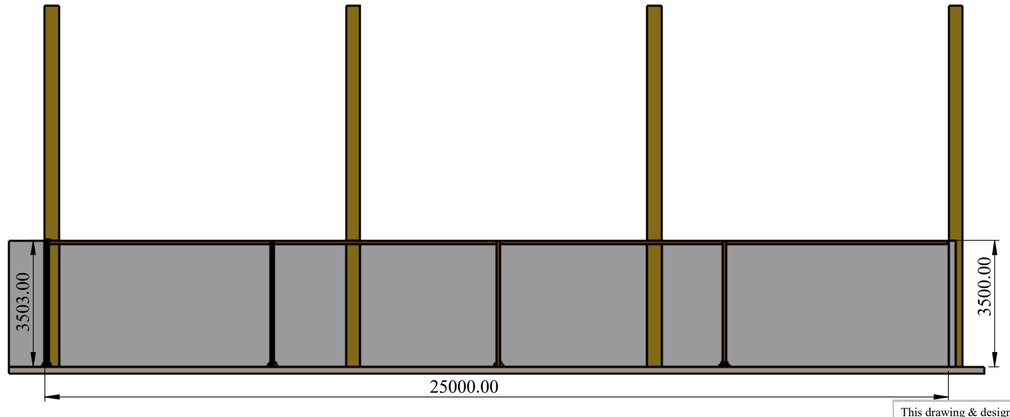

S.V.

REV DESCRIPTION	DATE	REV NO
	13-10-2026	REV 00
1.		

NOTE :

BASE STRUCTURE

SPECIAL INSTRUCTION'S :

This drawing & design is the property of NIHVA TECHONOLOGIES PVT. LTD. Not to be sold or copied to any other concern

TITLE - ROOF AUTOMATION

DWG NO - NTPL-

NIHVA TECHNOLOGIES PVT.LTD.PUNE
Website - www.nihva.com

	NAME	SIGNATURE	DATE
DRAWN	V.W.		13-10-2026
CHK'D	S.P.		15-10-2026
APPV'D	V.T.		15-10-2026

PRODUCT - C SHAPE RECTRACTABLE ROOF

CLIENT NAME - MANGAL ELECTRICALS.

SITE LOCATION - JAIPUR.

MATRIAL - QTY - 1

If any queries contact - info@nihva.com

ALL DIMENSION ARE IN mm A2

PROJECTION METHOD:

SCALE :

SHEET 2 OF 2