




ELEVATION

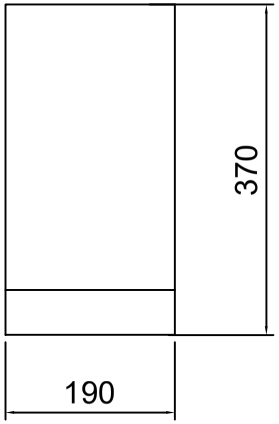


PLAN

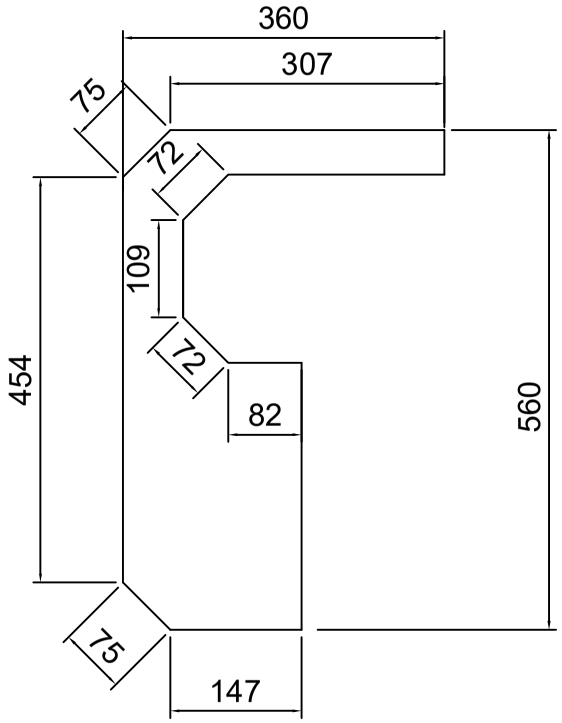

SIDE VIEW

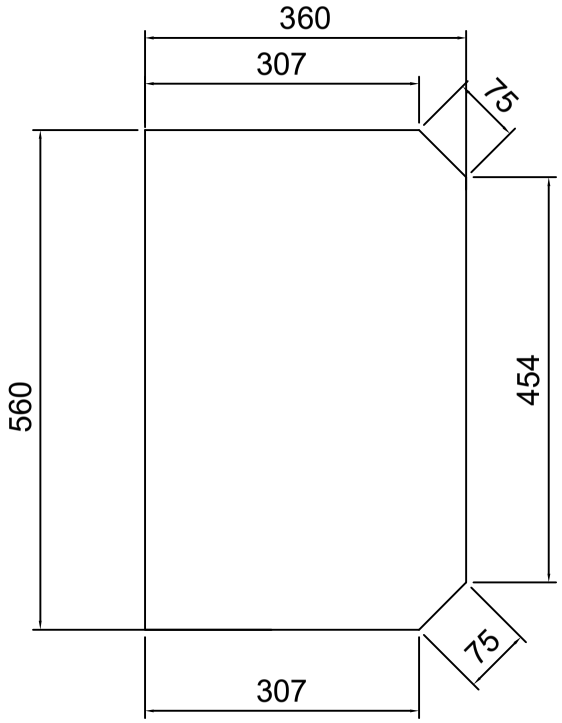

SIDE VIEW

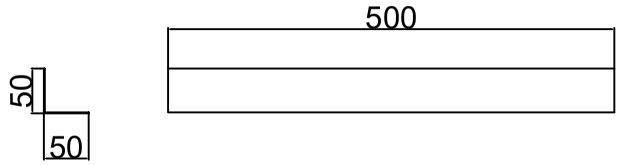

L bracket
50x50x3x500L
QTY:03NOS

NOTE :
1. LEFT SIDE MOTOR DOOR : 1 NO

TOLERANCE - ±5mm

MATERIAL:- Galvanised with Silver paint
THK:- 0.9mm

This drawing & design is the property of NIHVA TECHNOLOGIES. Not to be sold or copied to any other concern.

TITLE	MOTOR COVER LEFT SIDE			NIHVA TECHNOLOGIES PVT. LTD. PUNE Tel : 020 66304033 Email:- info@nihva.com Website:- www.nihva.com
	NAME	SIGN	DATE	
DRAWN	G.I.P.		13.01.22	CLIENT -
CHECK	A.K.		13.01.22	PROJECT - HIGH SPEED DOOR
APPRD.				SITE LOCATION -
If any queries contact : design@nihva.com				DWG. NO. : NIHVA/21-22/VDR/064
ALL DIMENSION ARE IN mm				SCALE: NTS / WT: / REV- 0