




SIDE VIEW

Section A-A

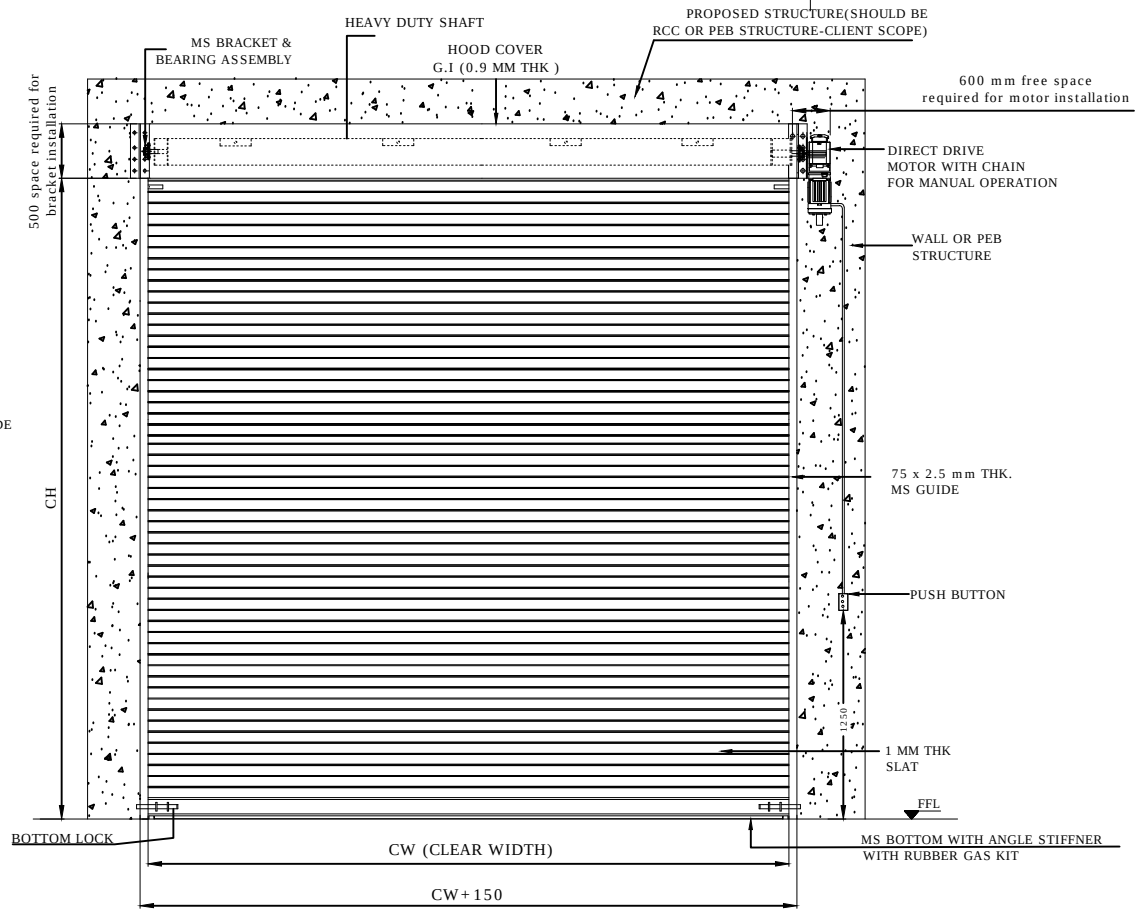


ELEVATION

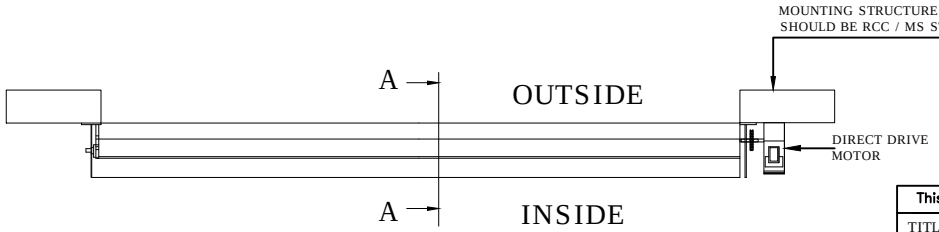

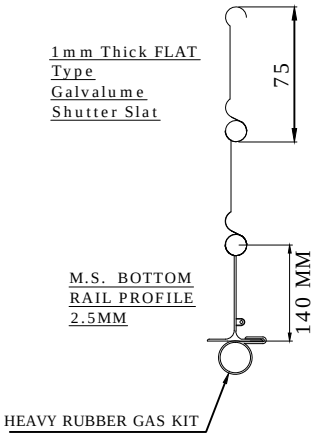

M.S. BOTTOM RAIL PROFILE 2.5MM

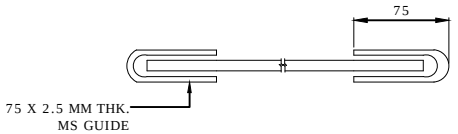

TOLERANCE - ±10mm

CLEAR WIDTH (CW)	CLEAR HEIGHT (CH)	QUANTITY
2500	4000	04 NOS
4000	4000	08 NOS

NOTE-
1. HOOD COVER WILL BE IN GI.
2.ALL CIVIL WORK & STRUCTURE WILL BE IN CLIENT'S SCOPE.

This drawing & design is the property of NIHVA TECHNOLOGIES. Not to be sold or copied to any other concern.

TITLE	MOTORIZED ROLLING SHUTTER GALVALUME		
	NAME	SIGN	DATE
DRAWN	P.A		27.02.20
CHECK	G.J		27.02.20
APPRD.			

NIHVA TECHNOLOGIES PVT. LTD.
NIHVA TECHNOLOGIES PVT. LTD. PUNE
Tel : 020 66304033
Email:- info@nihva.com
Website:- www.nihva.com

CLIENT - Endress + Hauser Flowtec (India) Pvt. Ltd.

PROJECT - Endress + Hauser Flowtec (India) Pvt. Ltd.

SITE LOCATION - AURANGABAD

If any queries contact : design@nihva.com | DWG. NO. : NIHVA/19-20/0222 | REV- 0

ALL DIMENSION ARE IN mm | SCALE: NTS | WT: | SHEET: 01 OF 01