
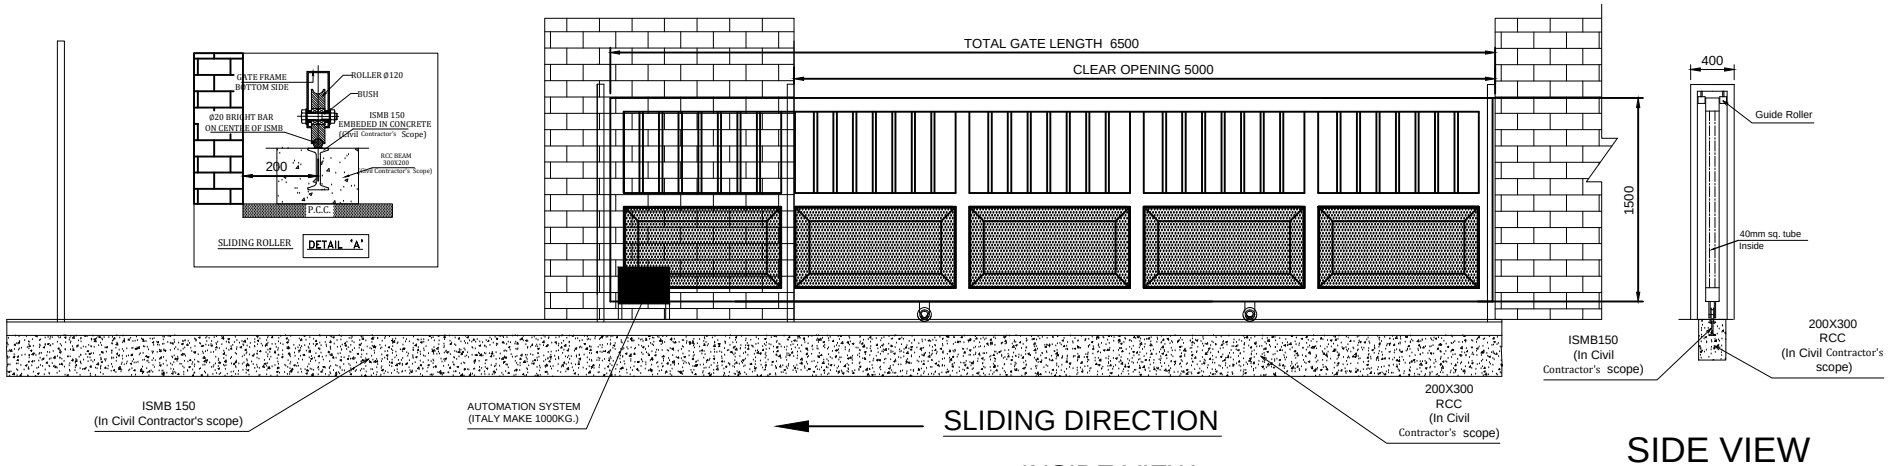



SLIDING DIRECTION


INSIDE VIEW

SIDE VIEW

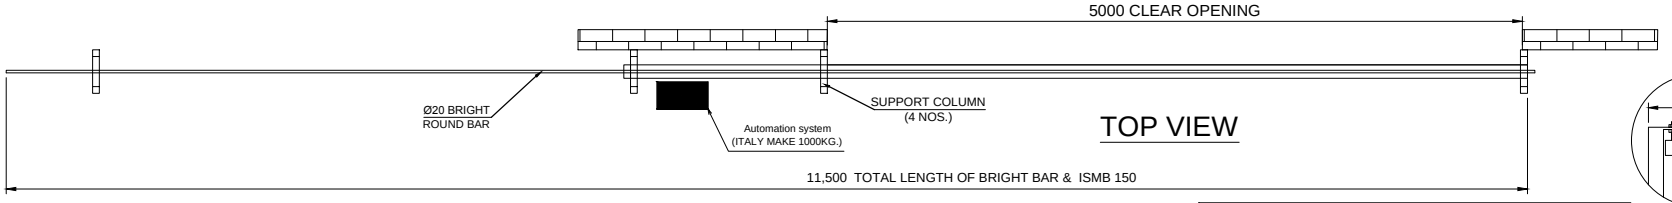

TOP VIEW

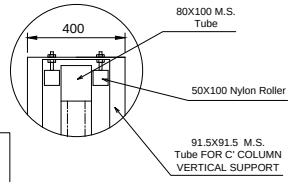

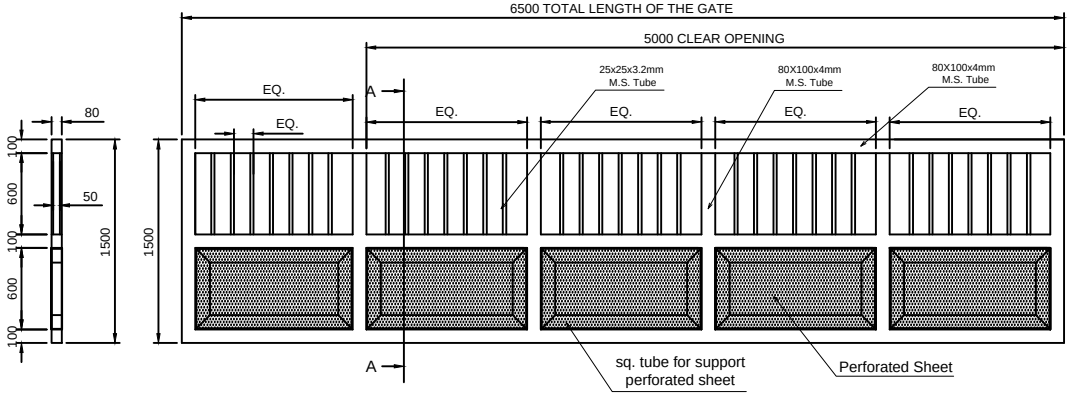

Clear Opening size - 5000X1500mm
Total length of gate - 6500X1500mm
No. Of Column - 4 nos.
Factory paint finish - Red oxide primer coat
NOTE :- *ALL REQ. CIVIL WORK WILL BE IN YOUR CONTRACTOR'S SCOPE.

☑ FINAL CERTIFIED

This drawing & designing is the property of NIHVA TECHNOLOGIES. Not be sold or copy to any other concern.

TITLE	MOTORIZED SLIDING GATE	
	SIGN	DATE
DRAWN	ABHIJIT	28/10/15
CHECK	ANIL	28/10/15
REV.	03	
APPROVAL		
If any queries contact : projects@nihva.com		
ALL DIMENSION ARE IN mm		

NIHVA TECHNOLOGIES PVT. LTD.
NIHVA TECHNOLOGY PVT. LTD. PUNE
Tel : 020 66304033
Email:- info@nihva.com
Website:- www.nihva.com

CLIENT - REWARD CONSTRUCTION
PROJECT - GIVAUDAN
SITE - RANJANGAON MIDC
DWG. NO. : NIHVA/15-16/104
SCALE: 01 | WT: | SHEET: 01 OF 01