

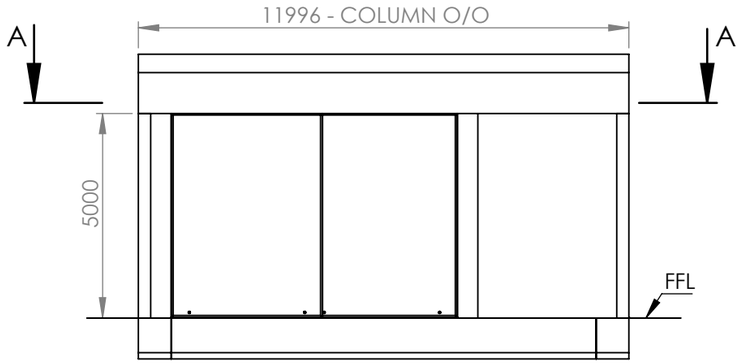



CLOSED POSITION

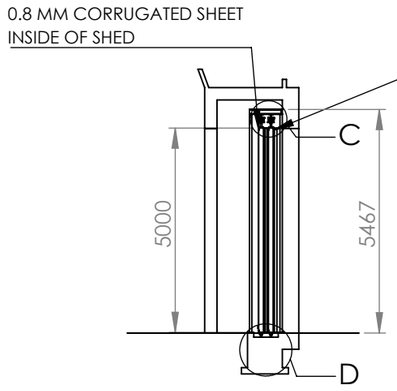

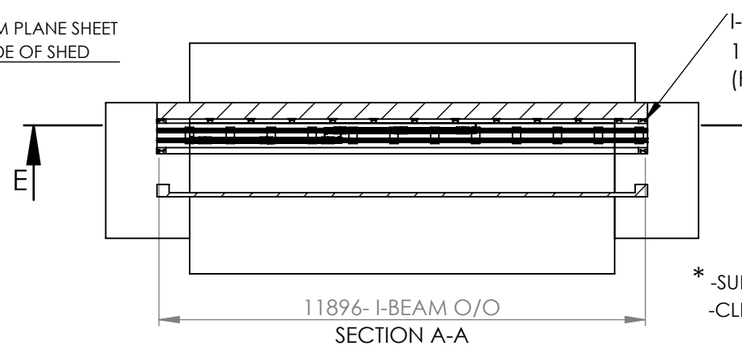



SECTION A-A

* -SUBJECT TO CHANGE AS PER SITE CONDITIONS
-CLIENT SCOPE

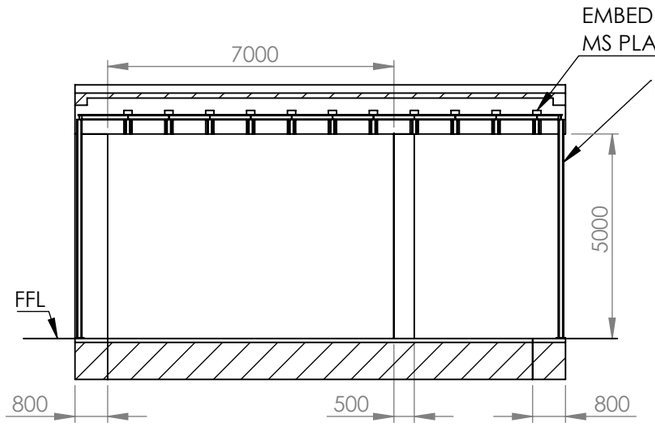


SECTION E-E

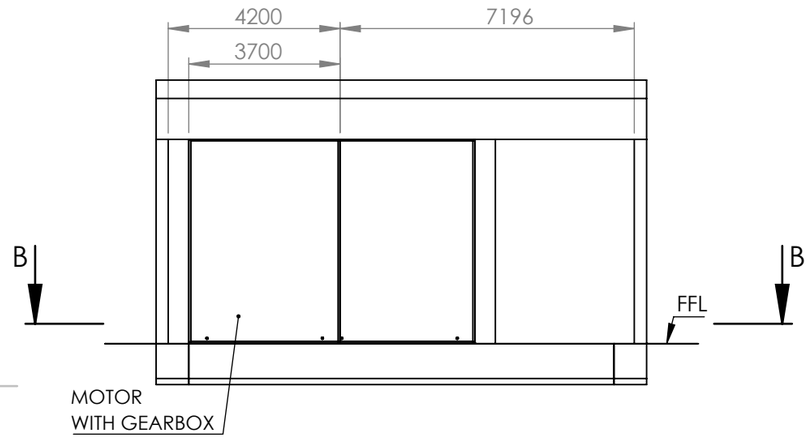


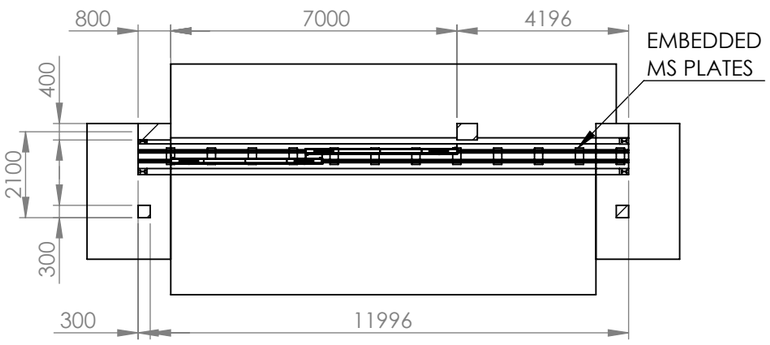


SECTION B-B

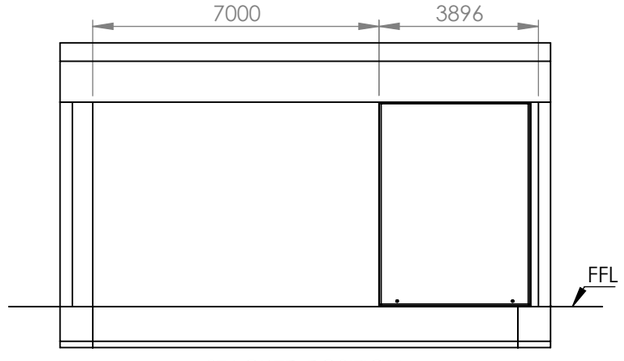


STACKED POSITION

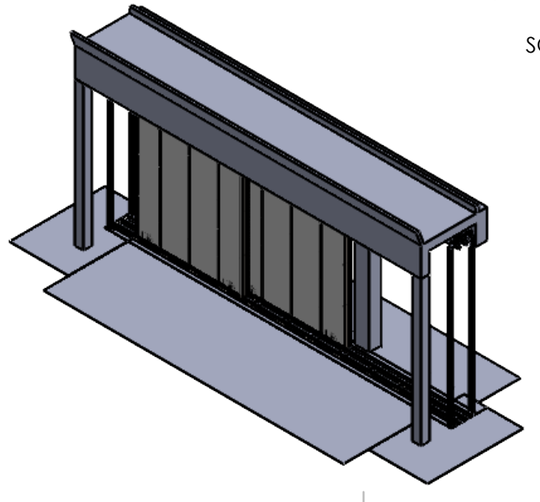

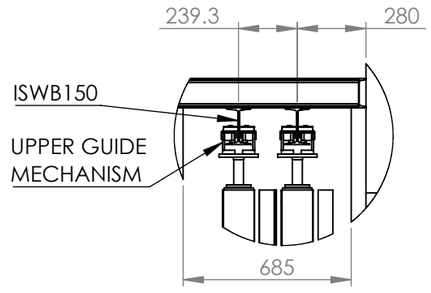

DETAIL C
SCALE 1 : 25

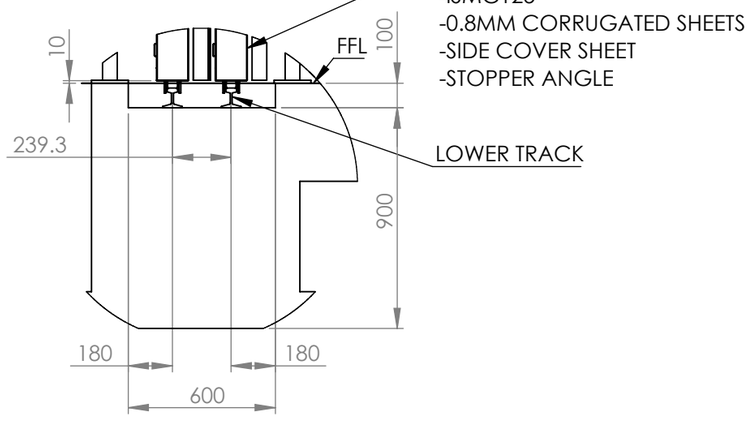

DETAIL D
SCALE 1 : 25

TITLE :	**HANGING SLIDING DOOR**		
	NAME	**SIGN**	**DATE**
DRAWN	BHARATI SABALE		14-02-2025
CHK'D	SURAJ WARALE		14-02-2025
APPV'D	VIJAY T		14-02-2025
	DIMENSIONS ARE IN MILLIMETERS		

NIHVA Technologies Pvt. Ltd.

NIHVA TECHNOLOGIES PVT LTD

CLIENT NAME : ISRO

PRODUCT NAME : HANGING SLIDING DOOR

SITE LOCATION : ALUVA, KERALA

DWG NO. GA

A3

REVISION : 1

SCALE:

SHEET 1 OF 1