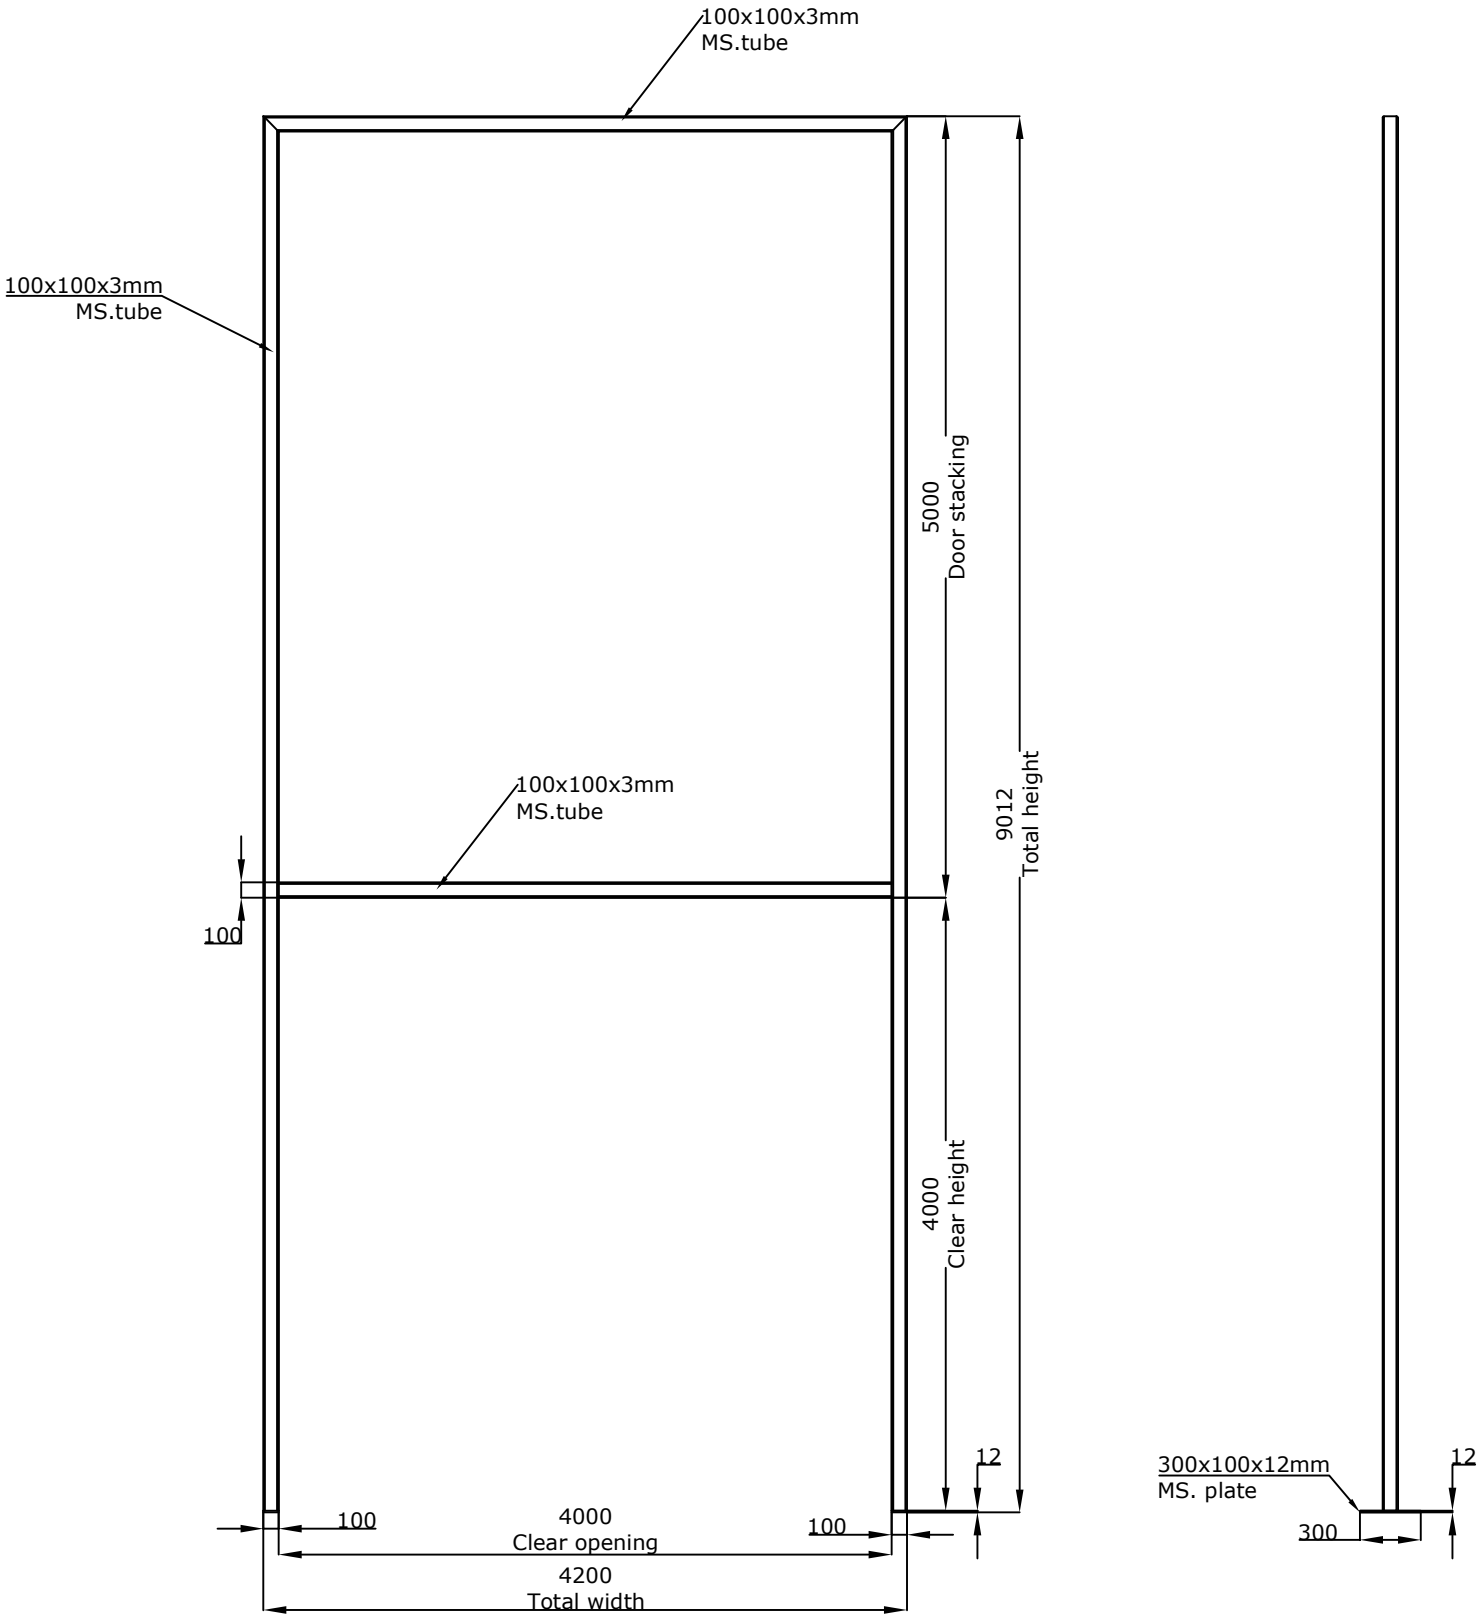


Note :-

1. All dimension are in mm
2. Support in client scope .

CLEAR WIDTH CW	CLEAR HEIGHT CH	QTY
4000 mm	4000 mm	01 NOS

This drawing & design is the property of NIHVA TECHNOLOGIES. Not to be sold or copied to any other concern.

TITLE :- SECTIONAL DOOR STRUCTURE

NIHVA TECHNOLOGIES PVT. LTD.

	NAME	SIGN	DATE
DRAWN	S.J		17.06.2024
CHECK	B.B		17.06.2024
APPROVAL	V.T		17.06.2024

If any queries contact : design@nihva.com

ALL DIMENSION ARE IN mm

CLIENT - FOURTH DIMENSION GROUP

PROJECT -

SITE LOCATION -

DWG. NO. : NIHVA/24-25/FDG/2406001

SCALE: NTS | WT: | SHEET: 01 OF 01