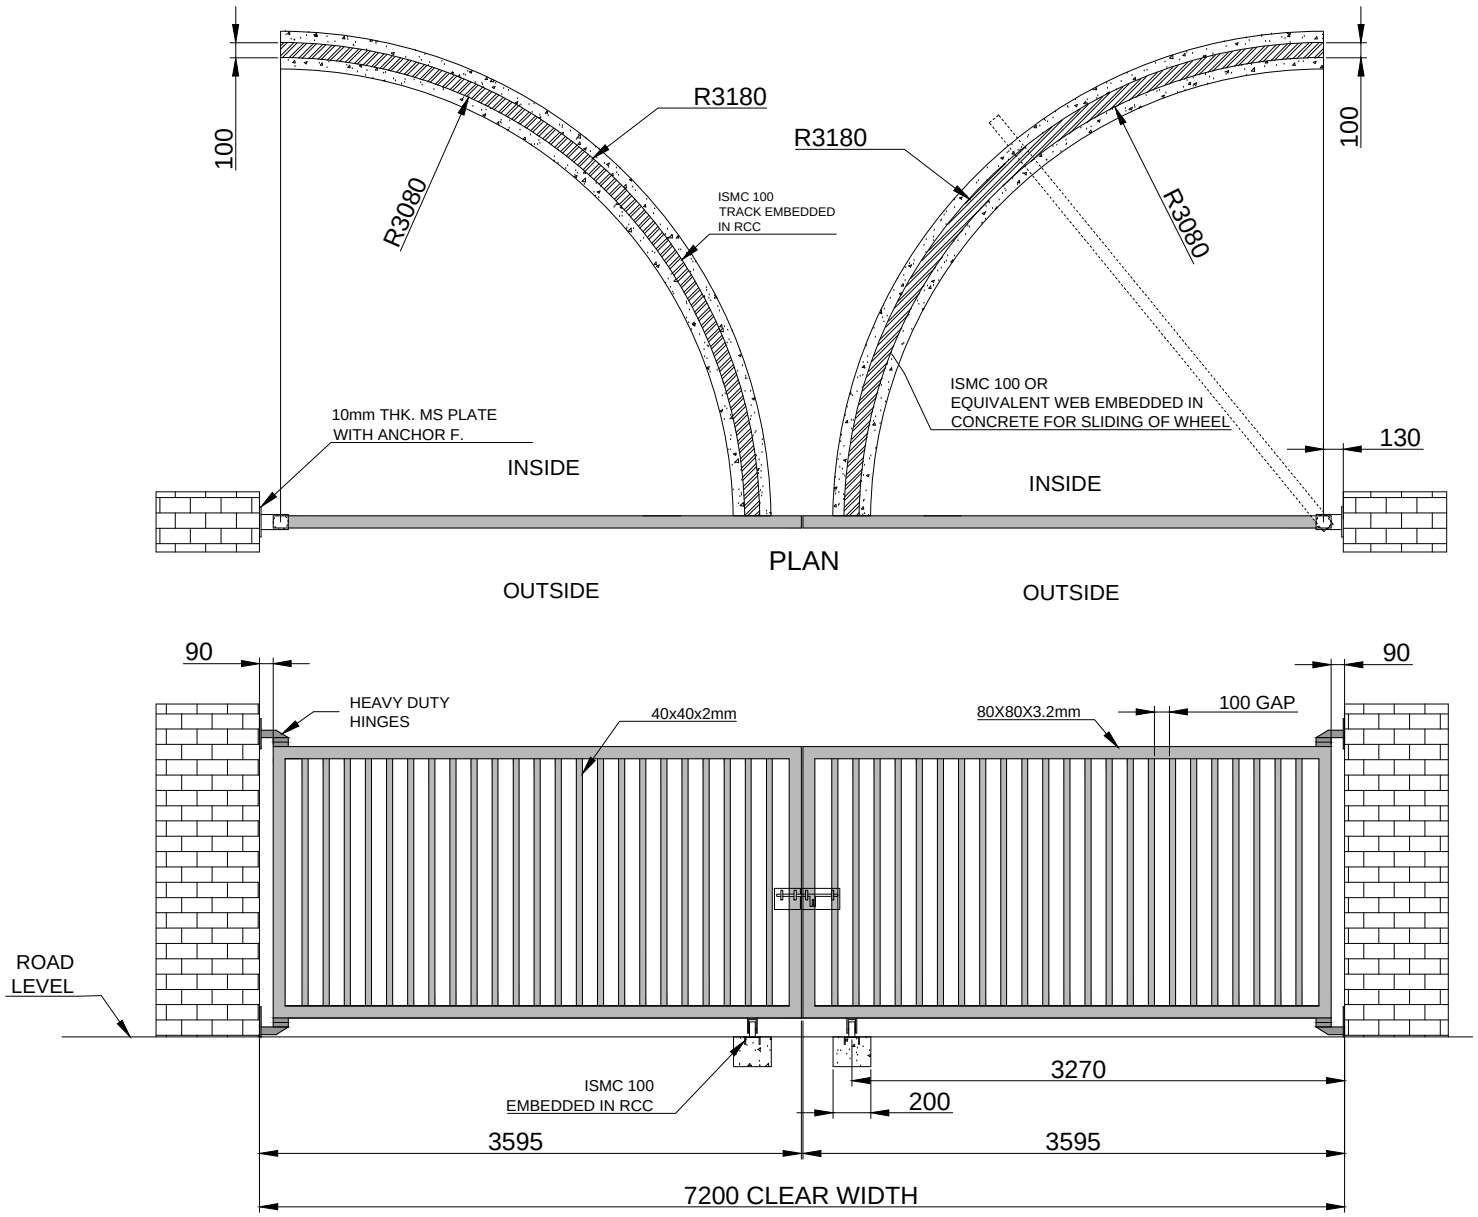



ELEVATION

TOLERANCE- ±10mm

DIMENSION :

| CLEAR WIDTH | CLEAR HEIGHT | QUANTITY |
|---|---|---|
| 7200mm | 1800mm | 1 NOS |

MATERIAL:

| SR NO | TUBE SPECIFICATION | |
|---|---|---|
| 1 | MS 80X80X3.2mm | OUTER FRAME |
| 2 | MS 40X40X2mm | INNER PATTERN |

THICKNESS :

NOTE-
1. ALL REQUIRED CIVIL WORK WILL BE IN CLIENTS SCOPE.
2. ONE COAT OF RED OXIDE & TWO COAT OF APPROVED RAL SHADE WILL BE GIVEN TO THE GATE.

NIHVA TECHNOLOGIES PVT. LTD.
NIHVA TECHNOLOGIES PVT. LTD. PUNE
Email:- info@nihva.com
Website:- www.nihva.com

TITLE:

# MANUAL SWING GATE 7.2X1.8m GATE NO 7

CLIENT'S APPROVAL :

CLIENT -

PROJECT -

SITE LOCATION -

DWG. NO. : NIHVA/17-18/VDR/0169 | REV-0

SCALE: NTS | WT: | SHEET:1 OF 1

| NAME | SIGN | DATE |
|---|---|---|
| DRAWN: SURAJ | | 04-11-2017 |
| CHECK : OMKAR | | 04-11-2017 |
| APPD : SHEKHAR | | 04-11-2017 |

If any queries contact : projects@nihva.com

NOTE: ALL DIMENSIONS ARE IN mm

THIS DRAWING & DESIGN IS THE PROPERTY OF NIHVA TECHNOLOGIES. NOT TO BE SOLD OR COPIED TO ANY OTHER CONCERN.