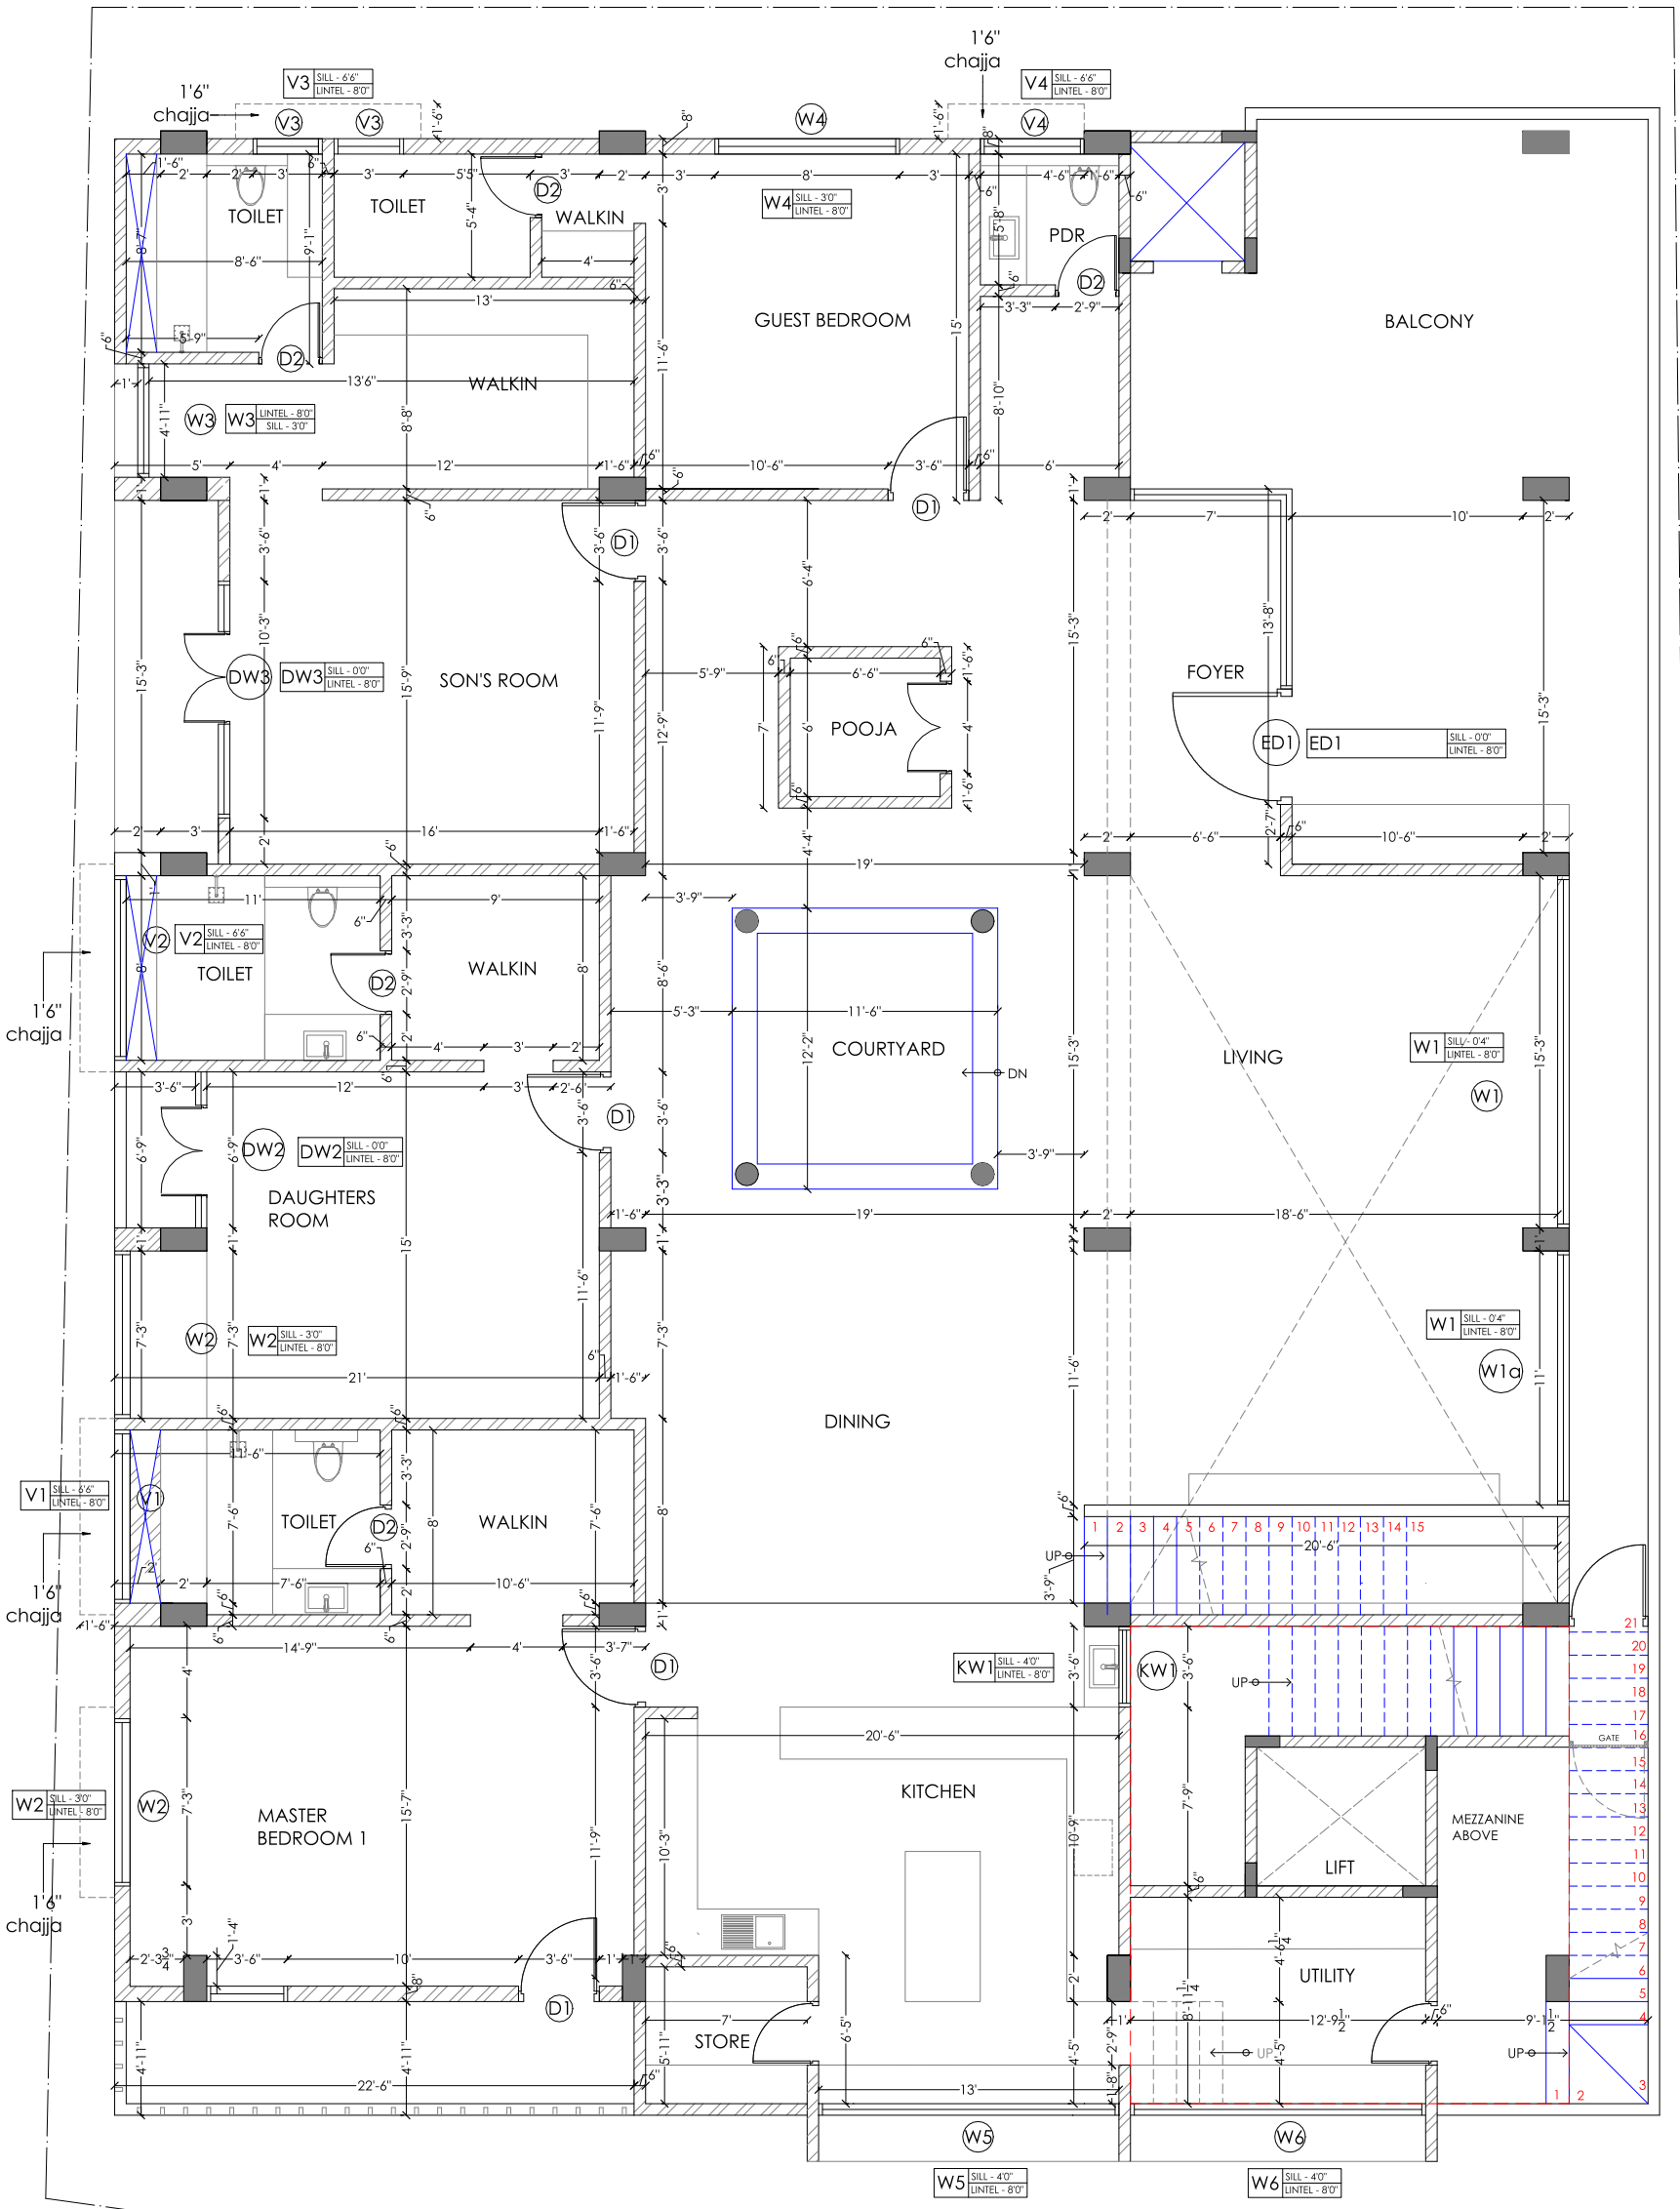


6" LIGHT WEIGHT BLOCK WALL (USED FOR PARTITION AND AS ROOM SEPERATION WALLS)

8" SOLID BLOCK WALL (BUILT ON BEAM OR EXTERNAL WALLS ONLY AS INDICATED IN DRAWING)

NOTE :

1) ALL SILL AND LINTELS CONSIDERED FROM FLOOR FINISH LEVEL (FFL)

2) FLOOR FINISH TO BE CONSIDERED ATLEAST 3" FROM RAW SLAB

3) LINTELS FOR DOORS TO BE 8" FROM FFL


NOTES

1.All dimensions in feet and inches. Dimensions to be read not measured.
2.Ambiguities and discrepancies shall be brought to the notice of theArchitects prior to execution.
3.For details such as doors,windows,grills,gates,handrails, railings, flooring pattern etc. refer relevant Architectural drawings.
4.These drawings shall be correlated and read in conjuction with relevant consultant's approved drawings for structural members, services such as plumbing, sanitary, electrical, airconditioning, ventilation, rainwater drainage & waterproofing and landscaping.
5.All levels are in mm and are unfinished levels unless specified otherwise.
6.All roof slabs to have waterproofing and insulation treatment as per services consultant's drawing.
7.Dowels to be left in stairs for fixing of handrails later.
8.Concreting in toilets to be co-ordinated with detailed toilet drawings.
9.Headroom in all stairs to be checked prior to concreting.

HOUSE NITHIN		
BANGALORE	GROUND FLOOR PLAN	
DRG. No. -		N
SCALE - NTS		
ISSUED - 01-03-24		
REVISON DATE -		R0
DRAWN BY- POOJA	GFC	

ARCHITECT:

DESIGN INTEGRATUS ARCHITECTS
2ND FLOOR ,
142, INFANTRY ROAD,
BANGALORE – 560001
PH : 9986074972

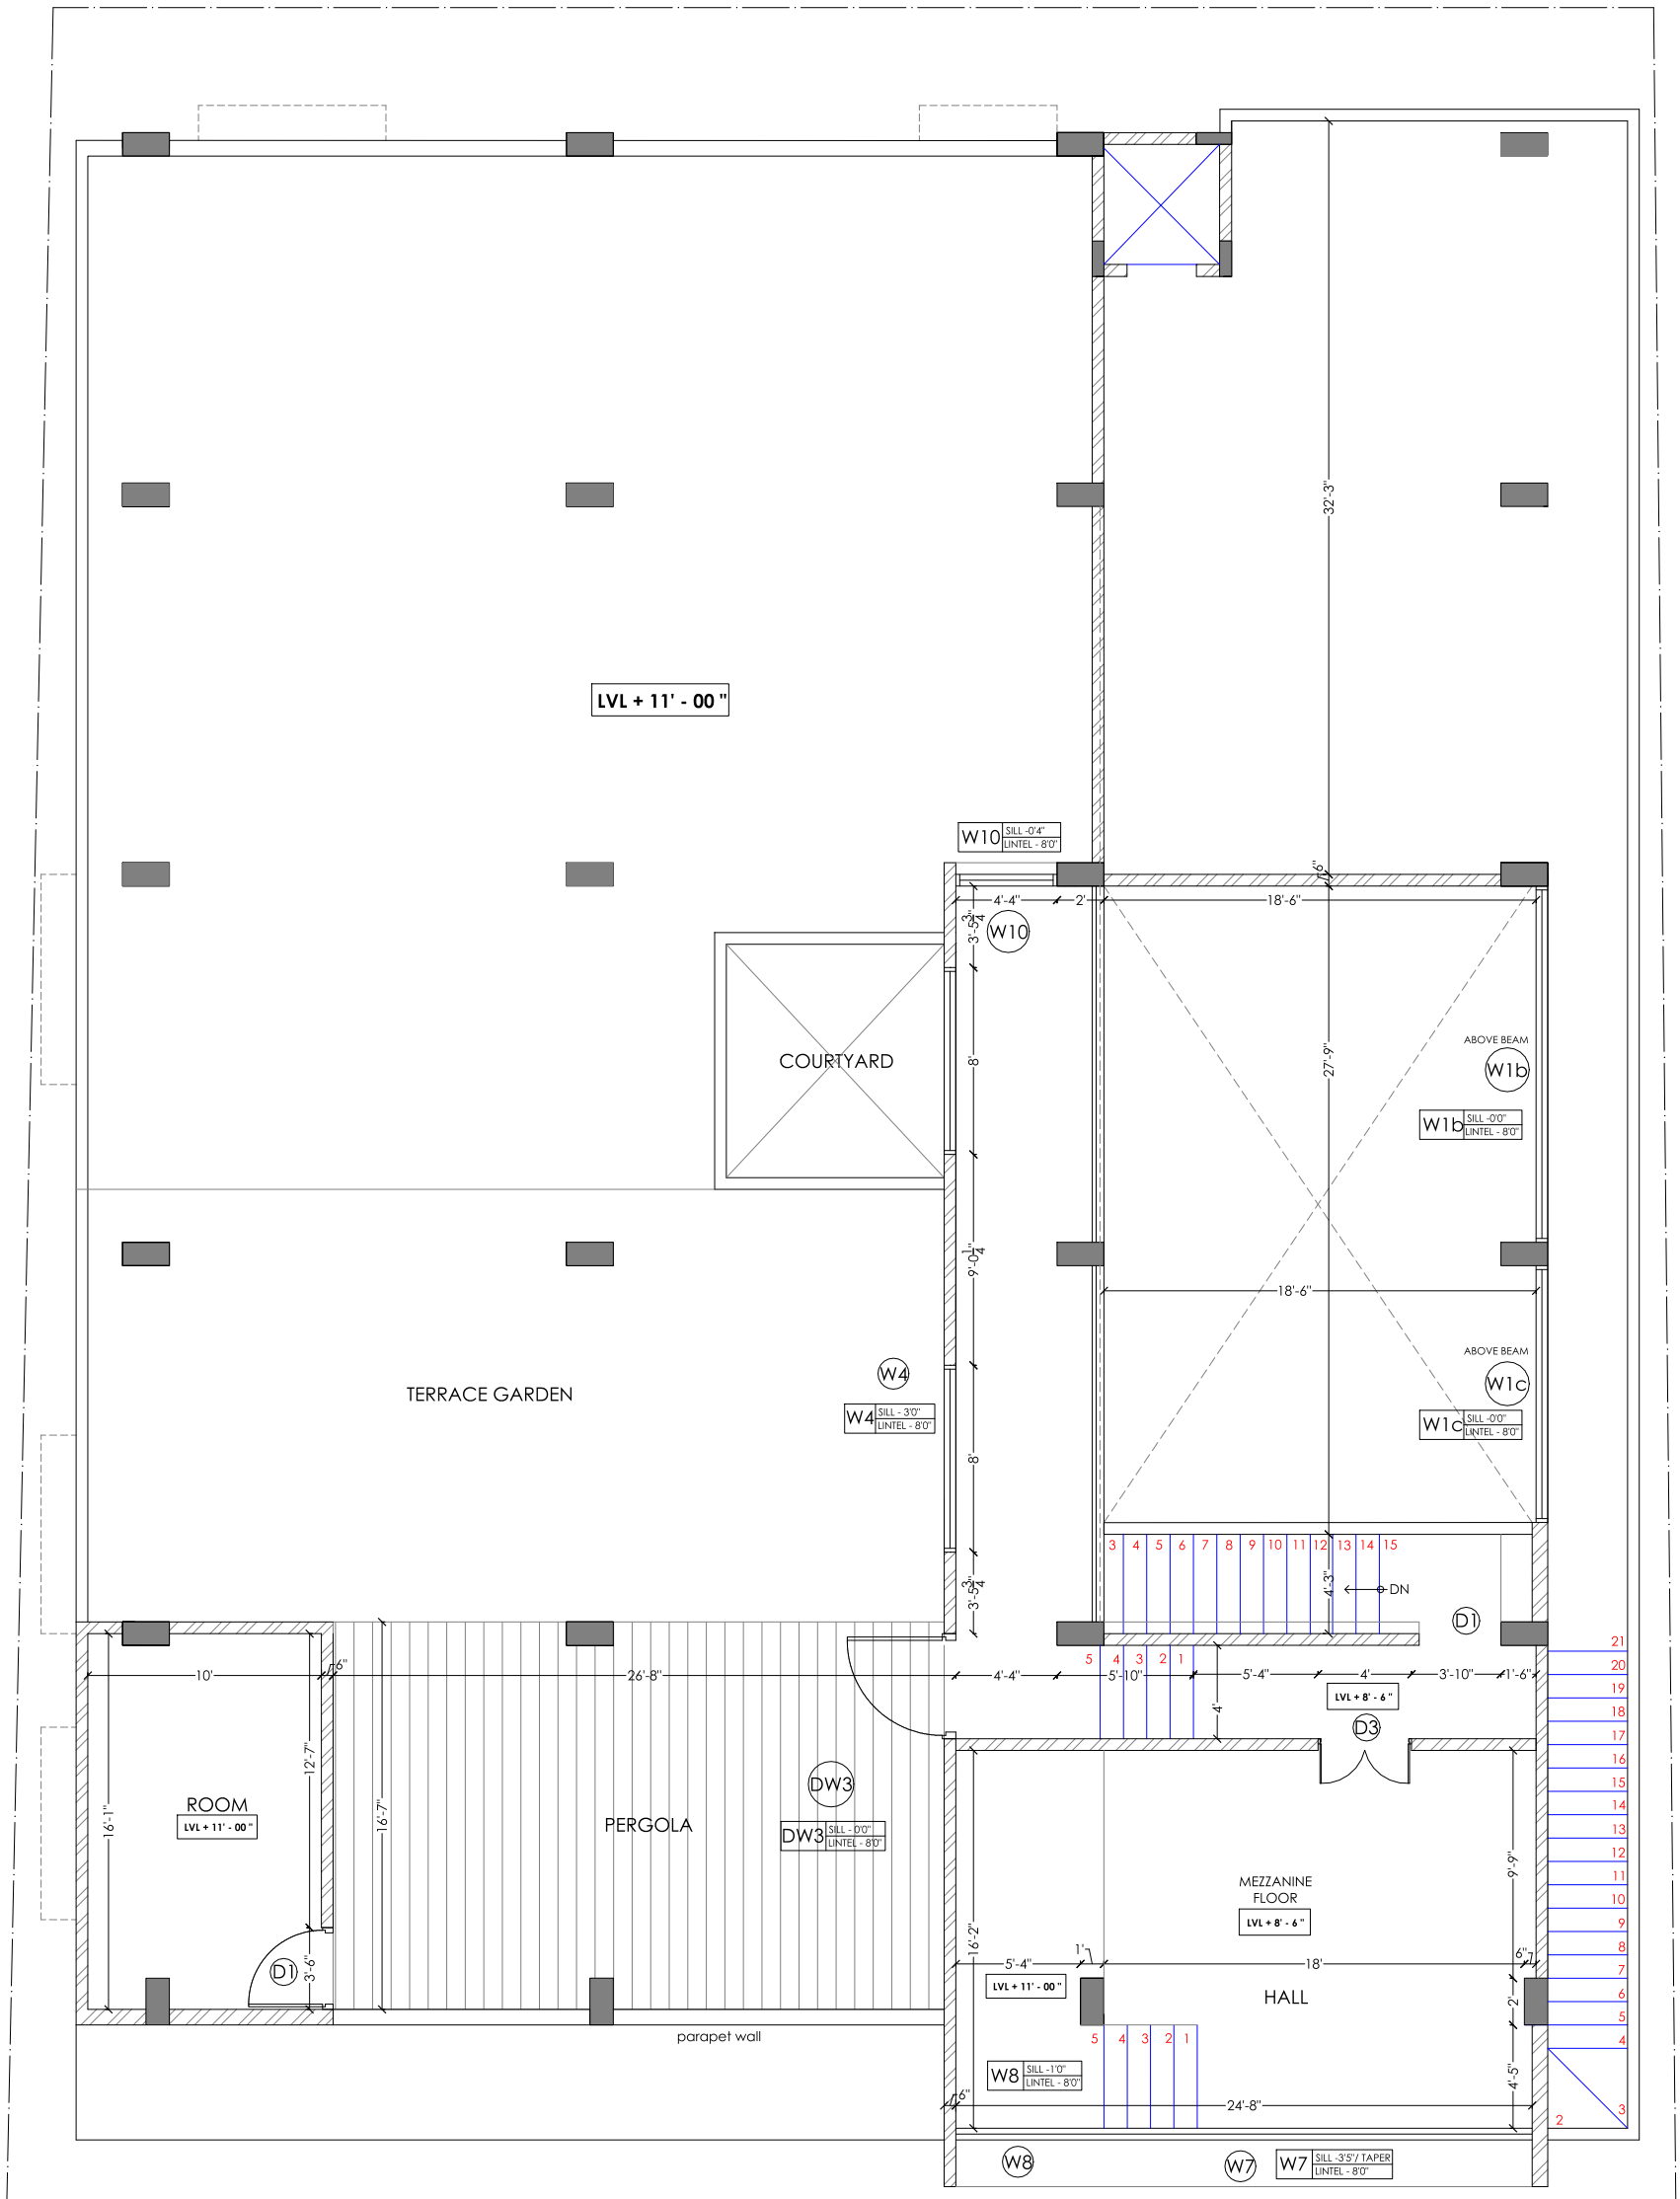

6" LIGHT WEIGHT BLOCK WALL (USED FOR PARTITION AND AS ROOM SEPERATION WALLS)

8" SOLID BLOCK WALL (BUILT ON BEAM OR EXTERNAL WALLS ONLY AS INDICATED IN DRAWING)

NOTE :

1) ALL SILL AND LINTELS CONSIDERED FROM FLOOR FINISH LEVEL (FFL)

2) FLOOR FINISH TO BE CONSIDERED ATLEAST 3" FROM RAW SLAB

3) LINTELS FOR DOORS TO BE 8" FROM FFL

NOTES

1.All dimensions in feet and inches. Dimensions to be read not measured.
2.Ambiguities and discrepancies shall be brought to the notice of theArchitects prior to execution.
3.For details such as doors,windows,grills,gates,handrails, railings, flooring pattern etc. refer relevant Architectural drawings.
4.These drawings shall be correlated and read in conjuction with relevant consultant's approved drawings for structural members, services such as plumbing, sanitary, electrical, airconditioning, ventilation, rainwater drainage & waterproofing and landscaping.
5.All levels are in mm and are unfinished levels unless specified otherwise.
6.All roof slabs to have waterproofing and insulation treatment as per services consultant's drawing.
7.Dowels to be left in stairs for fixing of handrails later.
8.Concreting in toilets to be co-ordinated with detailed toilet drawings.
9.Headroom in all stairs to be checked prior to concreting.

HOUSE NITHIN		
BANGALORE	FIRST FLOOR PLAN	
DRG. No. -		N
SCALE - NTS		
ISSUED -		
REVISON DATE -01-03-24		R2
DRAWN BY- POOJA	GFC	

ARCHITECT:

DESIGN INTEGRATUS ARCHITECTS
2ND FLOOR ,
142, INFANTRY ROAD,
BANGALORE – 560001
PH : 9986074972