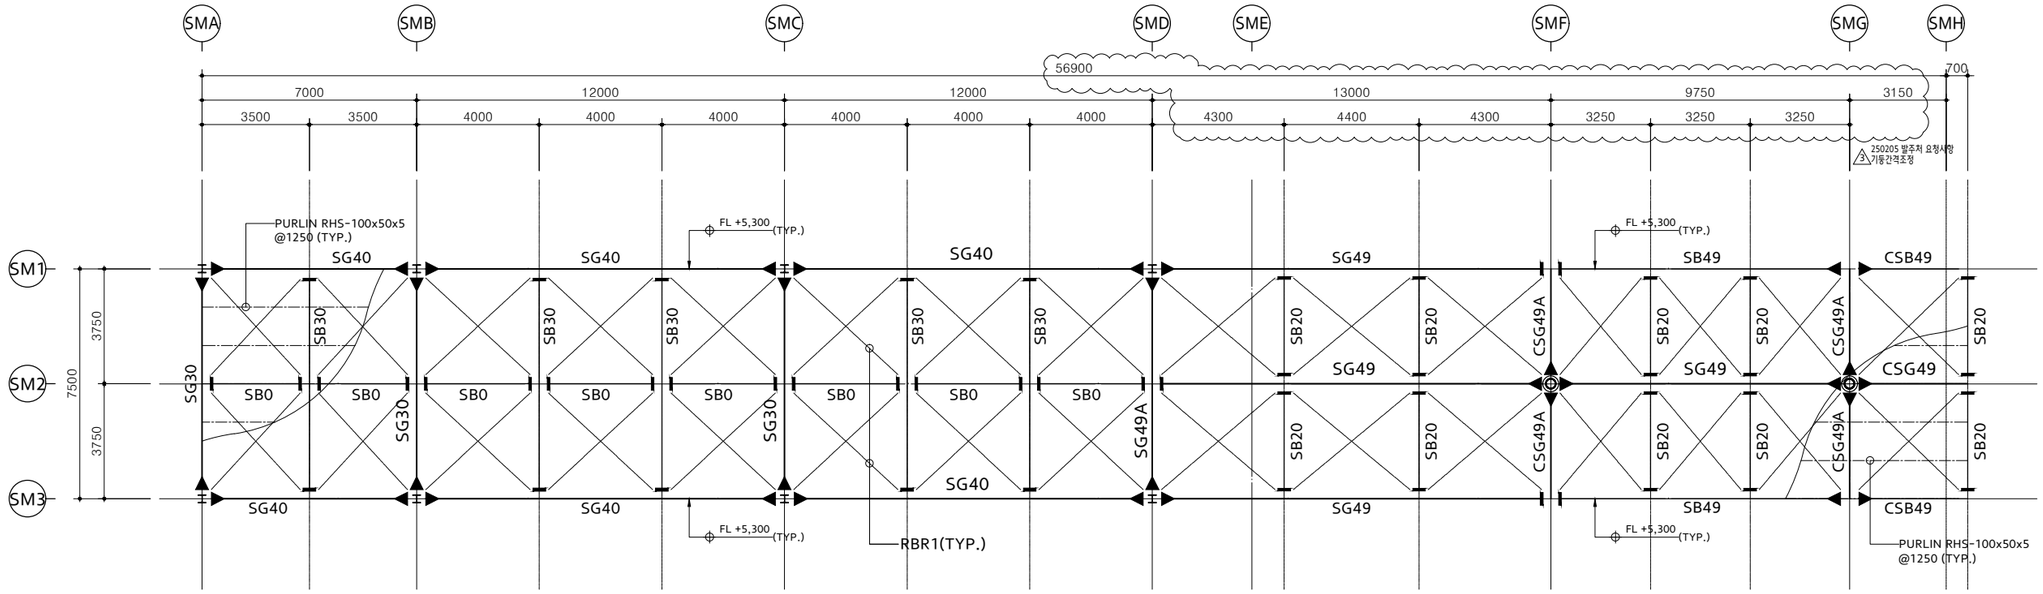


1 ROOF FRAMING PLAN

SCALE : 1/100

KEY PLAN

NOTE

■ MATERIAL STRENGTH

1. CONCRETE
   1) STRUCTURAL CONCRETE
   - fck = 30 MPa (Cubic Strength)
   - fck = 24 MPa (Cylinder Strength)
   2) LEAN CONCRETE
   - fck = 15 MPa (Cubic Strength)
   - fck = 12 MPa (Cylinder Strength)
2. REINFORCING BAR
   - fy = 415 MPa (IS Fe415)
3. STEEL
   1) ALL STEEL MEMBERS
   EXCEPT THOSE SPECIFIED BELOW
   - E250 (Fy = 230~250 MPa, Fu = 410 MPa)
   2) RECT.HSS : IS YST 240
   - YST 240(Fy=240MPa, Fu=410MPa)
4. HIGH STRENGTH BOLT
   - KS F10T TS BOLT OR
   EQUIVALENT TO GRADE 10.9
   (Fy = 900MPa, Fu = 1,000MPa)
5. ANCHOR BOLT
   - IS GRADE 4.6 (Fu = 400 MPa)
6. CONNECTION OF STEEL STRUCTURES
   ▶— : FIX CONNECTION & GIRDER CONNECTION
   —| : HINGE CONNECTION

■ NOTE

1. ALL DIMENSIONS AND ELEVATIONS ARE IN MILLIMETERS UNLESS OTHERWISE NOTED.
2. CLEAR COVER TO MAIN REINFORCEMENT
   1) FOOTING : 40mm (CONSIDERING LEAN CONCRETE)
   2) COLUMN : 40 mm (CONSIDERING FORM)
   3) BEAM : 40 mm (CONSIDERING FORM)
   4) SLAB : 20 mm (CONSIDERING LEAN CONCRETE)
3. ALLOWABLE SOIL BEARING CAPACITY
   1) Fe = 100 kN/m² (SFRC SLAB & S.O.G SLAB)
   2) Fe = 150 kN/m² (FOUNDATION)
4. ALLOWABLE SOIL BEARING CAPACITY
   IS IT MAY BE CHANGED DEPENDING ON THE SITE AND SOIL CONDITIONS.

■ MEMBER LIST

NAME	MEMBER	GRADE
SB0	ISA 100x100x8	E250
SB20	UB 203X133X25	
SB30	UB 305X165X40	
CSB49	BH 450X200X8X16	
SG30	UB 305X165X40	
SG40	BH 400X150X8X12	
SG49,SG49A CSG49,CSG49A	BH 450X200X8X16	

■ MEMBER LIST

NAME	MEMBER	GRADE
RBR1	ROD BAR D16	E250
	(Turn buckle)	
PURLIN	RHS-100x50x5@1250	E250
	(MIN 2 SPAN CONTINOUS)	

REV.	DESCRIPTION	DRAWN	DATE
3	CD Rev.3	OH.J.S	2025. 02.14
2	CD Rev.2	OH.J.S	2024. 11.29
1	CD Rev.1	OH.J.S	2024. 10.18
0	CONSTRUCTION DRAWING	OH.J.S	2024. 07.30
A	DESIGN DEVELOPMENT	OH.J.S	2024. 06.28

CLIENT

HYUNDAI

ARCHITECTS & ENGINEERS

JUNGLIM ARCHITECTURE

PROJECT TITLE

PUNE HMI PROJECT

DRAWING TITLE

[MAIN SECURITY OFFICE]
ROOF FRAMING PLAN

SCALE	DRAWN	CHECKED	REVIEWED	APPROVED	APPROVED
A1: 1/100 A3:1/200	OH.J.S	HONG.G.D	LEE.S.L	HEC INDIA	PARK.T.S
DATE					
14 FEB,2025					

MAIN CONTRACTOR

HEC INDIA LLP

DRAWING NO. WA-IPB-645-S-2002

REV. 3

A1 SIZE (841mm x 594mm)