SAFETY RAILING	900 MM HT
POWER PACK	3HP, 3PH
MAX HT	1700 MM
LIFT HT	1200 MM
SHUT HT	500 MM
PLATFORM SIZE	3000L x 1000W
CAPACITY	1.3 TON

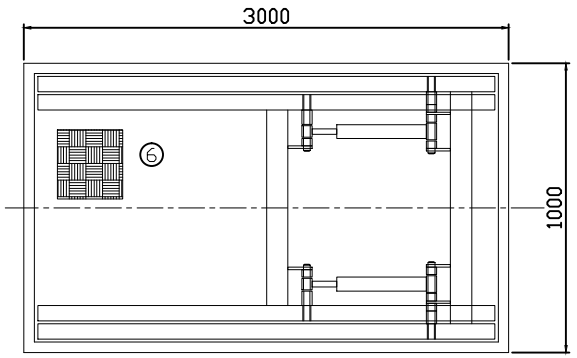

TOP VIEW

SR.NO	ITEM	DESCRIPTION	QTY	MTL
1	TOP FRAME	ISMC 125x65	1 NO	M.S
2	BASE FRAME	ISMC 125x65	1 NO	M.S
3	SCISSOR	RECT. TUBE 122x61x5.4THK	4 NOS	M.S
4	MAINTENANCE STOPPER	RECT. TUBE 80x40x4THK	2 NOS	M.S
5	SAFETY RAILING	PIPE OD27x2.6THK	2 NOS	M.S
6	CHEQ. SHEET	1000x5THKx3000	1 NO	M.S
7	HYDRAULIC CYLINDER	BORE 63 MM	2 NOS	M.S
8	POWER PACK	3HP, 3PH	1 NO	M.S
9	CONTROL PANEL	3HP, 3PH	1 NO	M.S

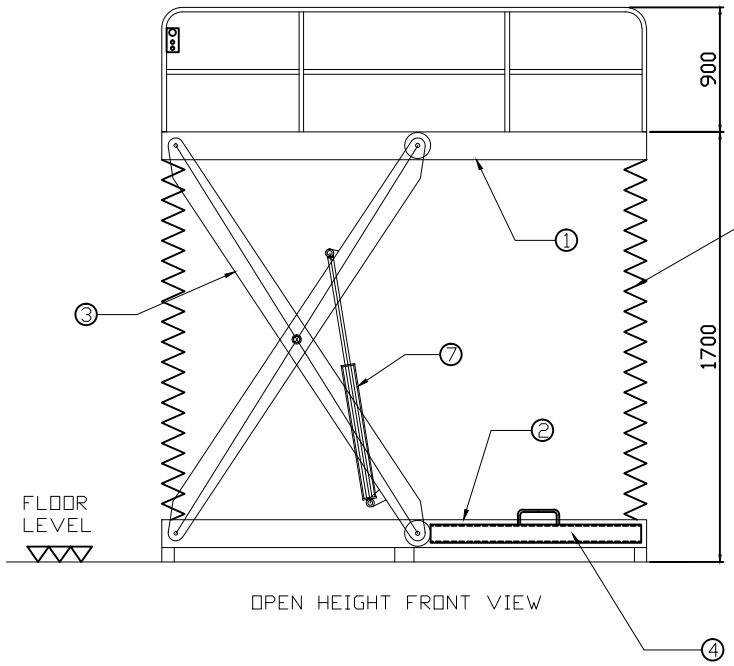

OPEN HEIGHT FRONT VIEW

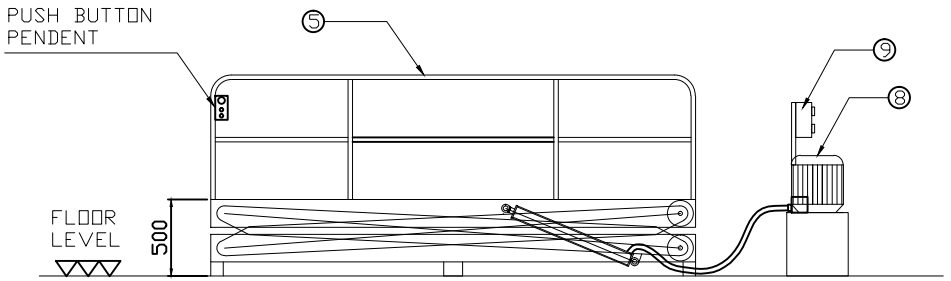

SHUT HEIGHT FRONT VIEW

SCISSOR LIFT QTY : 4 NOS
HOSE & CABLE : 12 MTR'S

REV NO	DRAWN	DATE	REMARK
R02	P.V.A	12.08.19	1. DETAILS ADDED.
R01	P.V.A	10.08.19	1. DETAILS ADDED.

This drawing & design is the property of NIHVA TECHNOLOGIES. Not to be sold or copied to any other concern.

TITLE:- ELECTRO HYDRAULIC SCISSOR LIFT

NIHVA TECHNOLOGIES PVT. LTD.

NIHVA TECHNOLOGIES PVT. LTD. PUNE
Tel : 020 66304033
Email:- info@nihva.com
Website:- www.nihva.com

	NAME	SIGN	DATE
DRAWN	P.V.A		29.07.2019
CHECK	V.M.T		29.07.2019

CLIENT - METROLAB ENGINEERING PVT .LTD
PROJECT -
SITE LOCATION - CHINCHWAD
If any queries contact : design@nihva.com
DWG. NO. : NIHVA/19-20/0065/R02
REV- R02
ALL DIMENSION ARE IN mm
SCALE: NTS
WT:
SHEET: 01 OF 02