




SECTION E
SCALE 1:4

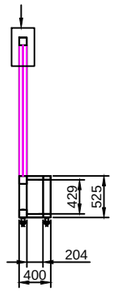


SECTION E

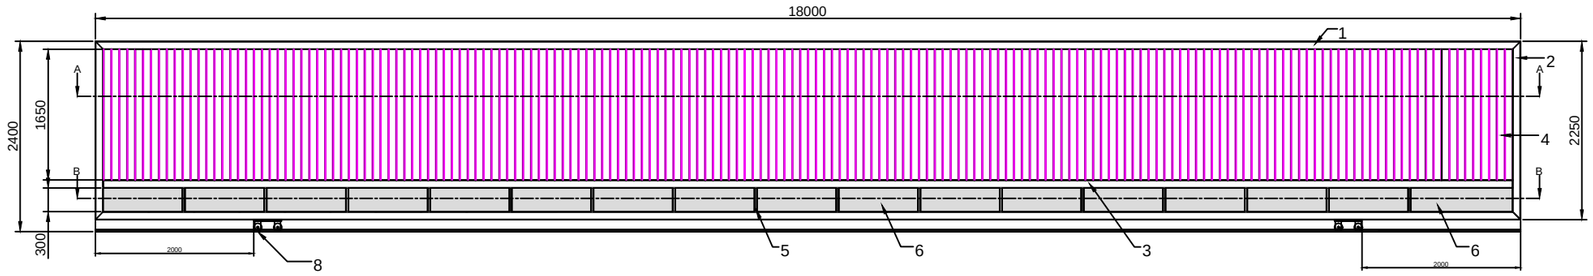


SECTION D

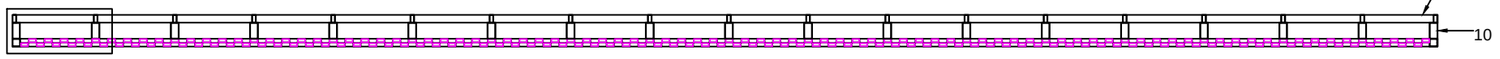


SECTION A-A

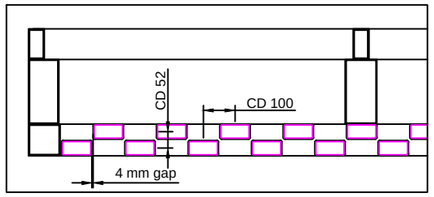

SECTION D
SCALE 1:4

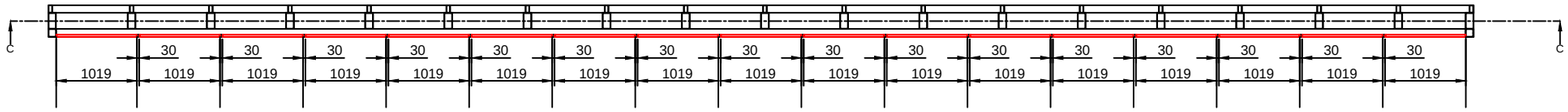

SECTION B-B

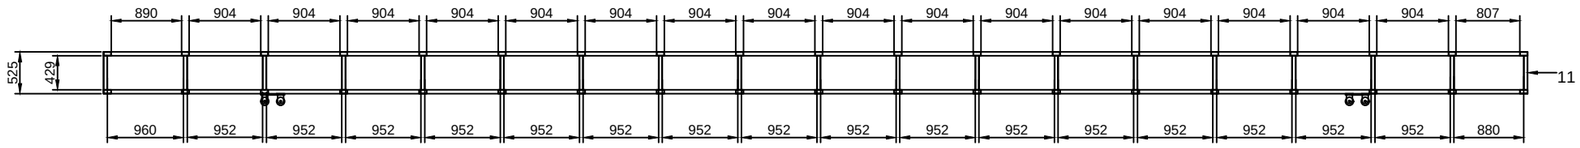

SECTION C-C

SR. NO.	DESCRIPTION	SPECIFICATION	QTY
1	SQ. TUBE	100 X 100 X 4, 18000 LENGTH	2 NOS
2	SQ. TUBE	100 X 100 X 4, 2250 LENGTH	2 NOS
3	SQ. TUBE	100 X 100 X 4, 17800 LENGTH	1 NOS
4	RECT. TUBE	96 X 48 X 3.2, 1650 LENGTH	178 NOS
5	SQ. TUBE	32 X 32 X 2.6, 300 LENGTH	16 NOS
6	MS PERFORATED TRAY	1015 X 298 X 29, 1.5 THK	17 NOS
7	---	---	---
8	WHEEL	4" WHEEL WITH BRACKET	4 NOS
9	RECT. TUBE	96 X 48 X 3.2, 18000 LENGTH	2 NOS
10	RECT. TUBE	96 X 48 X 3.2, 204 LENGTH	38 NOS
11	RECT. TUBE	96 X 48 X 3.2, 429 LENGTH	19 NOS

REV: 01 08-03-2022
1. CHANGED TRAY SIZES.

This drawing & design is the property of NIHVA TECHNOLOGIES. Not to be sold or copied to any other concern.

TITLE
MOTORIZED SLIDING GATE FRAME

	NAME	SIGN	DATE
DRAWN	G.P.		04.03.22
CHECK	A.K.		04.03.22
APPRD.	V.T.		04.03.22

If any queries contact : design@nihva.com

ALL DIMENSION ARE IN mm

NIHVA
NIHVA TECHNOLOGIES PVT. LTD.
NIHVA TECHNOLOGIES PVT. LTD. PUNE
Tel : 020 66304033
Email:- info@nihva.com
Website:- www.nihva.com

CLIENT - SRF
LOCATION - PITHAMPUR
PRODUCT - MOTORIZED SLIDING GATE
NIHVA\21-22\MFG\029 | REV- 01
SCALE: NTS | SHEET: 01 OF 01