



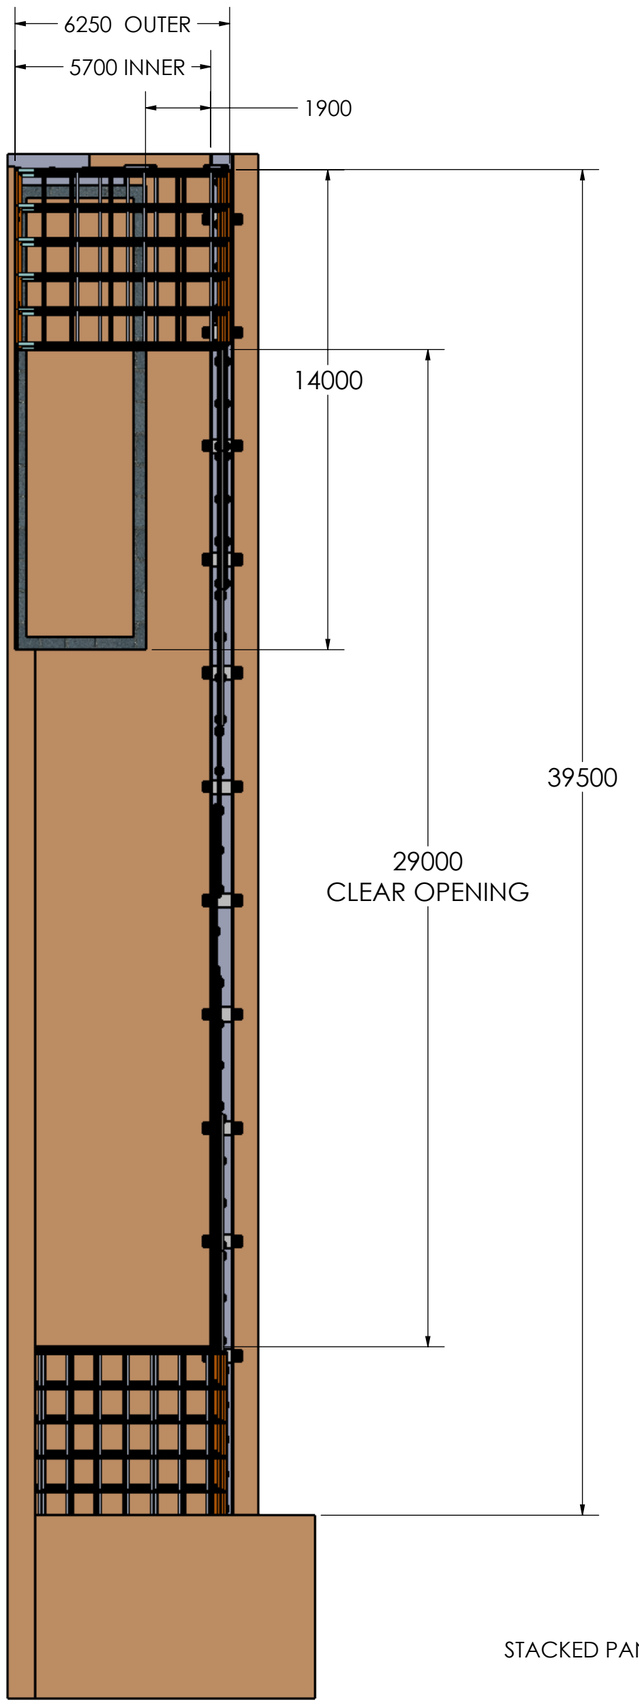


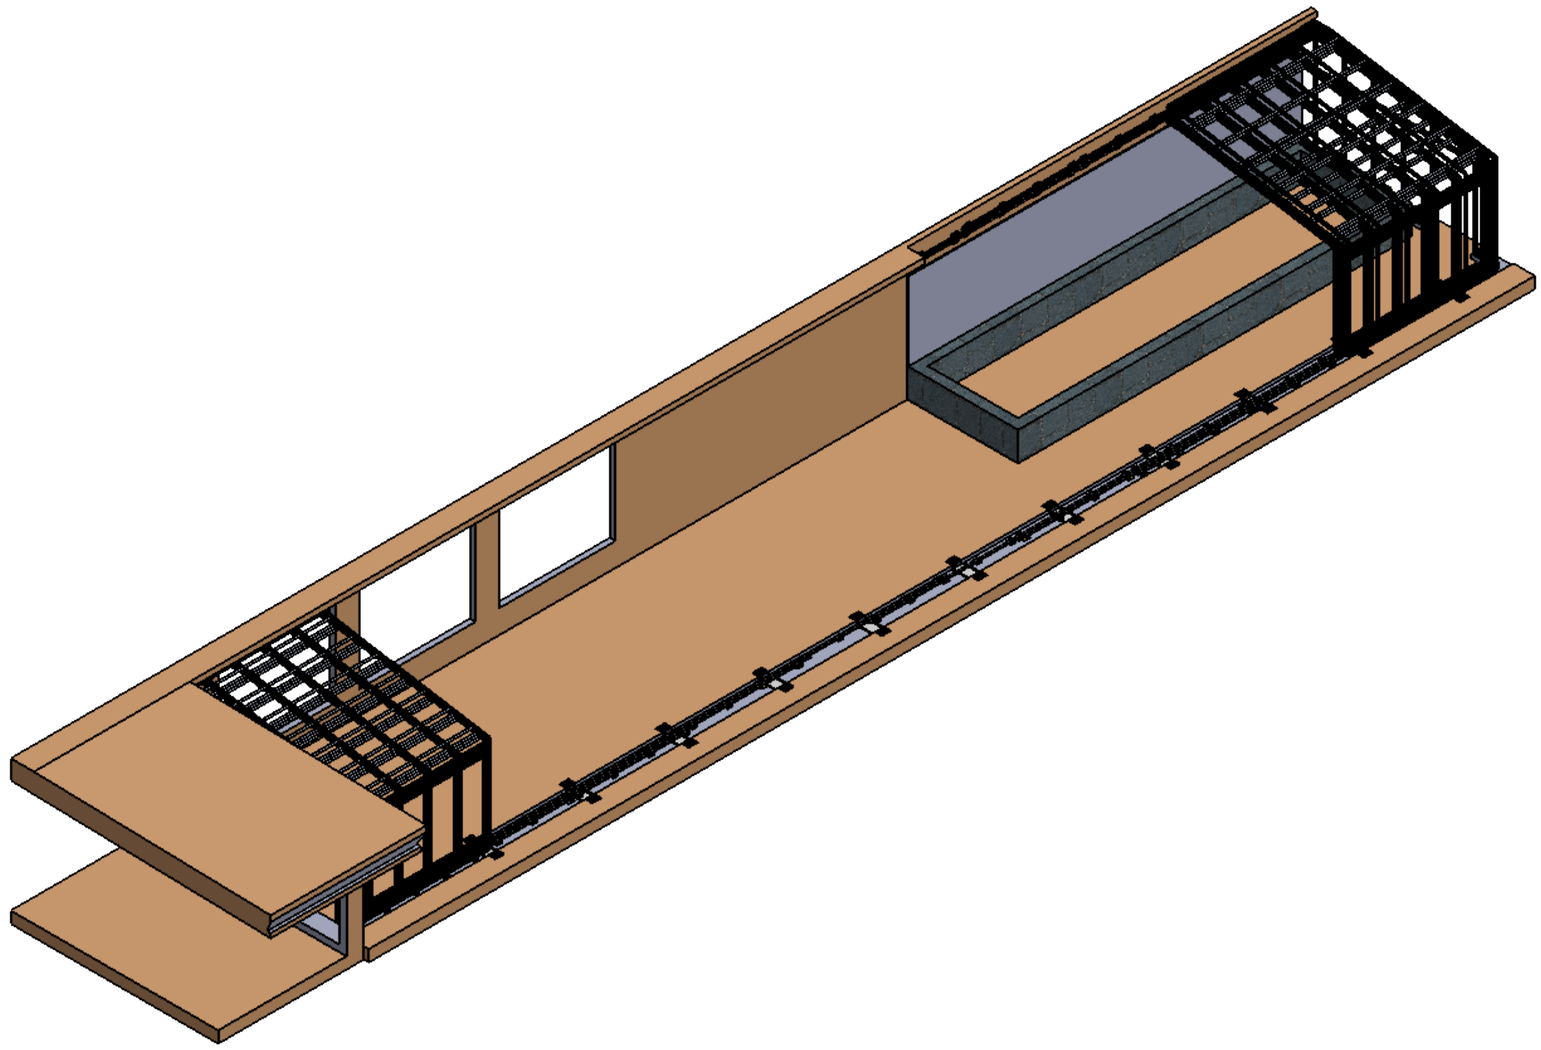

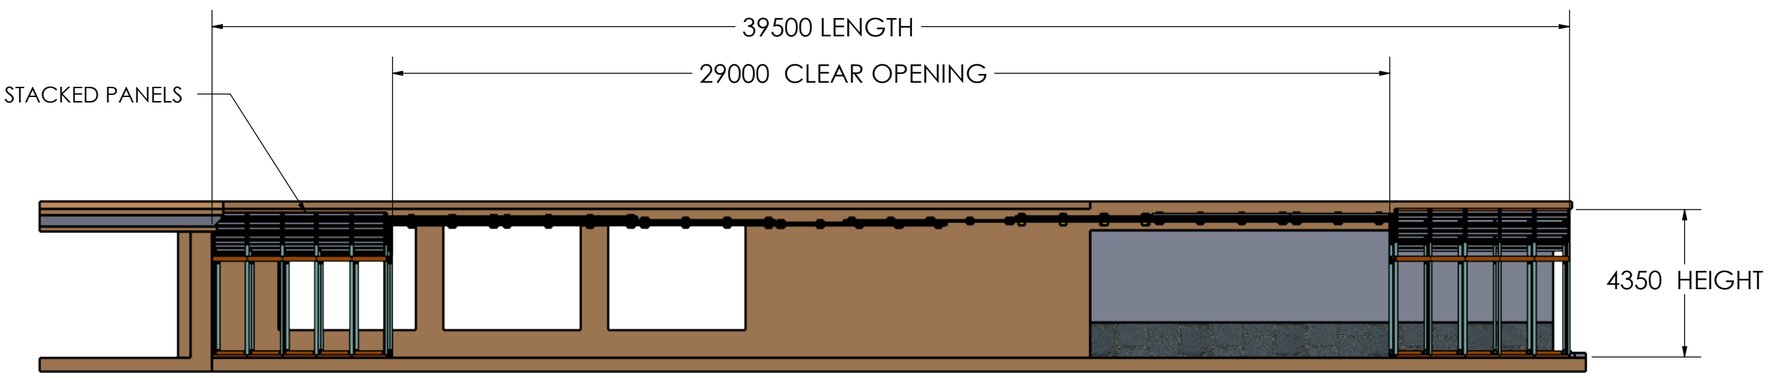

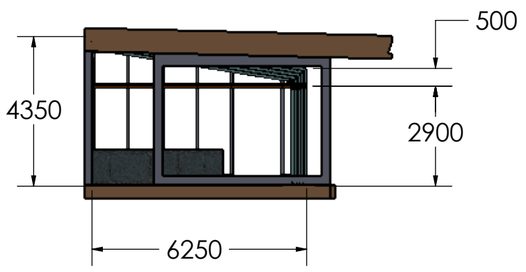

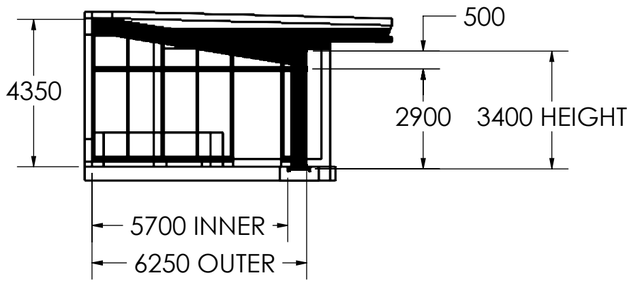

TITLE - STACKED PLAN				NIHVA TECHNOLOGIES PVT.LTD.PUNE
DWG NO - NTPL160 - ROOF			PANEL QTY - 8	Website - www.nihva.com
	NAME	SIGNATURE	DATE	PROJECT NO - NTPL160
DRAWN	D.V.		10.06.2023	PRODUCT - RETRACTABLE ROOF
CHK'D	P.M.		10.06.2023	SITE LOCATION -
APPV'D	V.T.		10.06.2023	
if any queries contact - supportautomation@nihva.com				REVISION -
ALL DIMENSION ARE IN mm		Custom		SCALE - SHEET 2 OF 2