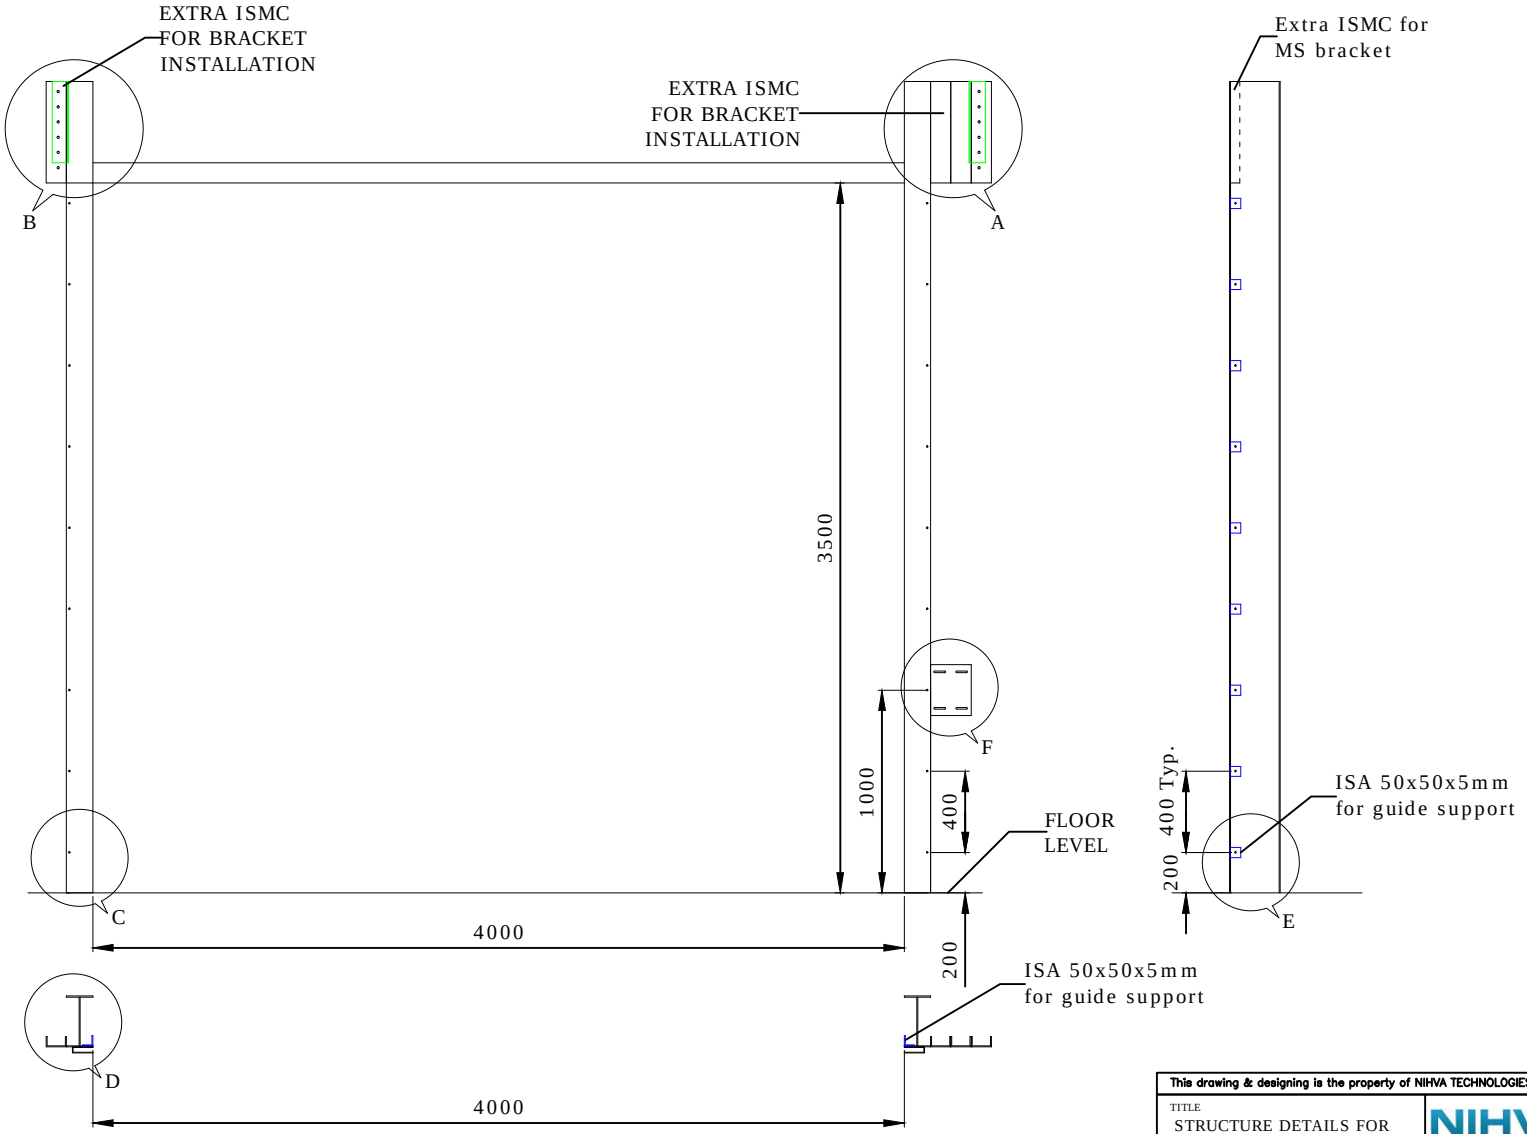

CLEAR WIDTH (CW)	CLEAR HEIGHT (CH)	QUANTITY
4000	3500	5

REV NO	DATE	DESCRIPTION
REV 0	03-01-2018	INITIAL DRAWING

This drawing & designing is the property of NIHVA TECHNOLOGIES. Not to be sold or copied to any other concern.

TITLE
STRUCTURE DETAILS FOR ROLLING SHUTTER (4x3.5m)

	SIGN	DATE
DRAWN	OMKAR	03/01/18
CHECK	SHEKHAR	03/01/18
APPROVAL	SHEKHAR	03/01/18
MFG.		

If any queries contact : design@nihva.com

ALL DIMENSION ARE IN mm

NIHVA
NIHVA TECHNOLOGIES PVT. LTD.
NIHVA TECHNOLOGIES PVT. LTD. PUNE
Tel : 020 66304033
Email:- info@nihva.com
Website:- www.nihva.com

CLIENT - MITTAL PRECISION HITECH STEEL PVT.LTD

PROJECT -

SITE - CHAKAN,PUNE

DWG. NO. : NIHVA/17-18/0324 | REV-0

SCALE: NTS | WT: | SHEET: 01 OF 01