
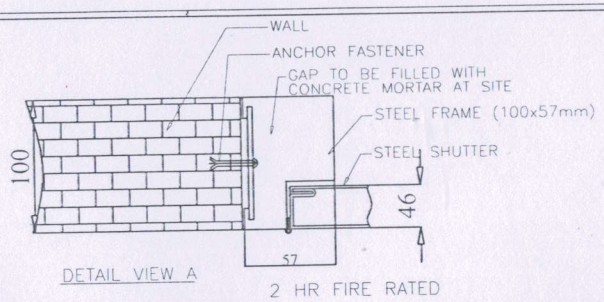


DETAIL VIEW A

2 HR FIRE RATED

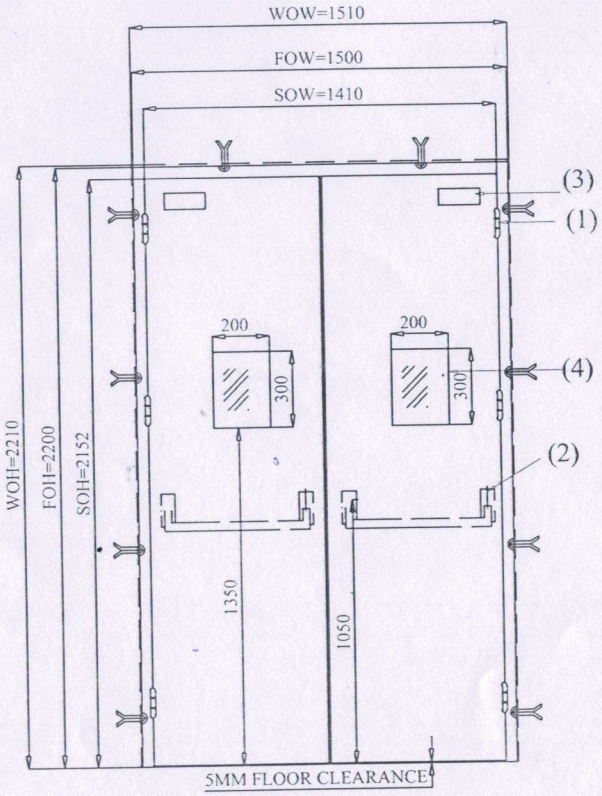

5MM FLOOR CLEARANCE

NOTES:-

ALL DIMENSIONS ARE IN MM.

A. ABBREVIATION

Wall Opening Width : WOW
Wall Opening Height : WOH
Frame Opening Height : FOH
Frame Opening Width : FOW
Shutter Opening Height : SOH
Shutter Opening Width : SOW

MATERIAL OF CONSTRUCTION
2HRS FIRE RATED
REF STD: IS 3614 PART-2: BS: 476

FRAME : G.I. 1.60mm Sheet
SHUTTER : G.I. 1.20mm Sheet

DOOR THICKNESS : 46mm

FRAME PROFILE : 100 x 57mm (Single Ribet)

INFILL MATERIAL : Rock Wool

PAINT: One Side Red Colour – One Side White

SCHEDULE OF HARDWARE

1) S.S. Ball Bearing Hinges (Yale Make) - 6 Nos.
2) Panic Bar for Double Leaf Door (Yale Make) - 1 Nos.
3) Heavy Duty Door Closer - 2 Nos.
4) Vision Panel with Fire Rated Glass of Size : 200 x 300mm (6mm Thick Fire Glass) - 2 Nos.

NIHVA TECHNOLOGIES PVT. LTD. * PUNE * NIHVA TECHNOLOGIES PVT. LTD.
Approved

24/11/2020

This drawing & design is the property of NIHVA TECHNOLOGIES. Not to be sold or copied to any other concern.

TITLE	1500mm (W) x 2200mm (H) Double Leaf Fire Door		
	NAME	SIGN	DATE
DRAWN	S.M.S.		24.11.2020
CHECK			
APPRD.			
If any queries contact : projectsupport@nihva.com			
ALL DIMENSION ARE IN mm			

NIHVA
NIHVA TECHNOLOGIES PVT. LTD.

NIHVA TECHNOLOGIES PVT. LTD. PUNE
Tel : 020 66304033
Email:- info@nihva.com
Website:- www.nihva.com

CLIENT -
PROJECT -
SITE LOCATION -
DWG. NO. : NIHVA/20-21/VDR/0079 REV- R00
SCALE: NTS WT: SHEET: