


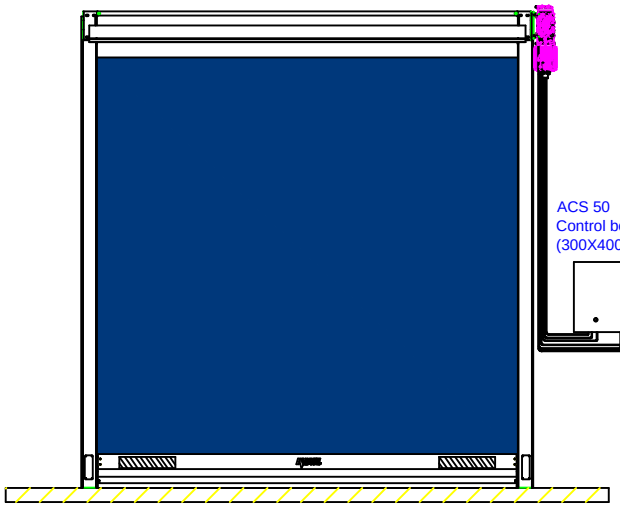


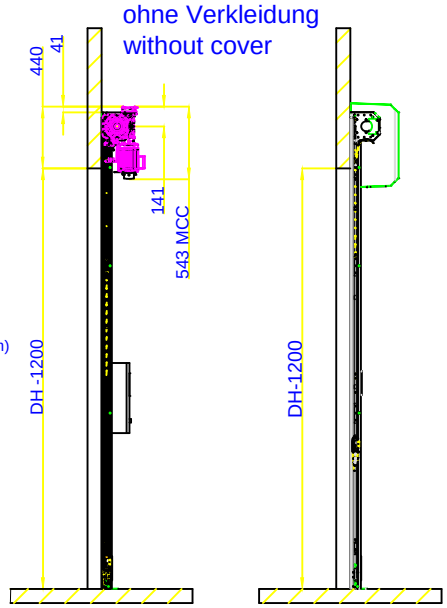


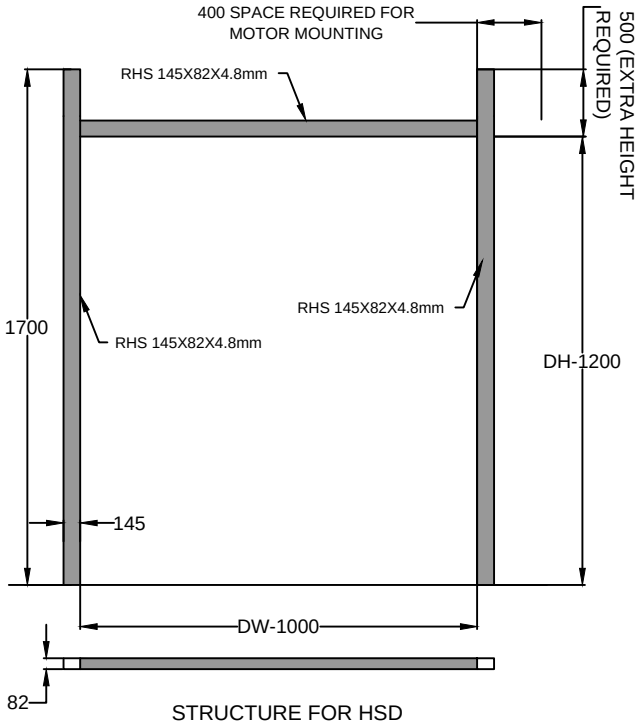

STRUCTURE FOR HSD

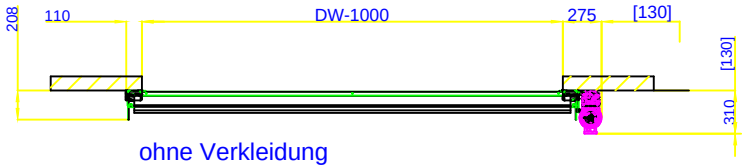

ohne Verkleidung
without cover

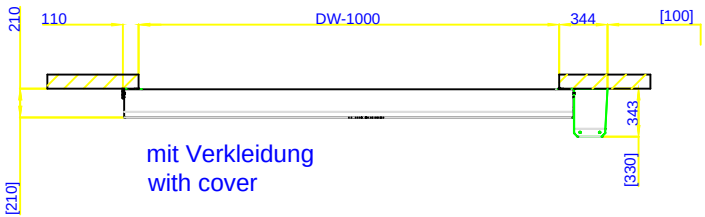

mit Verkleidung
with cover

COLORS -
1. BLUE (RAL 5002)
2. ORANGE (RAL 2009)
3. GREY (RAL 7001)

CURTAIN TYPE:-ROLLTEX

Tolerance ±3 mm (for all dimensions)

Dimensions in [ ] ==> clearance for installation

CLEAR WIDTH(DW)	CLEAR HEIGHT(DH)	MOTOR MOUNTING	QUANTITY
1000mm	1200mm	RIGHT SIDE	04 NOS

NOTE -
1.STRUTURE REQUIRED FOR HSD IS IN CLIENT'S SCOPE.
2.CLIENT HAS TO CONFIRM MOTOR POSITION(RIGHT/LEFT SIDE) AS PER SITE CONDITIONS.
3.CLIENT HAS TO CONFIRM COLOR OF CURTAIN.

This drawing & design is the property of NIHVA TECHNOLOGIES. Not to be sold or copied to any other concern.

TITLE	HIGH SPEED DOOR RP300 & STRUCTURE		
	NAME	SIGN	DATE
DRAWN	OMKAR		16/03/18
CHECK	PRADEEP		16/03/18
APP'V'ED	PRADEEP		16/03/18
If any queries contact : design@nihva.com			
ALL DIMENSION ARE IN mm			

NIHVA TECHNOLOGIES PVT. LTD. PUNE
Tel : 020 66304033
Email:- info@nihva.com
Website:- www.nihva.com

CLIENT :- KIRPEKAR ENGINEERING PVT. LTD.
PROJECT :-
LOCATION :- HINJEWADI PHASE-2
DWG. NO. :- NIHVA/17-18/0398 REV.:- 0
SCALE: NTS WT: SHEET: 01 OF 01