
Gate Opening Position

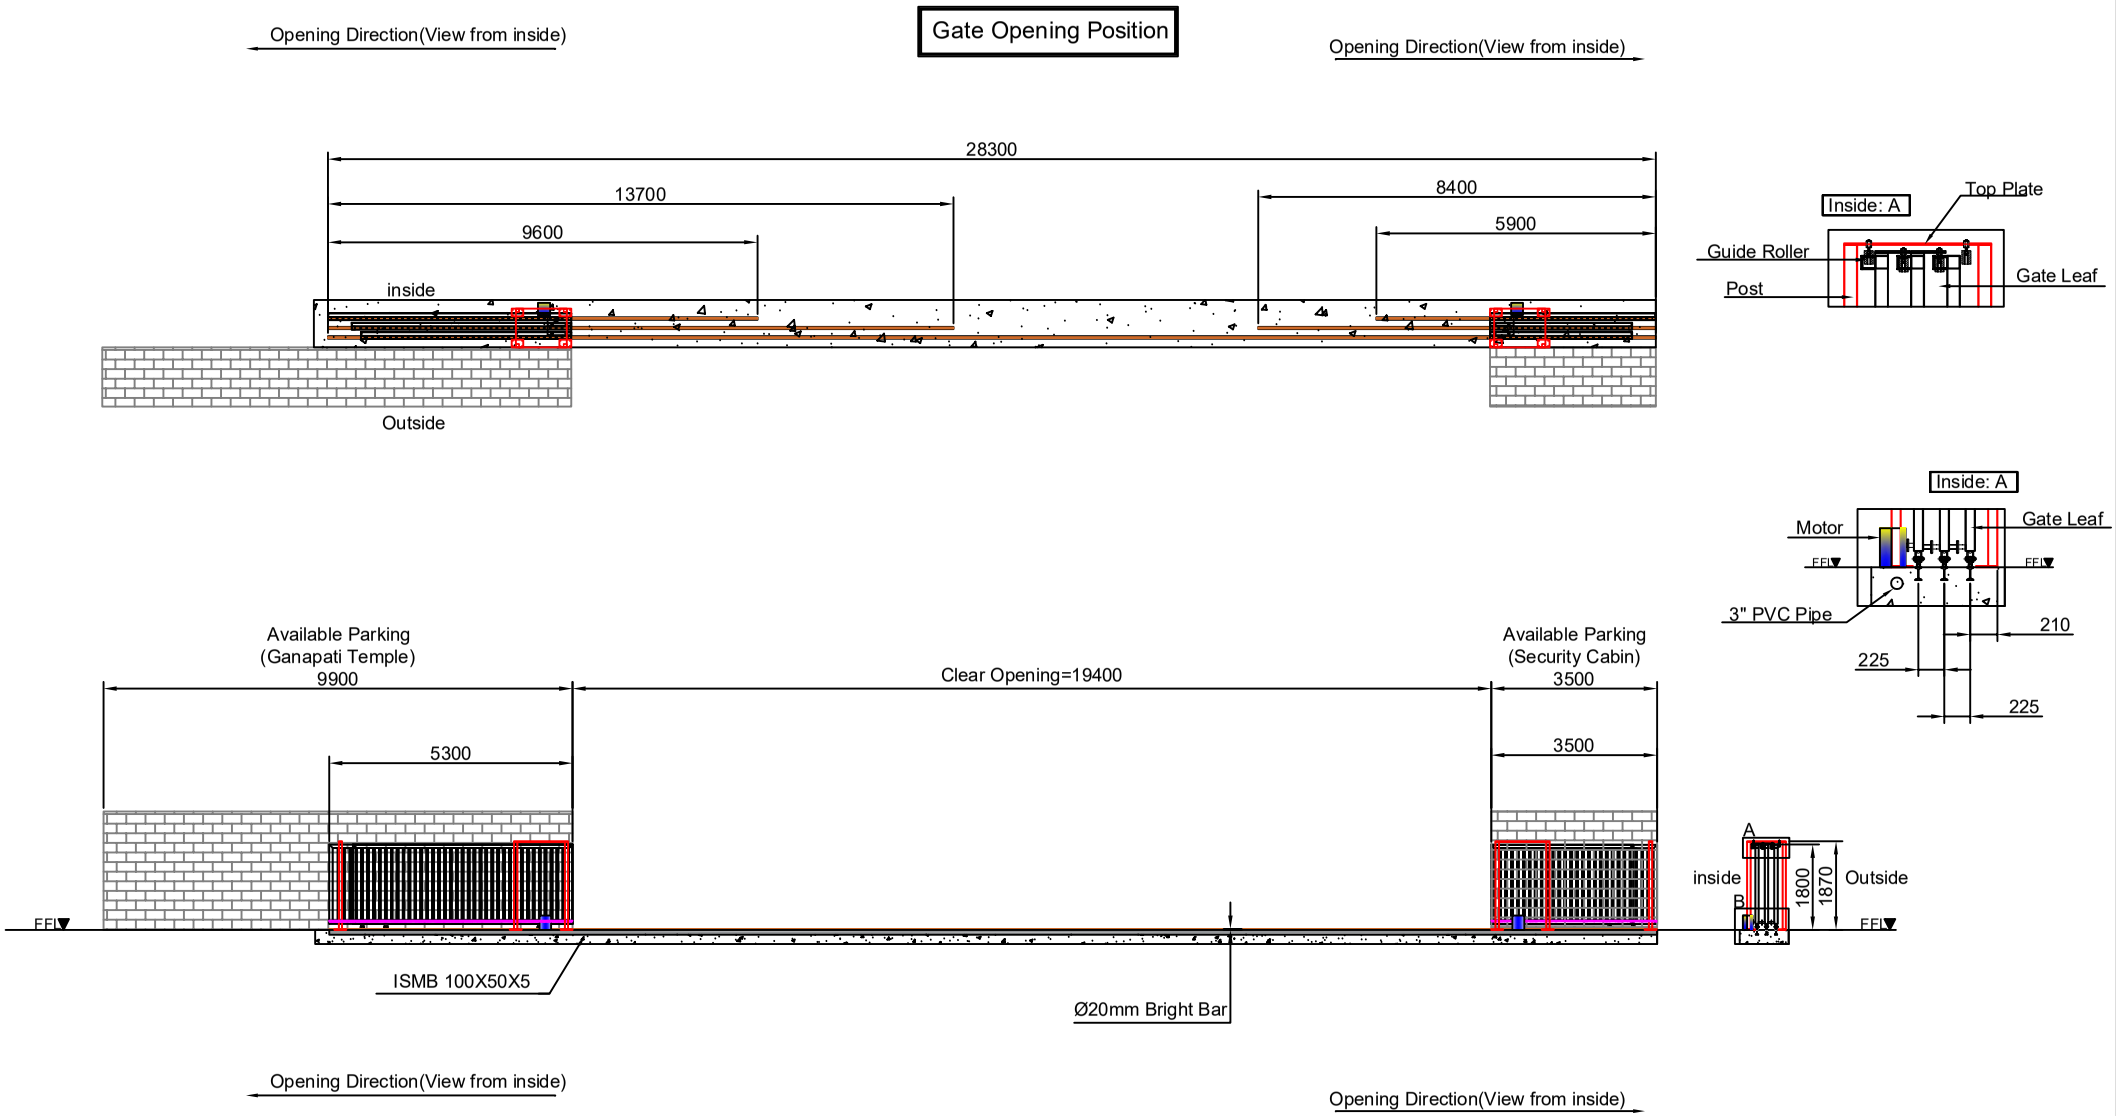

Note:-

1.All Dimension are in MM

2.Required All civil work will be in Client scope

3.Installlation and Fabrication tolerance will be ±20mm

4. Required Parking will be 5400mm and 3500mm

5. Gate Color will be Metalic color,shade stone gray(RAL7030)

This drawing & design is the property of NIHVA TECHNOLOGIES. Not to be sold or copied to any other concern.

TITLE:-
Bi-Parting Tel.Sliding Gate

	NAME	DATE	SIGN
DRAWN	SUJATA.B	30/07/2022	
CHECK	MAHESH.S	30/07/2022	
APPRD.	AMIT.K	30/07/2022	

If any queries contact : design@nihva.com

ALL DIMENSION ARE IN mm

NIHVA
NIHVA TECHNOLOGIES PVT. LTD.
NIHVA TECHNOLOGIES PVT. LTD. PUNE
Tel : 020 66304033
Email:- info@nihva.com
Website:- www.nihva.com

CLIENT - NAVNEET EDUCATION LTD

LOCATION - PALGHAR

PRODUCT - TEL.SLIDING GATE | QTY-01

DWG NO:- NIHVA/22-23/CLT/0071_7 | REV-01

SCALE: NTS | SCALE:-- 1:1 | SHEET: 01 OF 01

Rev No.	Revision	Date	Revised By
01	As per New Opning	30/07/2022	Sujata