



ELEVATION

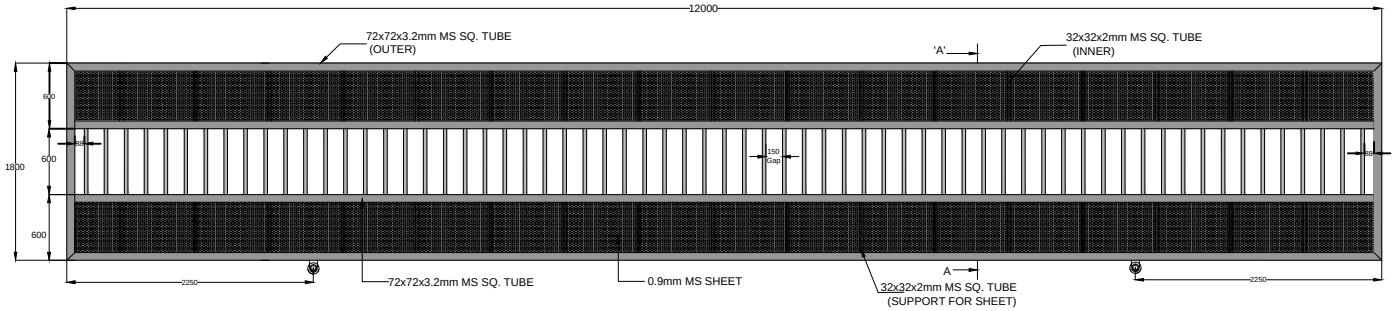

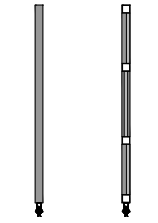

PLAN

SR NO	TUBE SPECIFICATION		MATERIAL	SIZE
1	72X72X3.2mm MS TUBE	OUTER FRAME	MILD STEEL	14.5 MTR- 04 NOS 1.8 MTR - 02 NOS
2	32X32X2mm MS TUBE	INNER PATTERN	MILD STEEL	0.600MTR- 65NOS 0.456MTR- 35NOS
3	150mm	GAP BETWEEN TUBES	-	-
4	0.9mm THK	MS SHEET	MILD STEEL	1482X456X0.9-16NOS

COLOUR CODE - RAL9002 GREY WHITE

TOLERANCE:- ± 10mm

CLEAR WIDTH (CW)	CLEAR HEIGHT (CH)	QUANTITY
12000mm	1800mm	1 NO

DIMENSION :

CLEAR WIDTH	CLEAR HEIGHT	QUANTITY
12000mm	1800mm	1 NO

MATERIAL: MS

THICKNESS :

NOTE-
1. ALL REQUIRED CIVIL WORK WILL BE IN CLIENTS SCOPE.
2.ONE COAT OF RED OXIDE & TWO COAT OF APPROVED RAL SHADE WILL BE GIVEN TO THE GATE.
3.GATE WILL CUT IN 3 PART FOR TRANSPORT.

NIHVA TECHNOLOGIES PVT. LTD.
NIHVA TECHNOLOGIES PVT. LTD, PUNE
Email:- info@nihva.com
TEL :020 66304033
Website:- www.nihva.com

TITLE:

SLIDING GATE LEAF

CLIENT'S APPROVAL :

CLIENT -

PROJECT -

SITE LOCATION - WEST BENGAL.

DWG. NO. : NIHVA/18-19/VDR/244

SCALE: NTS	WT:	SHEET:1 OF 1

	NAME	SIGN	DATE
DRAWN	SURAJ		04-12-2018
CHECK	PRADEEP		04-12-2018
APPROVED	R.D		04-12-2018

IF ANY QUERIES CONTACT:- design@nihva.com

NOTE: ALL DIMENSIONS ARE IN mm

THIS DRAWING & DESIGN IS THE PROPERTY OF NIHVA TECHNOLOGIES. NOT TO BE SOLD OR COPIED TO ANY OTHER CONCERN.