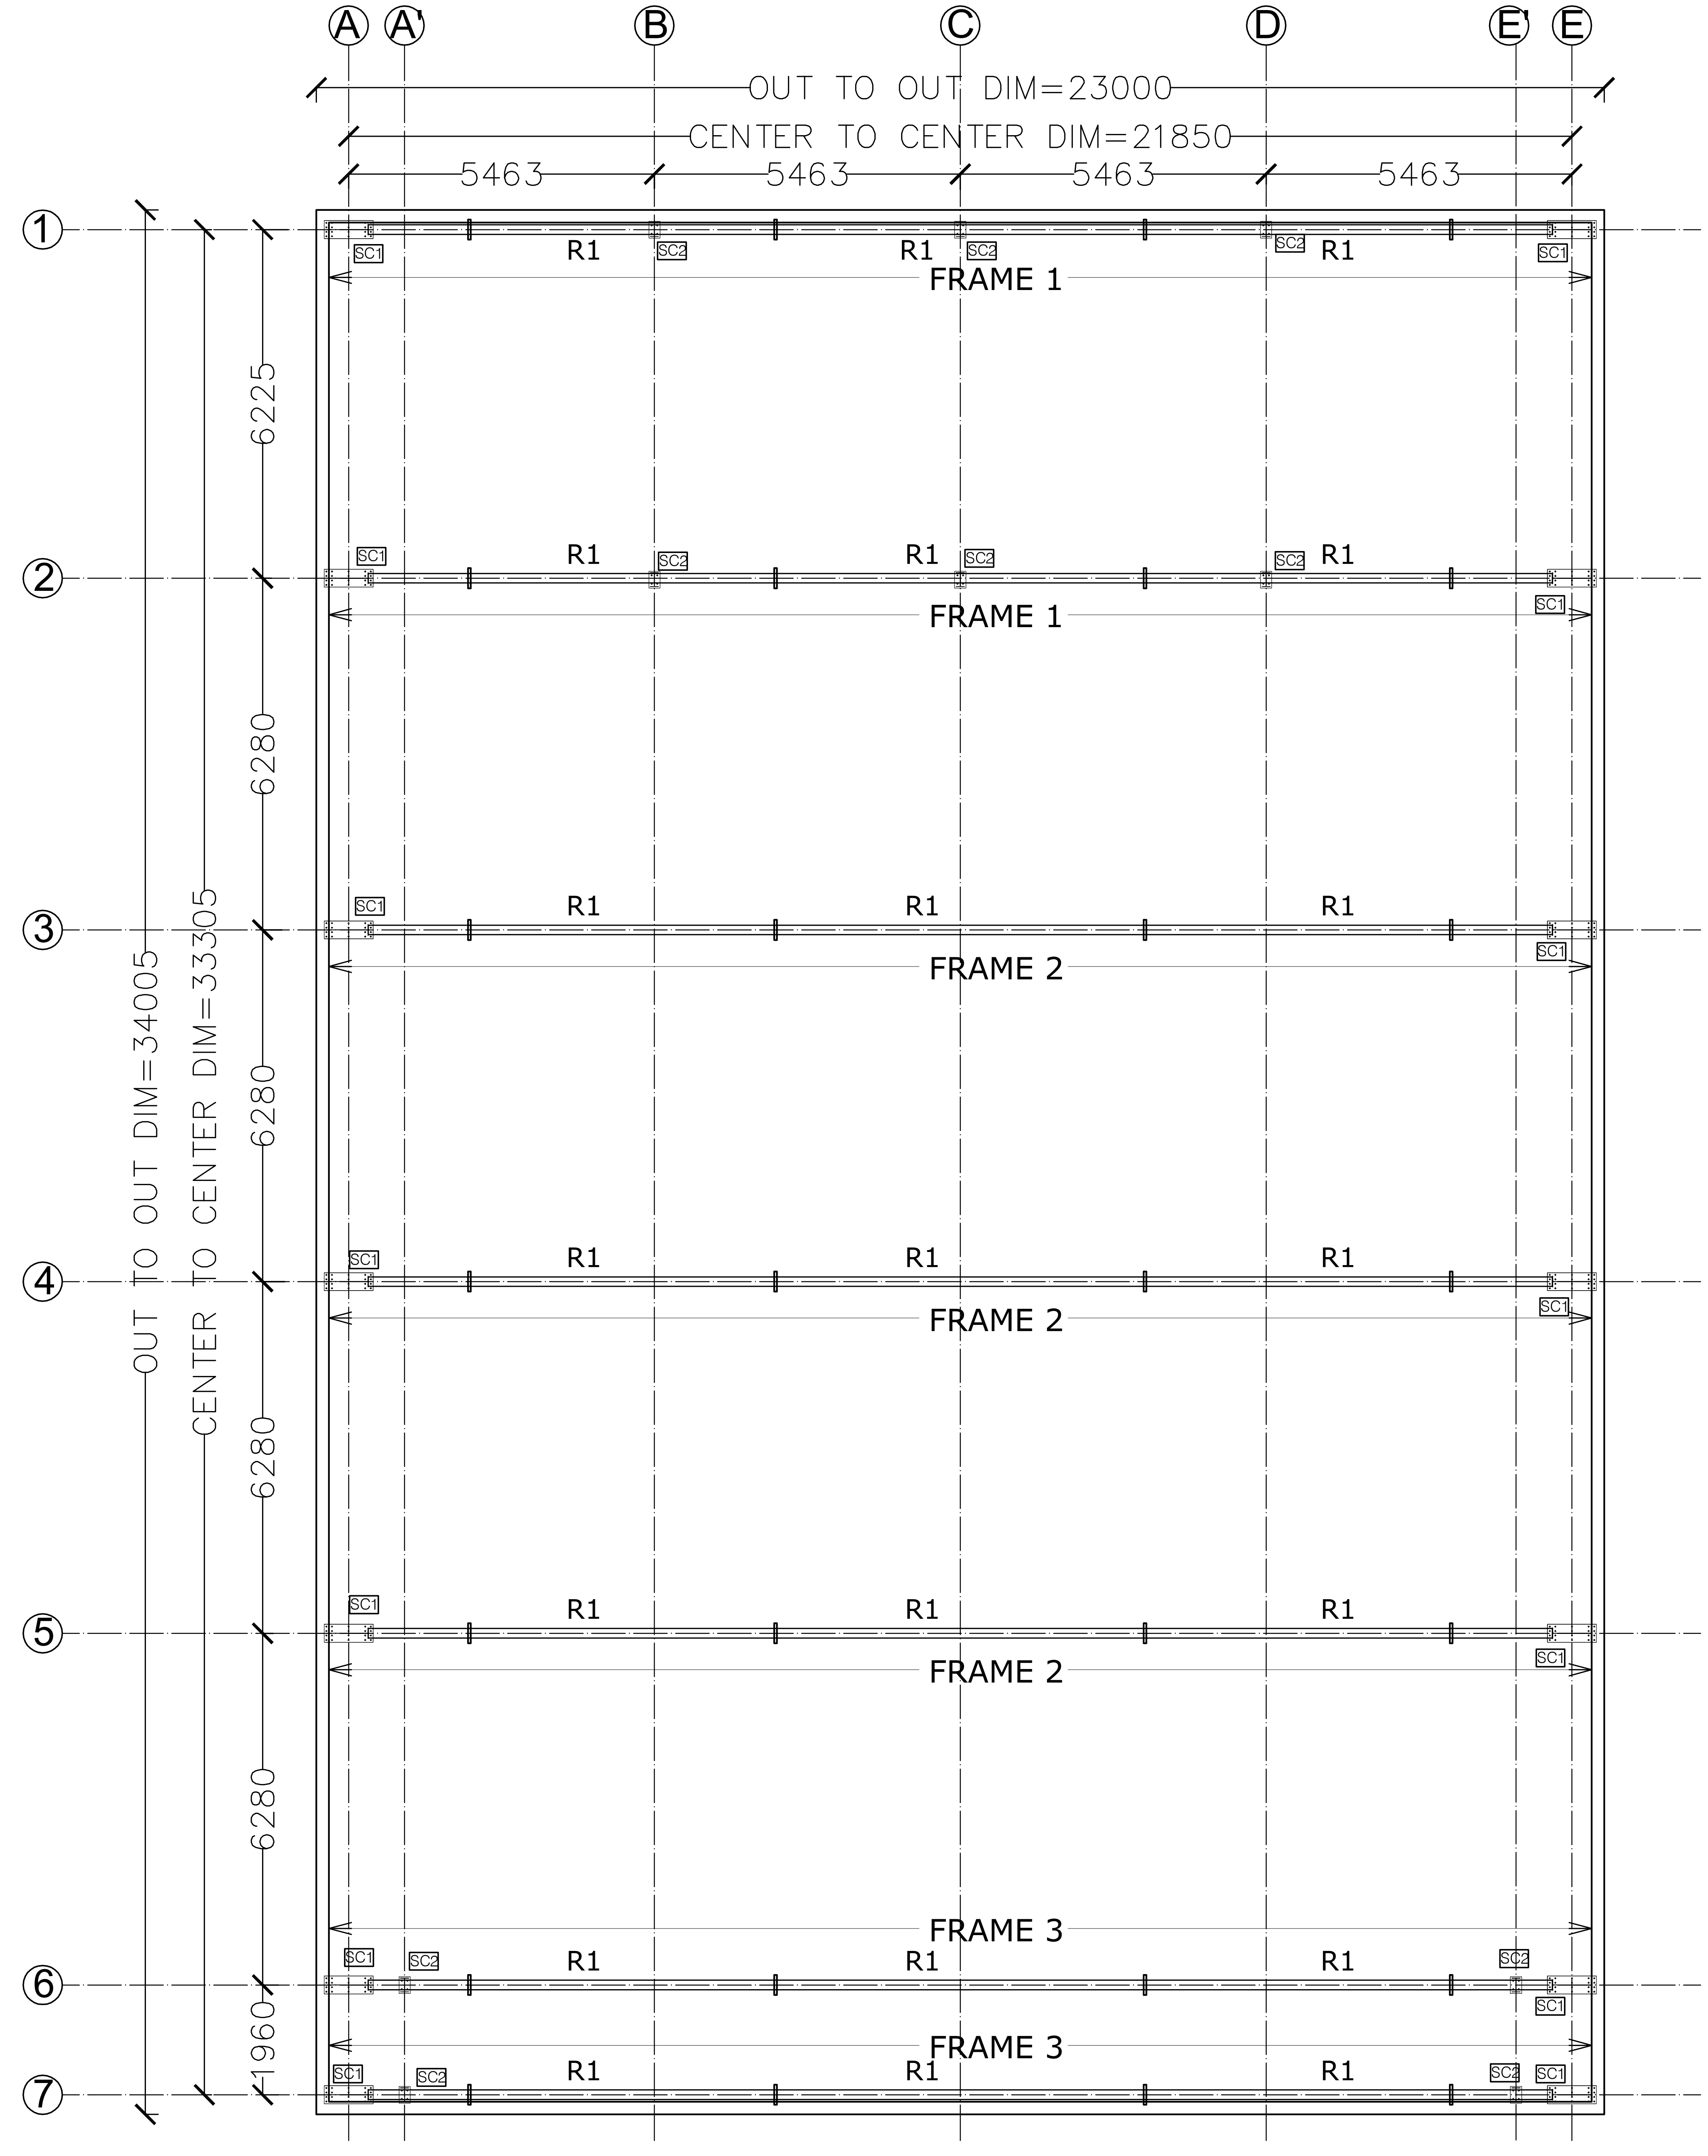
A
A'
B
C
D
E'
E
OUT TO OUT DIM=23000
CENTER TO CENTER DIM=21850
5463
5463
5463
5463
1
2
3
4
5
6
7
OUT TO OUT DIM=34005
CENTER TO CENTER DIM=33305
6225
6280
6280
6280
6280
1960
R1
SC1
SC2
FRAME 1
FRAME 1
FRAME 2
FRAME 2
FRAME 2
FRAME 3
FRAME 3

INDEX PLAN

KEY PLAN :-

LEGEND :-

⬚	REINFORCED CONCRETE
▨	230MM THK BRICK WALL
■	STRUCTURAL GLAZING

N

GENERAL NOTES :

ALL DIMENSIONS ARE IN MILLIMETRES AND ARE UNFINISHED DIMENSIONS UNLESS OTHERWISE SPECIFIED.

ALL LEVELS ARE IN METRES AND ARE UNFINISHED LEVELS UNLESS OTHERWISE SPECIFIED.

DO NOT SCALE DRAWINGS. ONLY WRITTEN DIMENSIONS SHALL BE FOLLOWED, ANY DISCREPANCIES NOTED SHALL BE BROUGHT TO THE NOTICE OF THE ARCHITECT PRIOR TO EXECUTION.

SCHEDULE OF JOINERY

TYPE	DESCRIPTION	SIZE	NO.
RS	HANGER DOOR	24000 x 9000	01
W	WINDOW	1500 x 1200	20
D	DOOR	1200 x 2200	0

STRUCTURAL NOTES :

- * ANCHOR BOLTS OF GRADE 4.6
- * CONCRETE GRADE M30
- * REBAR GRADE Fe 415

R1	ISSUED FOR APPROVAL	20-07-17	CMF	SSF
R0	ISSUED FOR APPROVAL	20-07-17	CMF	SSF
REV.	DESCRIPTION	DATE	BY	CHD.

AMENDMENT

GRAPHIC SCALE: 0.5M 0 0.5M 1M 2M 3M 4M 5M

ARCHITECT

CLIENT:

HANGER
AT PUNE

PROJECT LOCATION:

PUNE

DRAWING TITLE:

GENERAL ARRANGEMENT DRAWINGS

SCALE : NTS
DRAWN : SRK
DATE : 02-08-2018
CHKD : SRK

R0

PROJECT ID:
1718-AI-052-PEB

DRAWING NO:
PD: 01

Astre Infra
Private Limited
imagine and its done

691, Bemciel Indl. Estate,
Khanapur Rd,
Udyambag, Belgaum- 590008.
www.astreinfra.com

THESE DRAWINGS ARE UNDER COPYRIGHT AND ARE THE PROPERTY OF ASTRE INFRA PVT. LTD.. NONE OF THE DRAWINGS AND RELATED DOCUMENTS CAN BE REPRODUCED, COPIED IN WHOLE OR IN PART WITHOUT PRIOR EXPRESSED WRITTEN CONSENT OF ASTRE INFRA PVT.LTD. THESE DRAWINGS CANNOT BE HANDED OVER TO A THIRD PARTY OR USED FOR ANY PURPOSE, OTHER THAN THAT FOR WHICH IT HAS BEEN LOANED. AFTER FULFILLING THE PURPOSE OF ISSUE THE DRAWINGS SHALL BE RETURNED TO ASTRE INFRA PVT.LTD.