


NOTE :
1. DOOR HINGES : GEZE MAKE.
2. DOOR CLOSER : GEZE MAKE.
3. DOOR EXTERNAL TRIM : YELE MAKE.

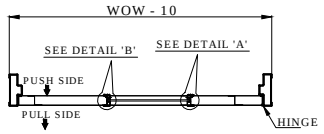

TOP VIEW

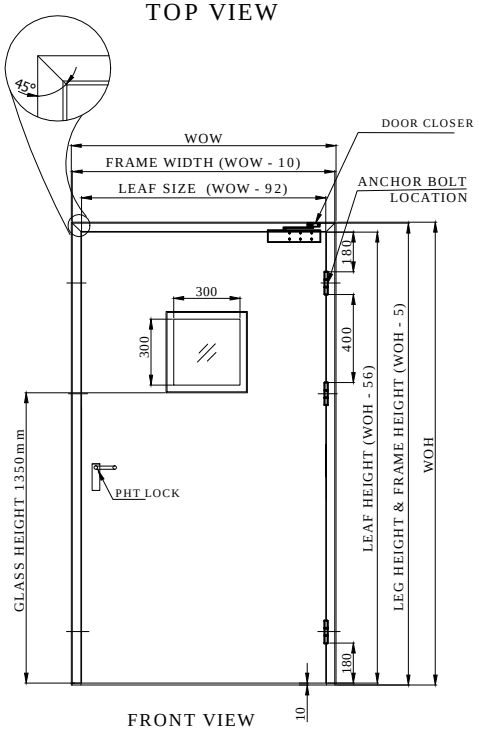


FRONT VIEW

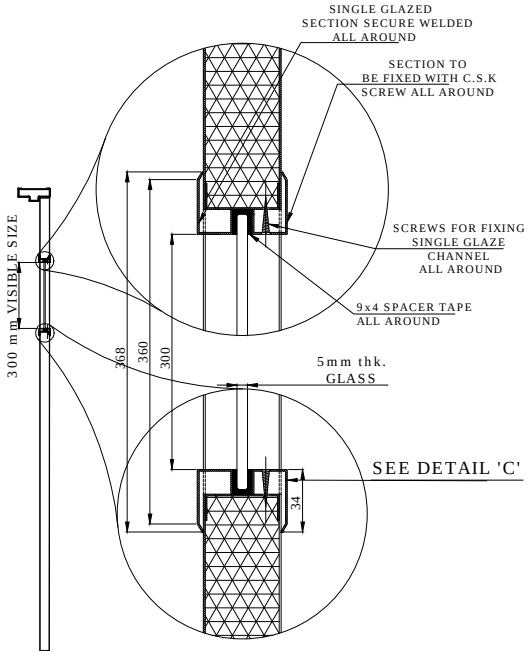


SIDE VIEW
SECTION A-A'

SINGLE GLAZE FIXING DETAIL

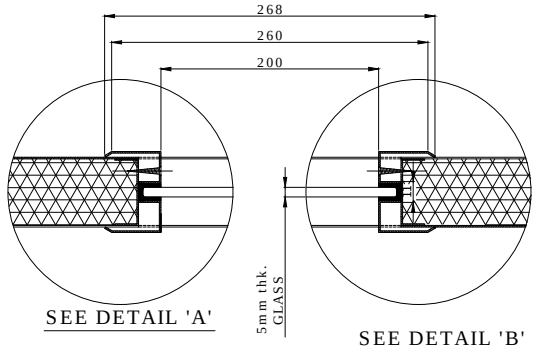



SEE DETAIL 'A'

SEE DETAIL 'B'

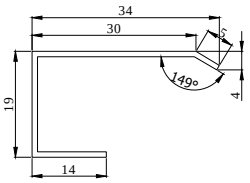


SEE DETAIL 'C'

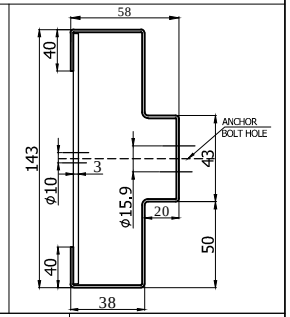

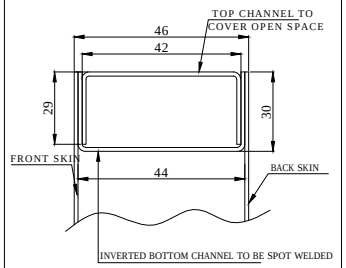

DOOR TOP SECTION DETAIL

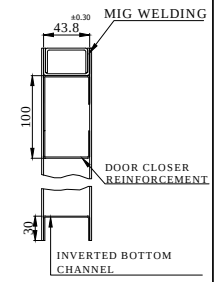

DOOR BOTTOM & TOP DETAIL

REV. NO	DATE	DRAWN	REMARK
R01	27.03.19	P.V.A	1.SPECIFICATION & QTY CHANGE.

SR. NO	WALL OPENING WIDTH	WALL OPENING HEIGHT	QTY	RAL	LOCATION	HARDWARE
02	900	2375	01	9002	Block G - Security cabin - white colour	Single leaf metal door with Vision Panel, Hinges , Door closer ,with external trim
01	900	2380	01	9002	Block G - Security cabin - white colour	Single leaf metal door with Vision Panel, Hinges , Door closer ,with external trim

TOLERANCE - ±05mm

This drawing & design is the property of NIHVA TECHNOLOGIES. Not to be sold or copied to any other concern.

TITLE: SINGLE LEAF STEEL DOOR

	NAME	SIGN	DATE
DRAWN	P.V.A		21.03.2019
CHECK	V.M.T		21.03.2019
APPRD.			

NIHVA TECHNOLOGIES PVT. LTD.
NIHVA TECHNOLOGIES PVT. LTD. PUNE
Tel : 020 66304033
Email:- info@nihva.com
Website:- www.nihva.com

If any queries contact : design@nihva.com

CLIENT -

PROJECT -

SITE LOCATION -

DWG. NO. : NIHVA/18-19/VDR/426/R01 | REV- R01

ALL DIMENSION ARE IN mm | SCALE: NTS | WT: | SHEET: 01 OF 01