




Client scope

* Drainage area or pipe need to be shift from right side
*Roof need to be shift at top 365mm
*Gutter need to be close till pipe

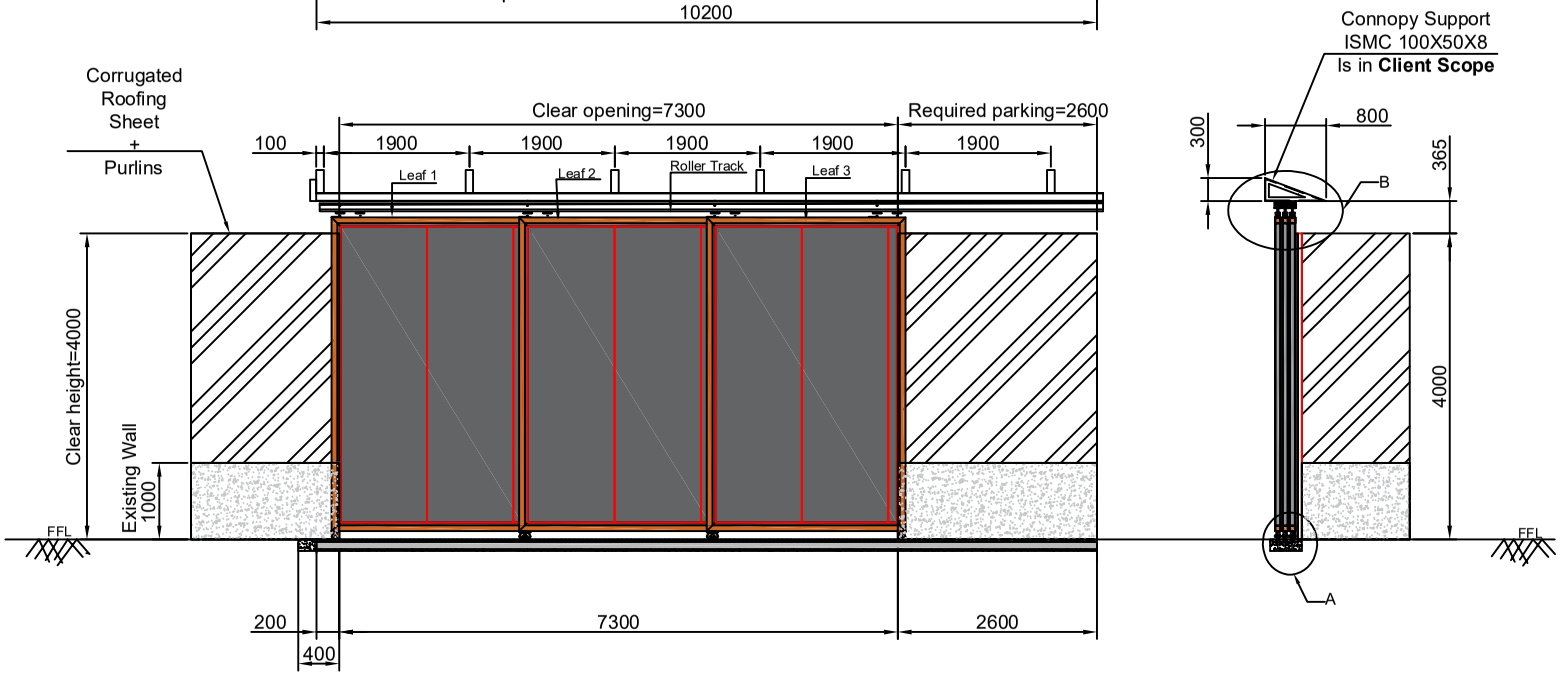


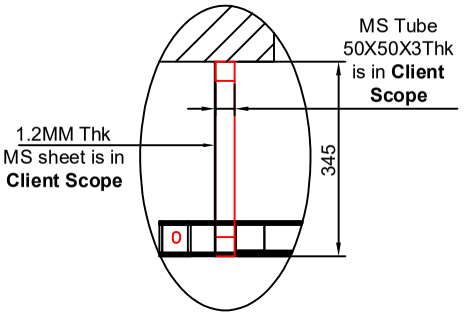

Detail C

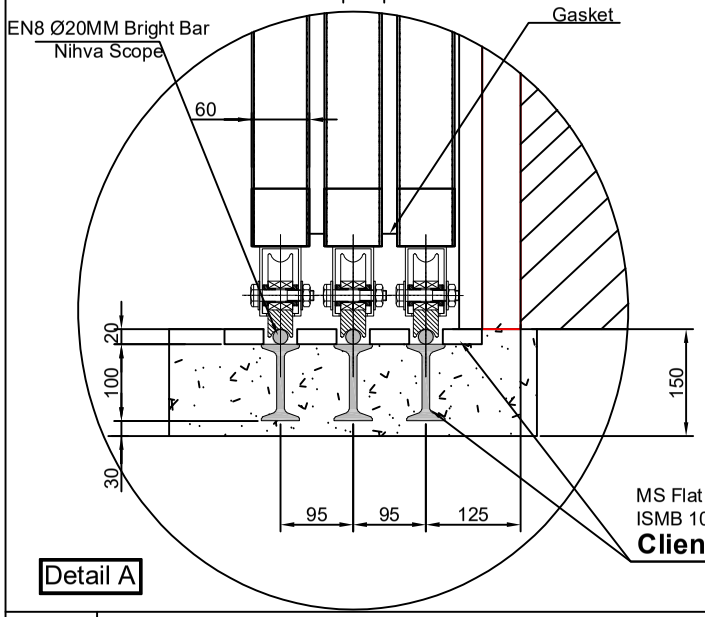

Detail A

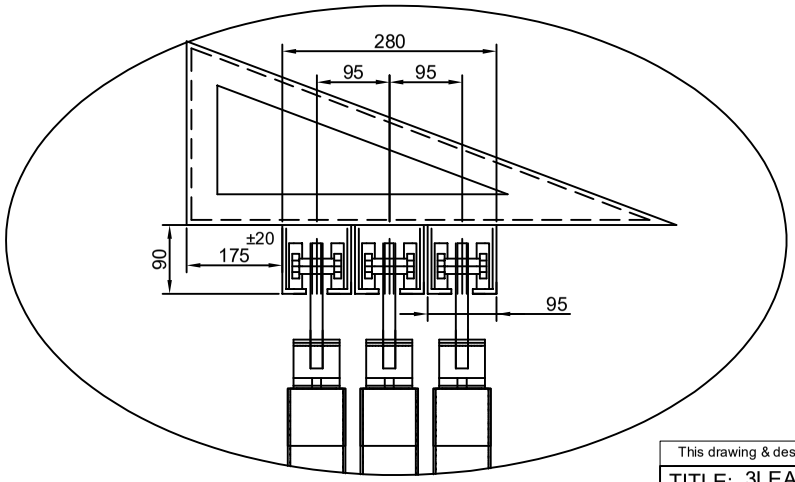

Detail B

Color code	Color
5018	Turquoise blue

Note:--

1. All dimension are in MM
2. All Civil work will be in client scope
3. For 7300mm opening we required exact 2600mm parking space if not there will be opening reduce by 100mm
4. Manufacturing,civil and installation tolerance will be ±10mm
5. Top and Bottom track should be in parallal within ±3mm
6. Nihva Supervisor on site for Monitoring/Checking of civil work

This drawing & design is the property of NIHVA TECHNOLOGIES. Not to be sold or copied to any other concern.

TITLE:- 3LEAF RIGHT SIDE CRM DOOR 03/Gate 11

NIHVA TECHNOLOGIES PVT. LTD.

NIHVA TECHNOLOGIES PVT. LTD. PUNE
Tel : 020 66304033
Email:- info@nihva.com
Website:- www.nihva.com

	NAME	DATE	SIGN
DRAWN	SUJATA	29/04/2022	
CHECK	M.SUTAR	29/04/2022	
APPRD.	V.TARAK	29/04/2022	

CLIENT - LESTECH
LOCATION - POSCO MANGAON
PRODUCT - SLIDING DOOR
If any queries contact : design@nihva.com
DWG NO:-NIHVA/22-23/CLT/0015 REV- 1
ALL DIMENSION ARE IN mm
SCALE: NTS SCALE:-- 1:1 SHEET: 01 OF 01

Rev No.	Revision	Date	Revised By
00	Released drawing	29/04/2022	Sujata
1.	Revised as per Client Comments	02/05/2022	Sujata