


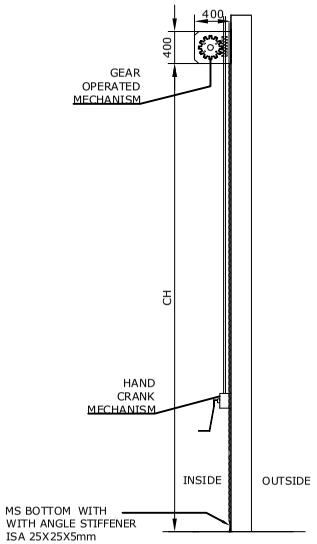



SIDE VIEW

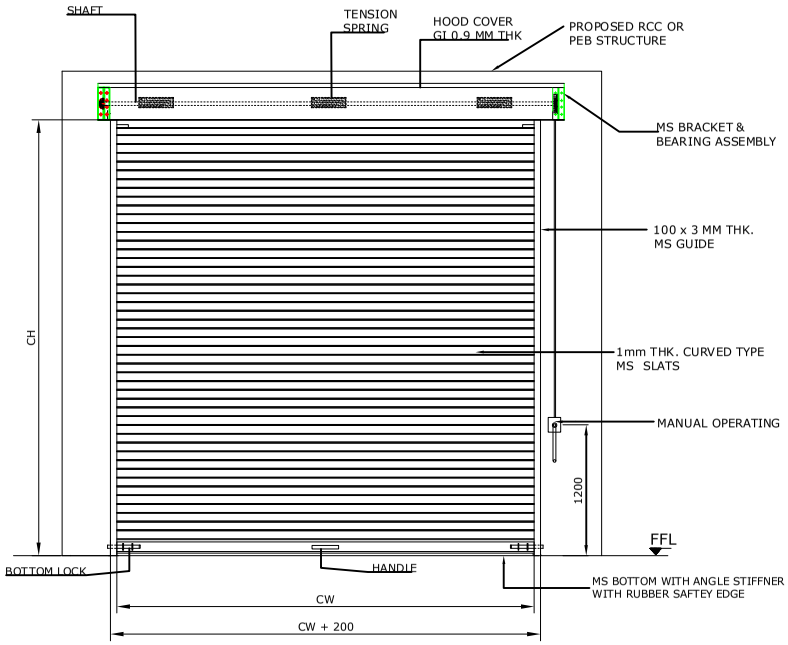

INSIDE ELEVATION

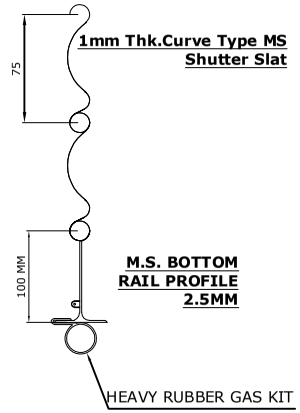

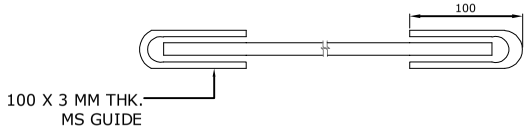

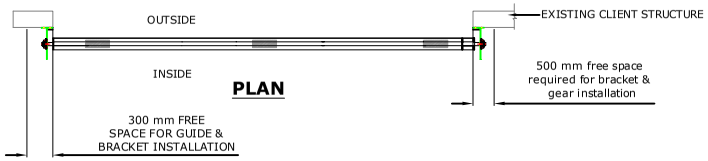

PLAN

NOTE-
1. All dimension are in MM.
2. Surface Finish: Powder coating of approved RAL CODE 9002
3.Mounting :On concrete column

TOLERANCE - ±10mm

SR NO	(CW) CLEAR WIDTH	(CH) CLEAR HEIGHT	QUANTITY
1	4500	3670	01 NO

This drawing & design is the property of NIHVA TECHNOLOGIES. Not to be sold or copied to any other concern.

TITLE			
GEAR OPERATED ROLLING SHUTTER			
	NAME	DATE	SIGN
DRAWN	Sujata	25.03.2022	
CHECK	G.I.P	25.03.2022	
APPRD.	P.J	25.03.2022	

NIHVA TECHNOLOGIES PVT. LTD.
NIHVA TECHNOLOGIES PVT. LTD. PUNE
Tel : 020 66304033
Website:- www.nihva.com
Email:- info@nihva.com

If any queries contact : design@nihva.com

CLIENT -

PROJECT -GEAR OPERATED ROLLING SHUTTER

SITE LOCATION -

DWG. NO. : NIHVA/21-22/VDR/060 | REV- R0

ALL DIMENSION ARE IN mm | SCALE: NTS | WT: | SHEET: 01 OF 01