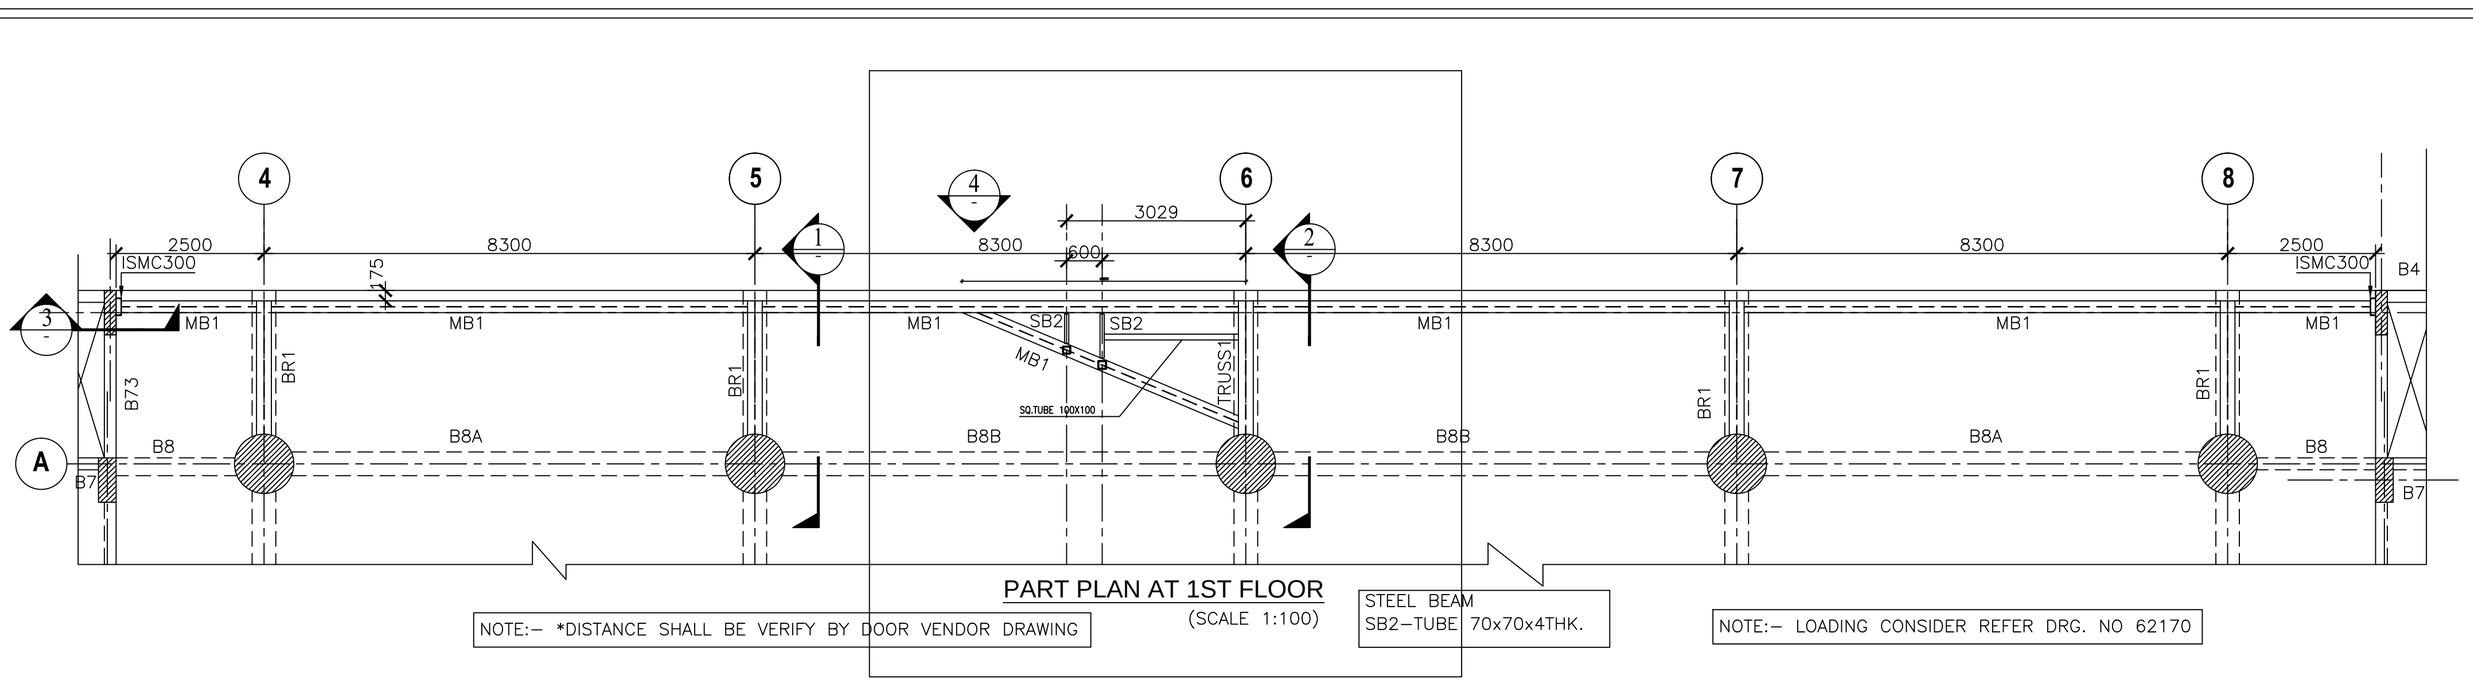



## PART PLAN AT 1ST FLOOR

(SCALE 1:100)

NOTE:– *DISTANCE SHALL BE VERIFY BY DOOR VENDOR DRAWING

STEEL BEAM
SB2–TUBE 70x70x4THK.

NOTE:– LOADING CONSIDER REFER DRG. NO 62170

This drawing & design is the property of NIHVA TECHNOLOGIES. Not to be sold or copied to any other concern.

TITLE
STRUCTURAL DESIGN

NIHVA TECHNOLOGIES PVT. LTD.
Website:– www.nihva.com
NIHVA TECHNOLOGIES PVT. LTD. PUNE
Tel : 020 66304033
Email:– info@nihva.com

| | NAME | SIGN | DATE |
|---|---|---|---|
| DRAWN | P.A | | 18.10.19 |
| CHECK | S.P | | 18.10.19 |
| APPRD. | | | |

CLIENT -
PROJECT -
SITE LOCATION -
If any queries contact : design@nihva.com
DWG. NO. -NIHVA/19-20/
ALL DIMENSION ARE IN mm
SCALE:NTS | WT: | SHEET:01 OF 01