


PRODUCED BY AN AUTODESK EDUCATIONAL PRODUCT

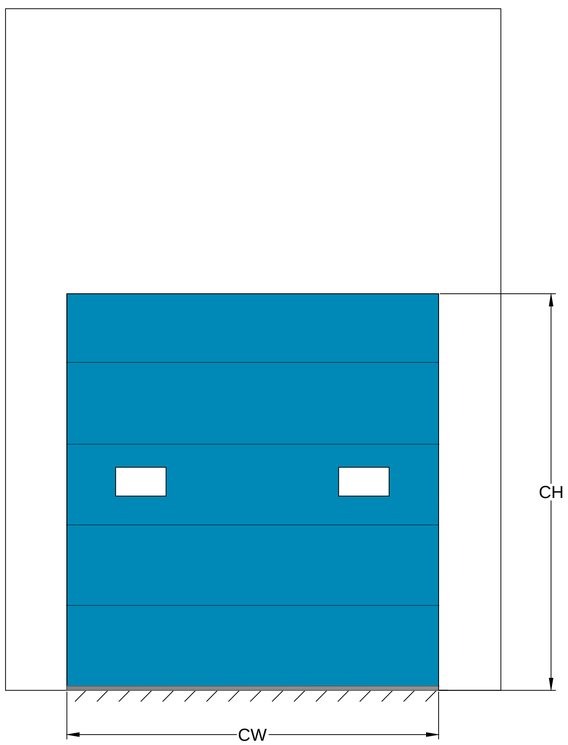


OUTSIDE ELEVATION

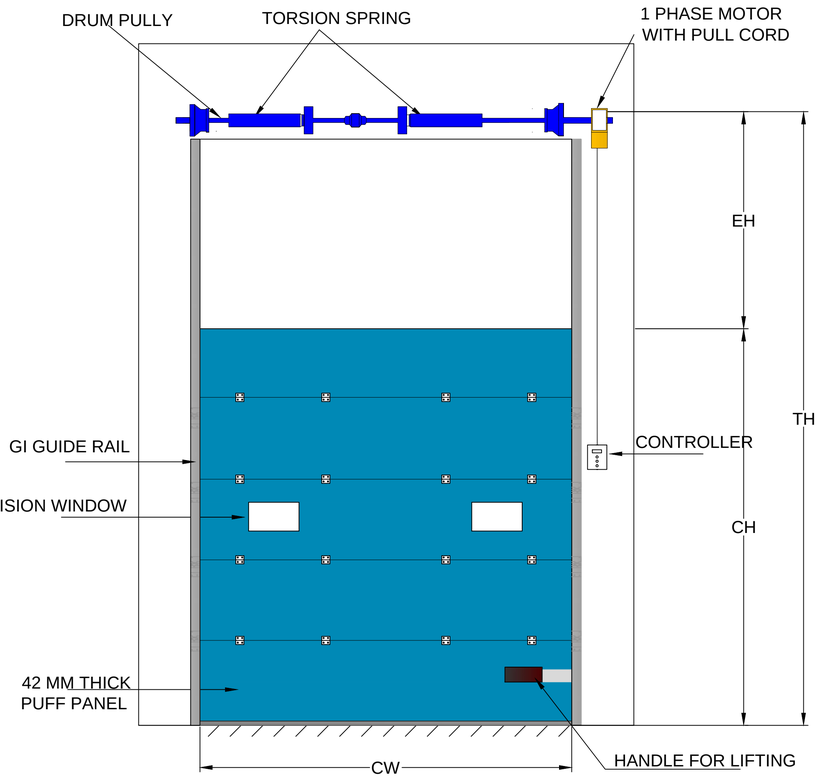


INSIDE ELEVATION

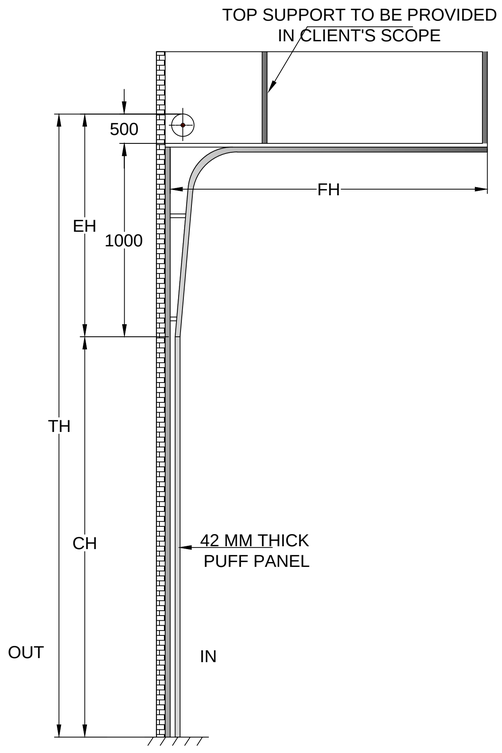

SIDE VIEW

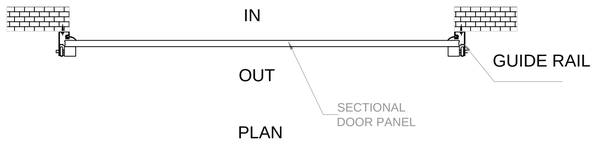

PLAN

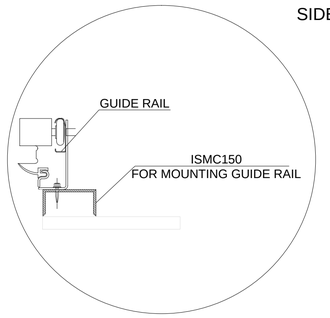

TRACK DETAILS

SR NO	CLEAR WIDTH (CW)	CLEAR HEIGHT (CH)	QUANTITY	EH	FH	TH	LOCATION
1	5000	5000	2	1500	4800	6500	

NOTE- 1. STRUCTURE REQUIRED FOR SECTIONAL DOOR SHALL BE IN CLIENT'S SCOPE.
2.COLOR FOR SECTIONAL DOOR PANEL WOULD BE RAL 5012(LIGHT BLUE)

This drawing & design is the property of NIHVA TECHNOLOGIES. Not be sold or copy to any other concern.

TITLE: SECTIONAL DOOR (HIGH LIFT) (MOTORIZED)

	SIGN	DATE
DRAWN	OMKAR	31/07/17
CHECK	SHEKHAR	31/07/17
REV.		
APPROVAL		

If any queries contact : projects@nihva.com

ALL DIMENSION ARE IN mm

NIHVA TECHNOLOGIES PVT. LTD.
NIHVA TECHNOLOGIES PVT. LTD. PUNE
Tel : 020 66304033
Email:- info@nihva.com
Website:- www.nihva.com

CLIENT - SCON PROJECTS
PROJECT - BEKAERT INDUSTRIES PVT. LTD.
SITE - RAJANGAON, MIDC
DWG. NO. : NIHVA/17-18/0142
SCALE: NTS | WT: | SHEET: 01 OF 01

PRODUCED BY AN AUTODESK EDUCATIONAL PRODUCT