
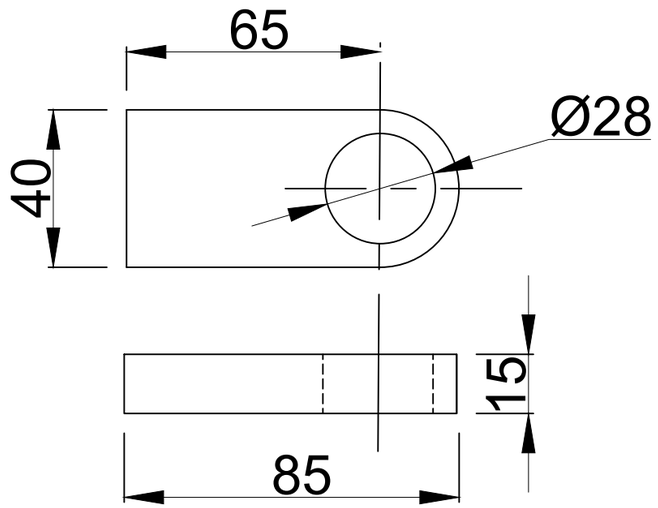


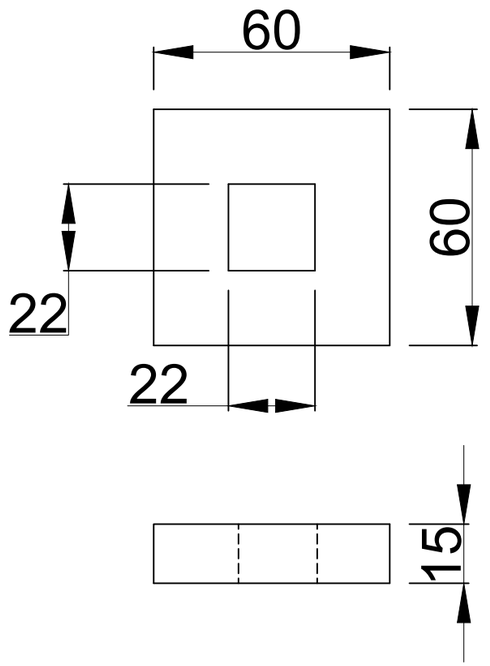

MNTG. BRACKET
40 X 85 X 15 MM THK
MTRL - M.S.
(TOWER BOLT ASM)

QTY= 75 NOS.

MNTG. BRACKET
60 X 60 X 15 MM THK
MTRL - M.S.
(EXTRA SUPPORT ASM)

QTY= 65 NOS.

This drawing & design is the property of NIHVA TECHNOLOGIES. Not to be sold or copied to any other concern.

	Date	Revised By

TITLE:- TOWER BOLT HANDLE PLATE

NIHVA TECHNOLOGIES PVT. LTD.

NIHVA TECHNOLOGIES PVT. LTD. PUNE
Tel : 020 66304033
Email:- info@nihva.com
Website:- www.nihva.com

	NAME	DATE	SIGN
DRAWN	M.SUTAR	15/06/2022	
CHECK	M.SUTAR	15/06/2022	
APPRD.			

If any queries contact : design@nihva.com

ALL DIMENSION ARE IN mm

CLIENT - NIHVA TECHNOLOGIES PVT.LTD

LOCATION -

PRODUCT - SLIDING DOOR

DWG NO:-NIHVA/22-23/VDR/0015 REV- 0

SCALE: NTS SCALE:-- 1:1 SHEET: 01 OF 01