


ITEM NO.	PART NUMBER	DESCRIPTION	SIZE MM	QTY
1	GNT006	PROFILE	L = 2780	5
2	GNT006	PROFILE	L = 991+100 = 1091	1
3	GNT006	PROFILE	L = 941+100 = 1041	1
4	GNT006	PROFILE	L = 2000+100 = 2100	2
5	GNT006	PROFILE	L = 1880+100 = 1900	1
6	GNT006	PROFILE	L = 300+100 = 400	1
7	PLATE 1	PROFILE	AL - 50X50X10	26
8	PLATE 2	PROFILE	AL - 200X120X10	2

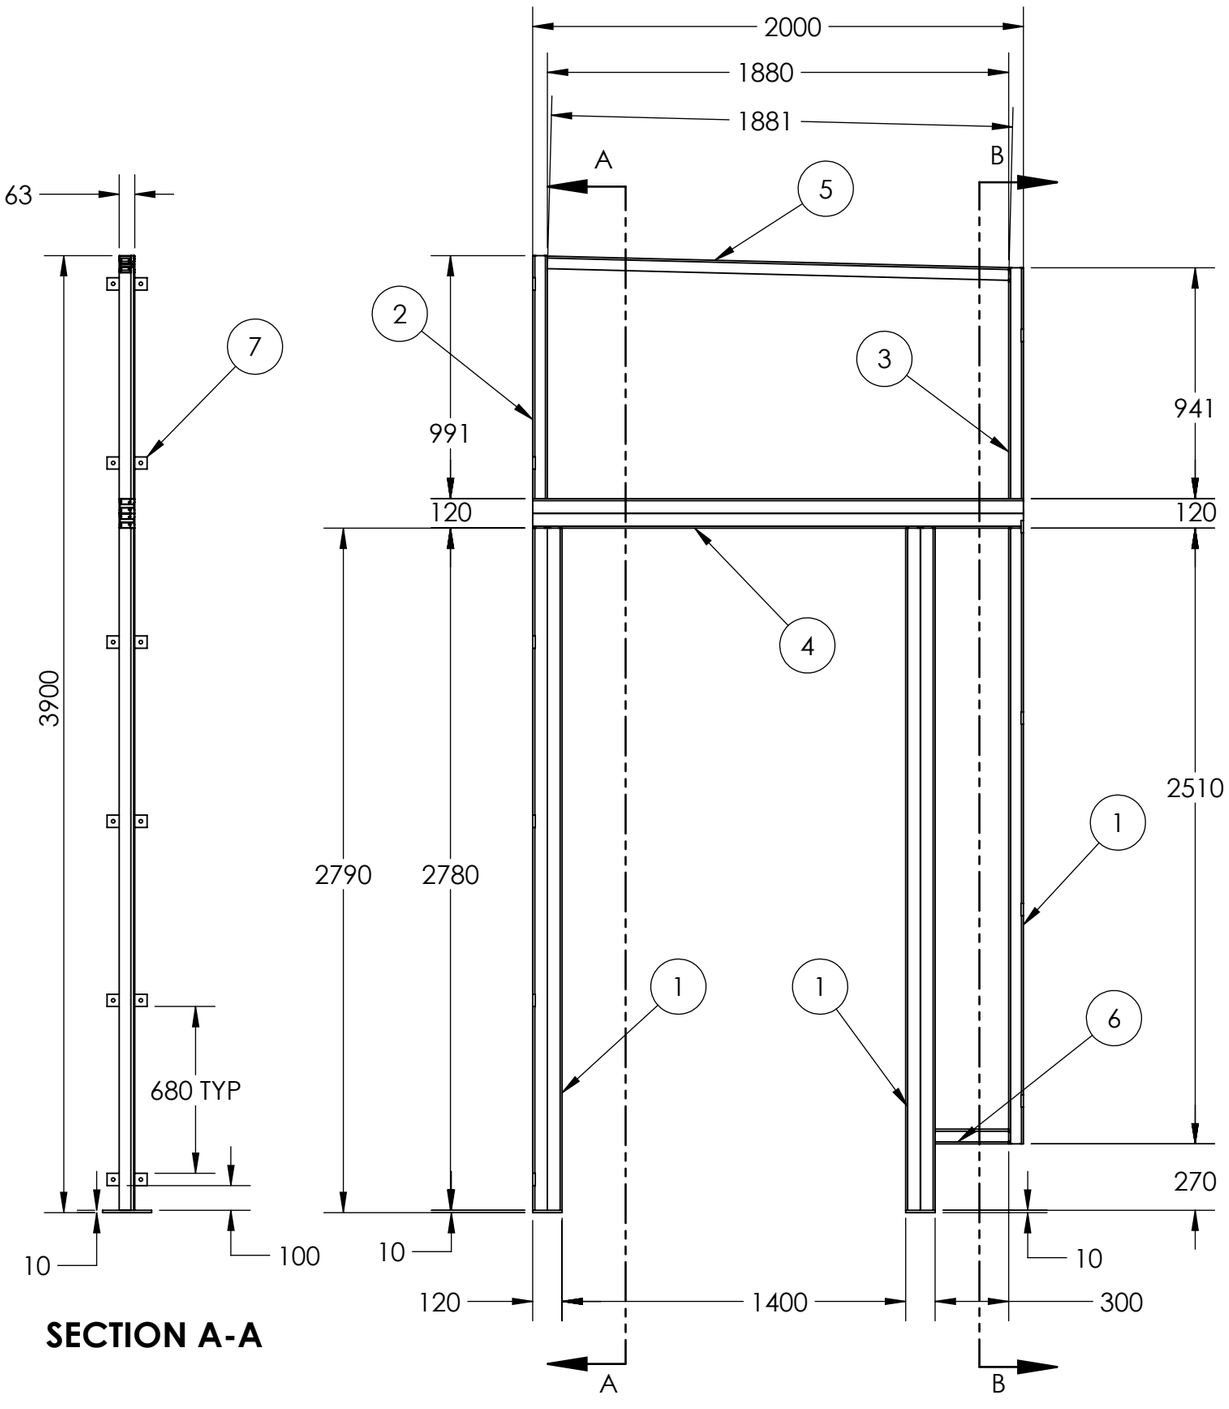


SECTION A-A

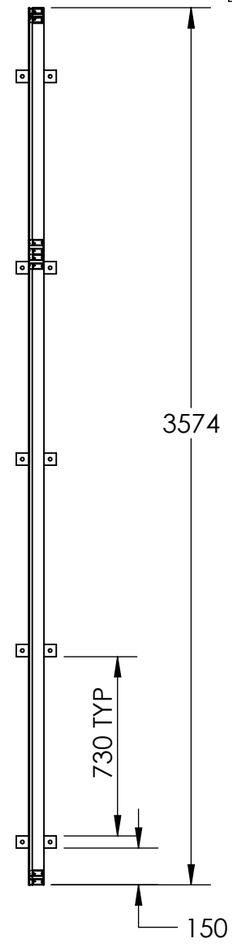

SECTION B-B

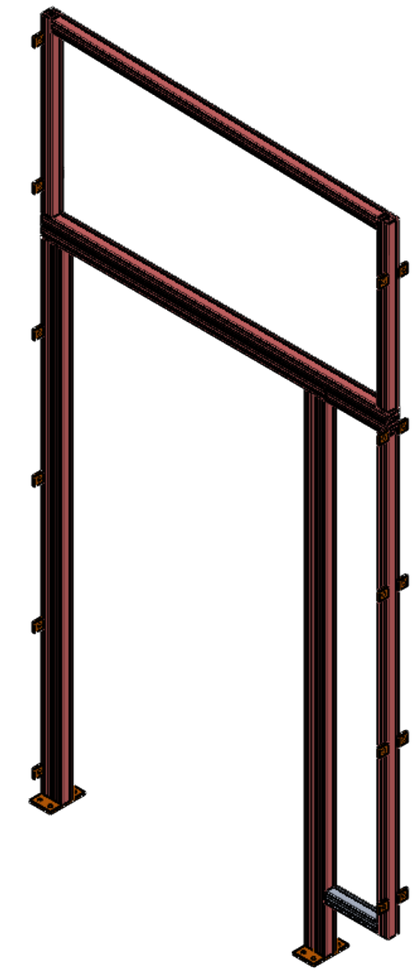

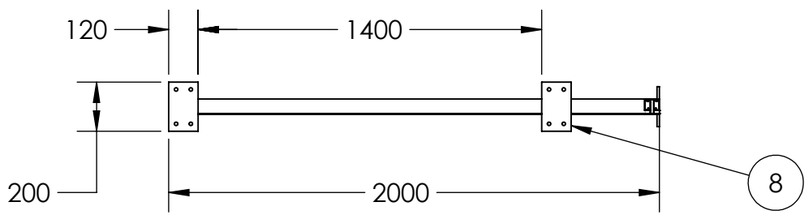

TITLE - ENTRY SIDE DOOR				NIHVA TECHNOLOGIES PVT.LTD.PUNE Website - www.nihva.com
DWG NO - NTPL160 - ENTRY SIDE DOOR			QTY - 1	
	NAME	SIGNATURE	DATE	PROJECT NO - NTPL160
DRAWN	D.V.		25.09.2023	PRODUCT - RETRACTABLE ROOF
CHK'D	P.M.		25.09.2023	SITE LOCATION -
APPV'D	V.T.		25.09.2023	
if any queries contact - supportautomation@nihva.com				REVISION -
ALL DIMENSION ARE IN mm			A3	SCALE - SHEET 1 OF 1