
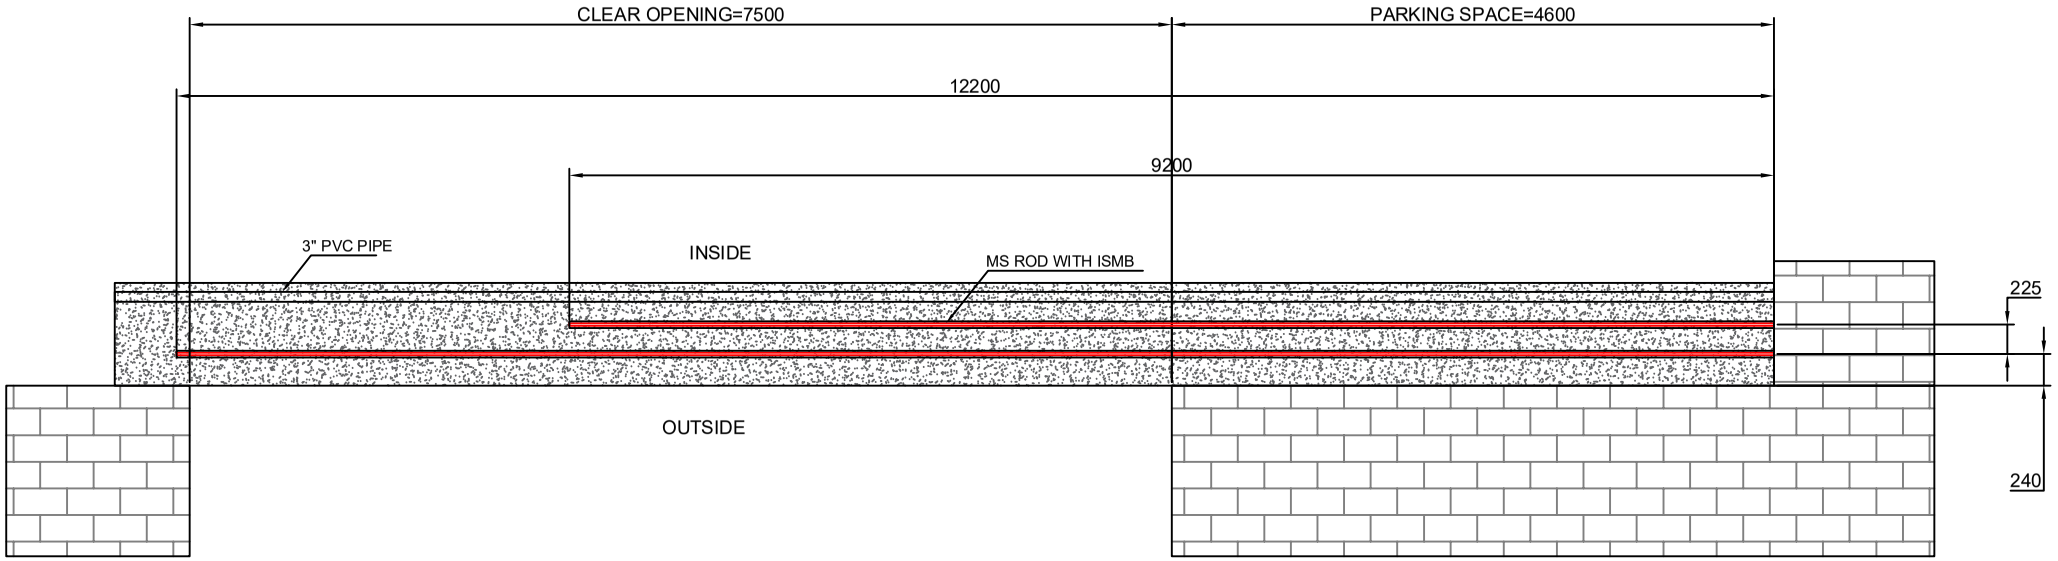


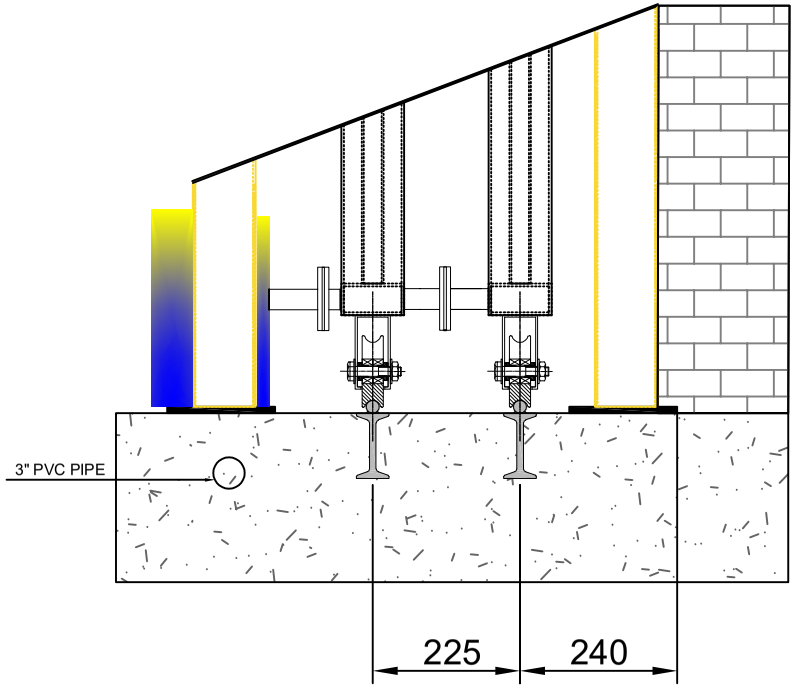

This drawing & design is the property of NIHVA TECHNOLOGIES. Not to be sold or copied to any other concern.

TITLE:- Two Leaf for tel.sliding gate foundation

NIHVA TECHNOLOGIES PVT. LTD.

NIHVA TECHNOLOGIES PVT. LTD. PUNE
Tel : 020 66304033
Email:- info@nihva.com
Website:- www.nihva.com

	NAME	DATE	SIGN
DRAWN	SUJATA	02/03/2022	
CHECK	G.PATIL	02/03/2022	
APPRD.	P.J	02/03/2022	

If any queries contact : design@nihva.com

ALL DIMENSION ARE IN mm

CLIENT - Kunal Structure Ind. Pvt. Ltd

LOCATION - Gujrat (Diyodar)

PRODUCT - Tel.sliding gate | QTY-

DWG NO:- NIHVA/21-22/CLT/0362 | REV- 0

SCALE: NTS | SCALE:-- 1:1 | SHEET: 01 OF 01

Rev No.	Revision	Date	Revised By