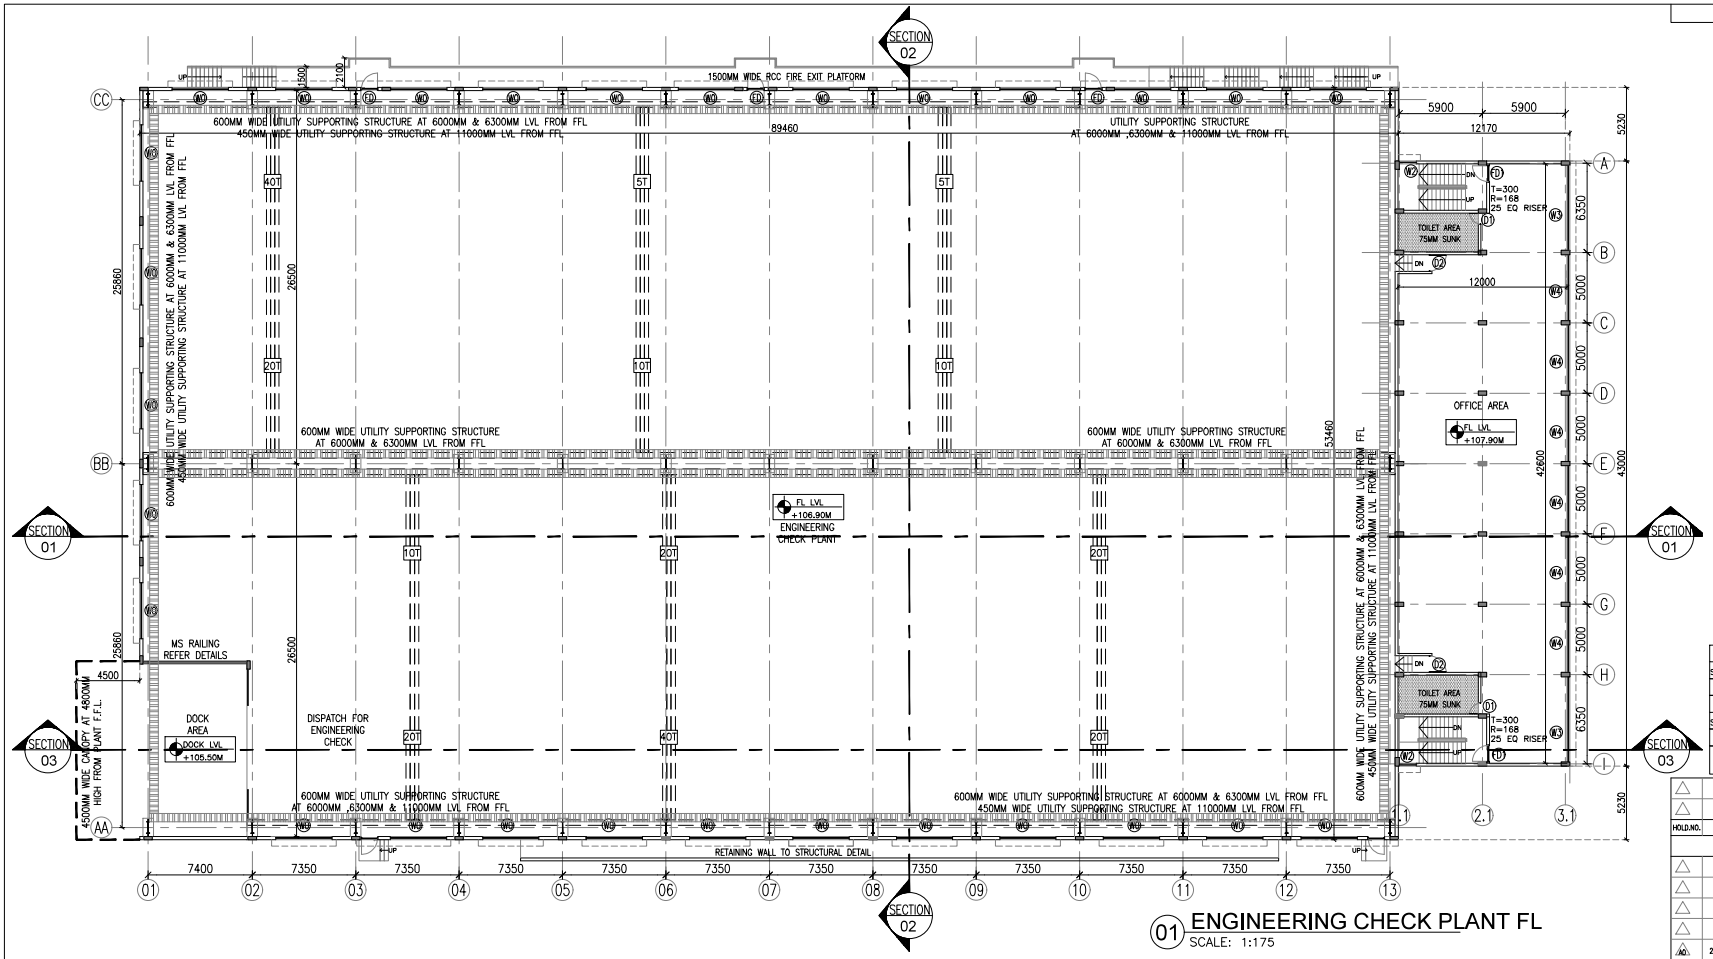


01 ENGINEERING CHECK PLANT FL
SCALE: 1:175


SCHEDULE OF DOORS					
S.NO	TYPE	SIZE	SILL	LINTEL FROM FFL	LOCATION
01	FD	1200 X 2250	--	2250	PLANT AREA

SCHEDULE OF WINDOWS					
S.NO	TYPE	SIZE	SILL	LINTEL FROM FFL	LOCATION
01	W0	4000 X 1950	300	2250	PLANT AREA

ALL DOORS/WINDOWS OPENING IN WALL ARE CONSTRUCTION OPENING. (i.e. UNPLASTERED SURFACE OF WALL)


HOLD.NO.	DATE	REASON FOR HOLD	SIGNED BY

REV.NO.	DATE	DESCRIPTION FOR REVISION	DRAWN BY	CHECKED BY
A0	24.09.2020	FOR SCHEMATIC APPROVAL	SAGAR	DEEPAK

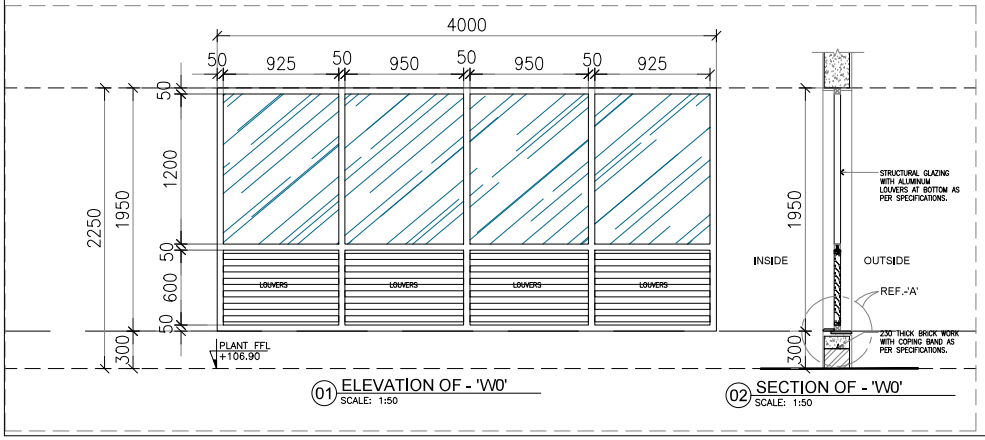


01 ELEVATION OF - 'W0'
SCALE: 1:50


02 SECTION OF - 'W0'
SCALE: 1:50

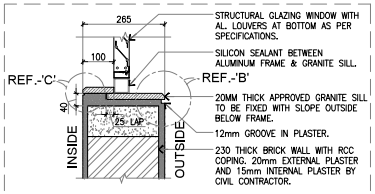

03 DETAIL @ 'A'
SCALE: 1:10

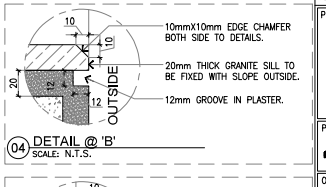

04 DETAIL @ 'B'
SCALE: N.T.S.

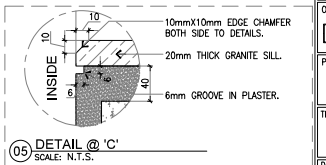

05 DETAIL @ 'C'
SCALE: N.T.S.

PURPOSE:VA

PROJECT MANAGER
CUSHMAN & WAKEFIELD INDIA PVT LTD

OWNER
M/S CRANE PROCESS FLOW TECHNOLOGIES (I) LTD


PROJECT
CRANE CPE BROWNFIELD EXPANSION - SATARA

TITLE
ENGINEERING CHECK PLANT
FLOOR PLAN

N

DEALT	JOB NO	REVISION
DEEPAK	281.01.08.20	A0
SCALE 1:200	DATE 24.09.20	DRAWING NO B1-A-2001

Venkataramanan Associates
AR SITE TO C-U DAS SINGH
VISHNU, 1ST FLOOR, PLOT NO.36, BHARATNAJ HSG. SOC., PUNE 38

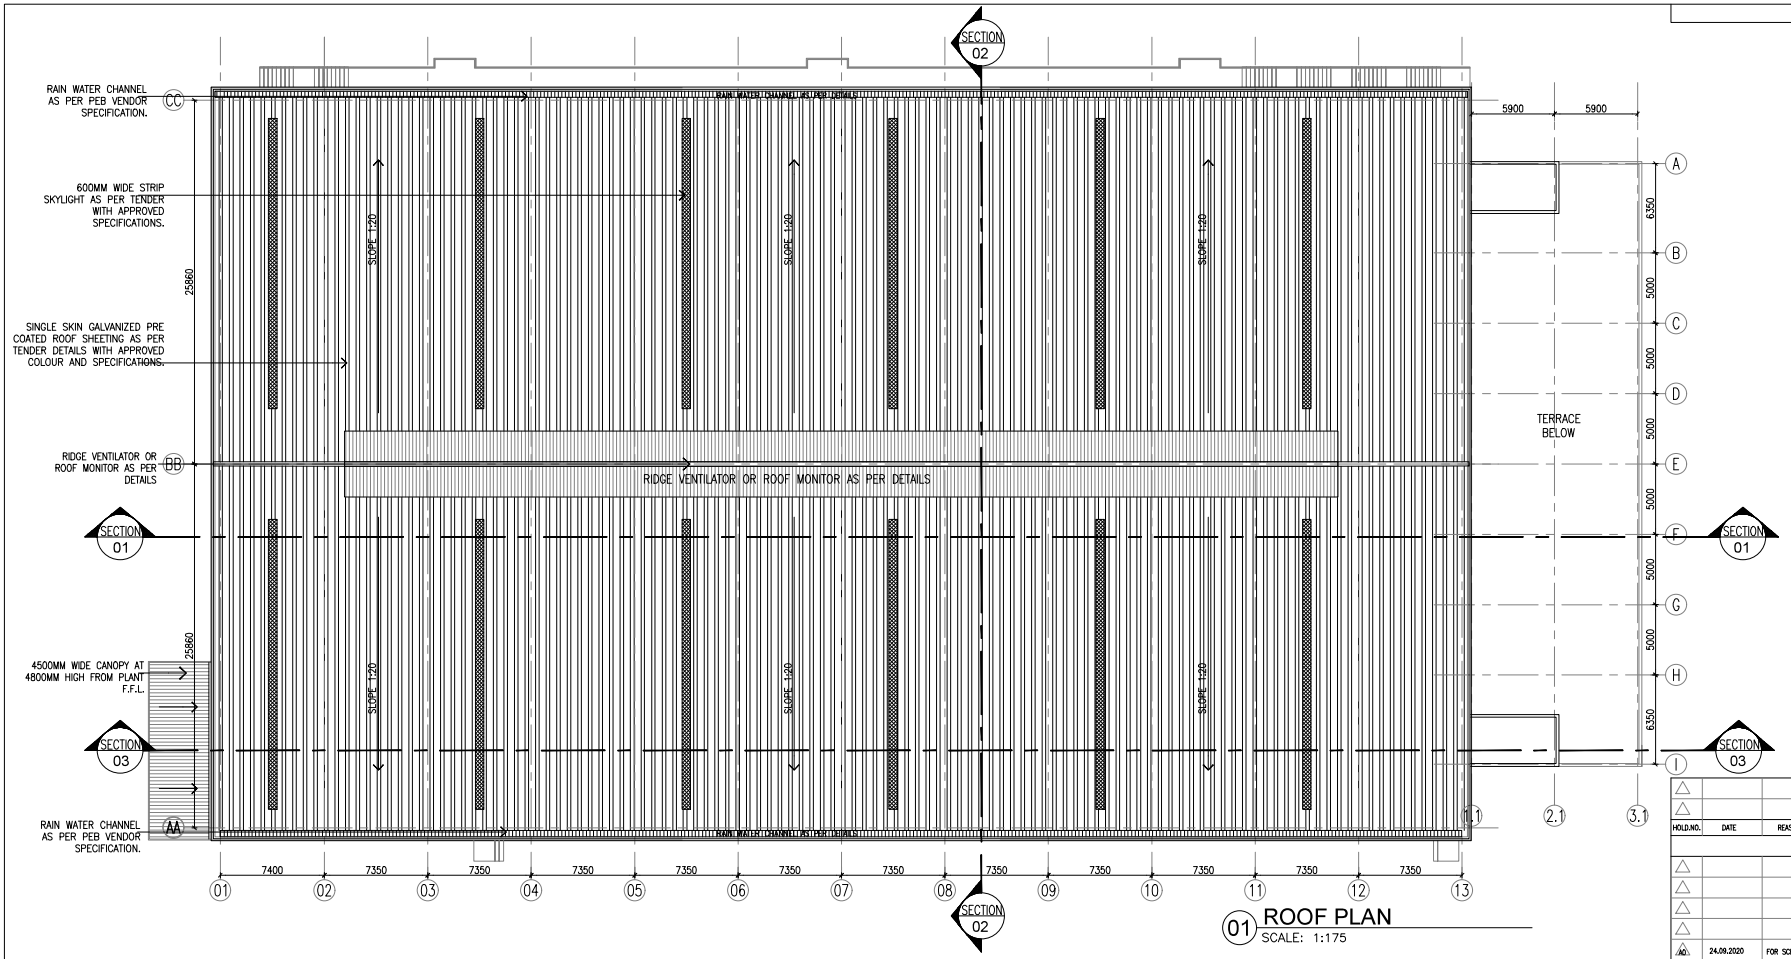

01 ROOF PLAN
SCALE: 1:175

HOLD.NO.	DATE	REASON FOR HOLD	SIGNED BY

REV.NO.	DATE	DESCRIPTION FOR REVISION	DRAWN BY	CHECKED BY
A0	24.09.2020	FOR SCHEMATIC APPROVAL	SAGAR	DEEPAK

PURPOSE:VA

PROJECT MANAGER
CUSHMAN & WAKEFIELD INDIA PVT LTD


OWNER
M/S CRANE PROCESS FLOW TECHNOLOGIES (I) LTD

PROJECT
CRANE CPE BROWNFIELD EXPANSION - SATARA


TITLE
ENGINEERING CHECK PLANT
ROOF PLAN

DEALT	JOB NO	REVISION
DEEPAK	281.01.08.20	A0
SCALE: 1:200	DATE: 24.09.20	DRAWING NO: B1-A-2002


Venkataramanan Associates
AN ISO 9001:2008
VENUS, 1ST FLOOR, PLOT NO.56, BHARATNAGAR HSG. SOC., PUNE 38

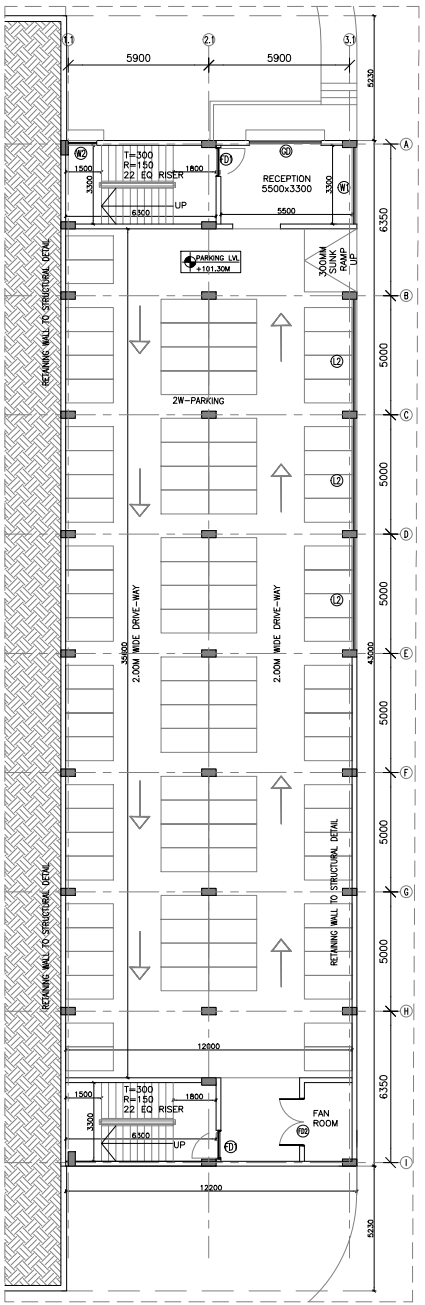

01 PARKING FLOOR @ 101.30 LVL
SCALE: 1:100

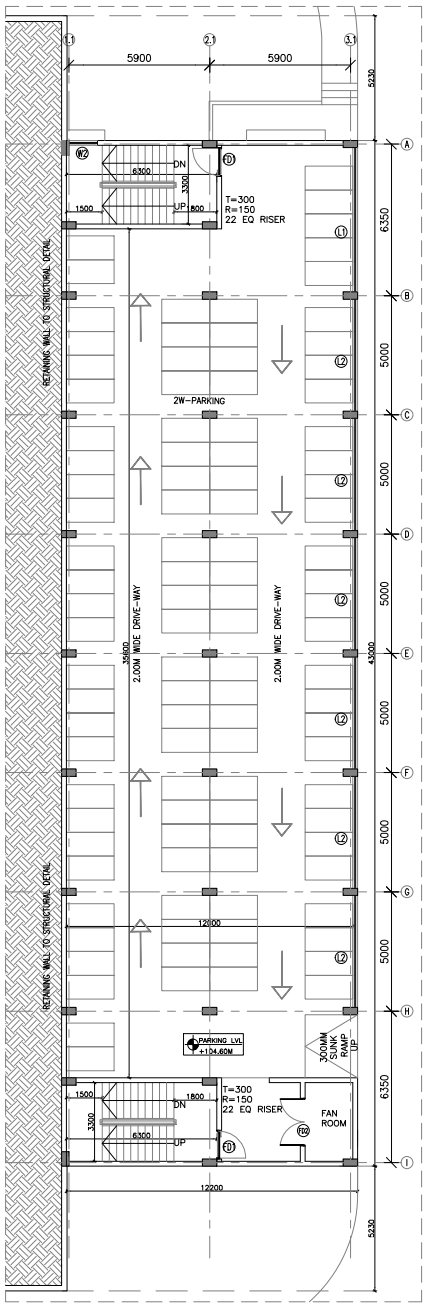

02 PARKING FLOOR @ 104.60 LVL
SCALE: 1:100

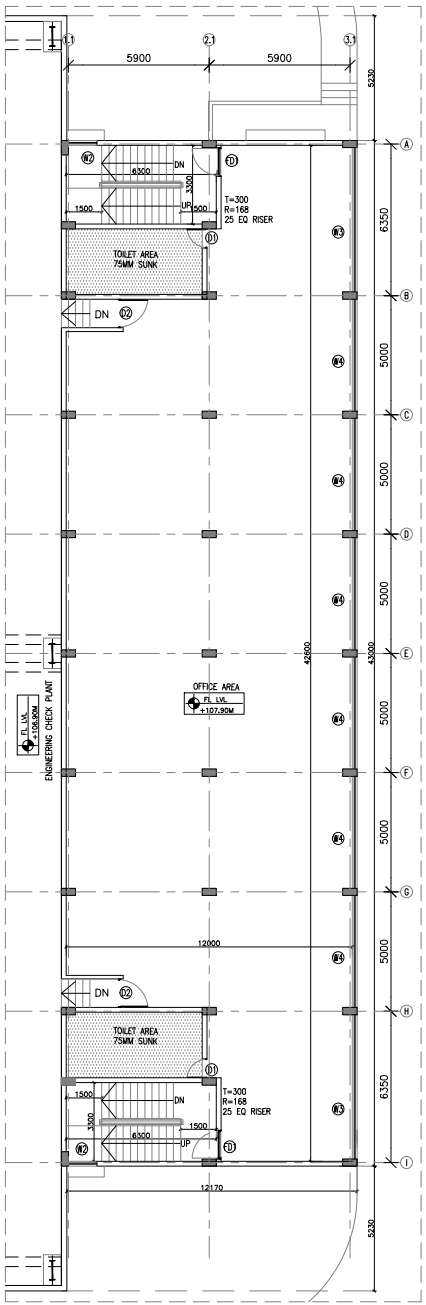

03 OFFICE FLOOR @ 107.90 LVL.
SCALE: 1:100

SCHEDULE OF DOORS					
S.NO	TYPE	SIZE	SILL	LINTEL FROM FFL	LOCATION
01	FD1	1200 X 2250	–	2250	STAIRCASE
02	FD2	2000 X 2250	–	2250	FAN ROOM
03	GD	3000 X 2250	–	2250	RECEPTION
04	D1	800 X 2250	–	2250	TOILET
05	D2	1200 X 2250	–	2250	OFFICE

SCHEDULE OF WINDOWS					
S.NO	TYPE	SIZE	SILL	LINTEL FROM FFL	LOCATION
01	W1	3200 X 2100	150	2250	RECEPTION
02	W2	1200 X 1200	1050	2250	STAIRCASE
03	W3	6050 X 2100	150	2250	OFFICE AREA
04	W4	4700 X 2100	150	2250	OFFICE AREA
05	L1	6050 X 2100	300	2250	PARKING AREA
06	L2	4700 X 2100	300	2250	PARKING AREA

ALL DOORS/WINDOWS OPENING IN WALL ARE CONSTRUCTION OPENING.
(i.e. UNPLASTERED SURFACE OF WALL)

HOLD.NO.	DATE	REASON FOR HOLD	SIGNED BY

NO.	DATE	DESCRIPTION FOR REVISION	DRAWN BY	CHECKED BY
1	24.09.2020	FOR SCHEMATIC APPROVAL	SAGAR	DEEPAK

PURPOSE:VA

PROJECT MANAGER
CUSHMAN & WAKEFIELD INDIA PVT LTD

OWNER
M/S CRANE PROCESS FLOW TECHNOLOGIES (I) LTD


PROJECT
CRANE CPE BROWNFIELD EXPANSION - SATARA

TITLE
PARKING LEVEL & OFFICE FLOORS


N

DEALT	JOB NO	REVISION
DEEPAK	281.01.08.20	A0
SCALE: 1:200	DATE: 24.09.20	DRAWING NO: B1-A-2003

Venkataramanan Associates
AN ISO 9001:2008 CERTIFIED
'VEDANT', 1ST FLOOR, PLOT NO.52, BHARATNAGAR HSG. SOC., PUNE 38

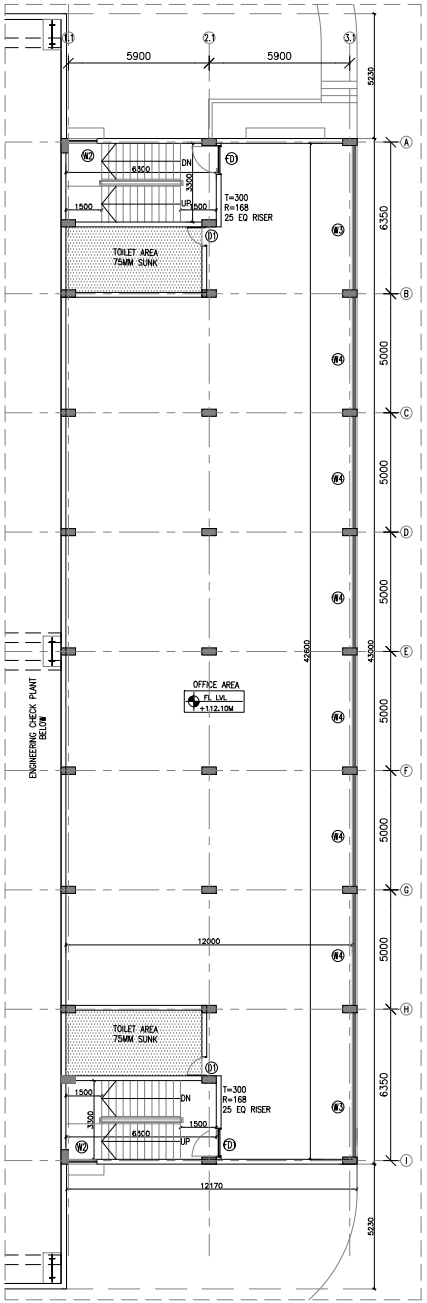

01 OFFICE FLOOR @ 112.10M LVL.
SCALE: 1:100

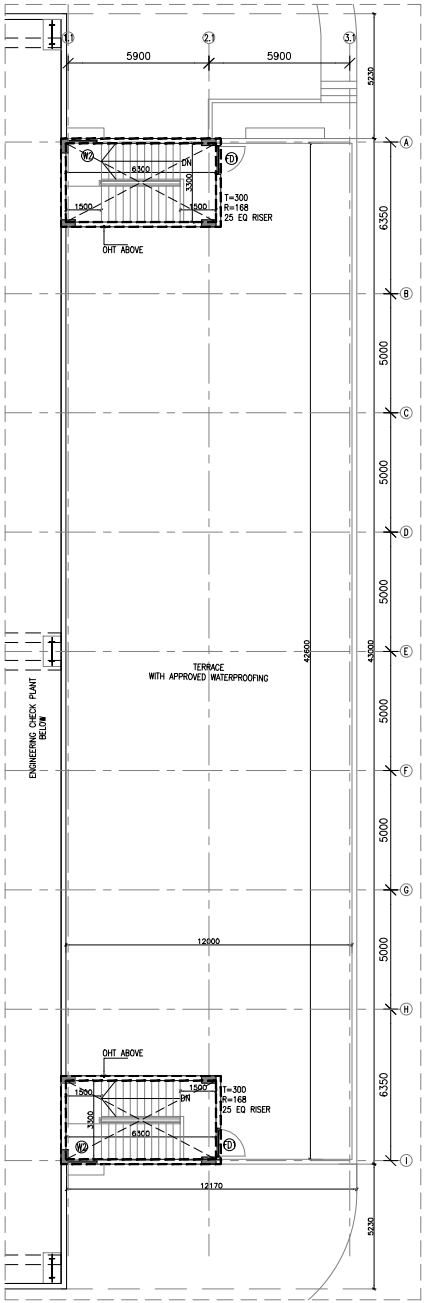

02 TERRACE FLOOR
SCALE: 1:100

SCHEDULE OF DOORS

S.NO	TYPE	SIZE	SILL	LINTEL FROM FFL	LOCATION
01	FD1	1200 X 2250	–	2250	STAIRCASE
02	FD2	2000 X 2250	–	2250	FAN ROOM
03	GD	3000 X 2250	–	2250	RECEPTION
04	D1	800 X 2250	–	2250	TOILET
05	D2	1200 X 2250	–	2250	OFFICE

SCHEDULE OF WINDOWS

S.NO	TYPE	SIZE	SILL	LINTEL FROM FFL	LOCATION
01	W1	3200 X 2100	150	2250	RECEPTION
02	W2	1200 X 1200	1050	2250	STAIRCASE
03	W3	6050 X 2100	150	2250	OFFICE AREA
04	W4	4700 X 2100	150	2250	OFFICE AREA
05	L1	6050 X 2100	300	2250	PARKING AREA
06	L2	4700 X 2100	300	2250	PARKING AREA

ALL DOORS/WINDOWS OPENING IN WALL ARE CONSTRUCTION OPENING.
(i.e. UNPLASTERED SURFACE OF WALL)

HOLD.NO.	DATE	REASON FOR HOLD	SIGNED BY

REV.NO.	DATE	DESCRIPTION FOR REVISION	DRAWN BY	CHECKED BY
A0	24.09.2020	FOR SCHEMATIC APPROVAL	SAGAR	DEEPAK

PURPOSE:VA

PROJECT MANAGER
CUSHMAN & WAKEFIELD INDIA PVT LTD

OWNER
M/S CRANE PROCESS FLOW TECHNOLOGIES (I) LTD


PROJECT
CRANE CPE BROWNFIELD EXPANSION - SATARA

TITLE
OFFICE FLOORS


N

DEALT	JOB NO		REVISION
DEEPAK	281.01.08.20		A0
SCALE 1:200	DATE 24.09.20	DRAWING NO B1-A-2004	

Venkataramanan Associates
AR SITE TO C-U DAS SINGH
VISHVA, 1ST FLOOR, PLOT NO.56, BHARATNAGAR HSG. SOC., PUNE 38

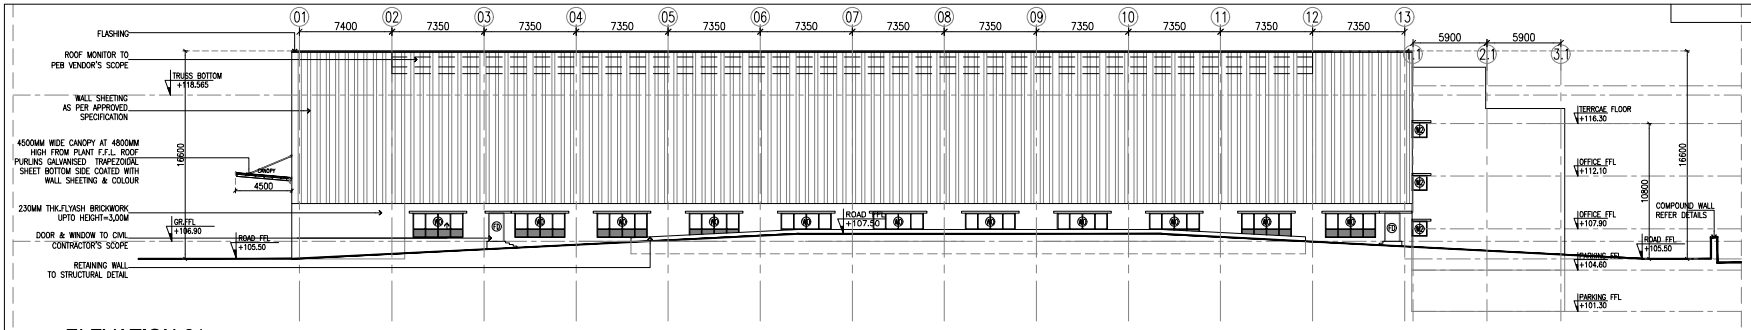

01 ELEVATION-01
SCALE: 1:200

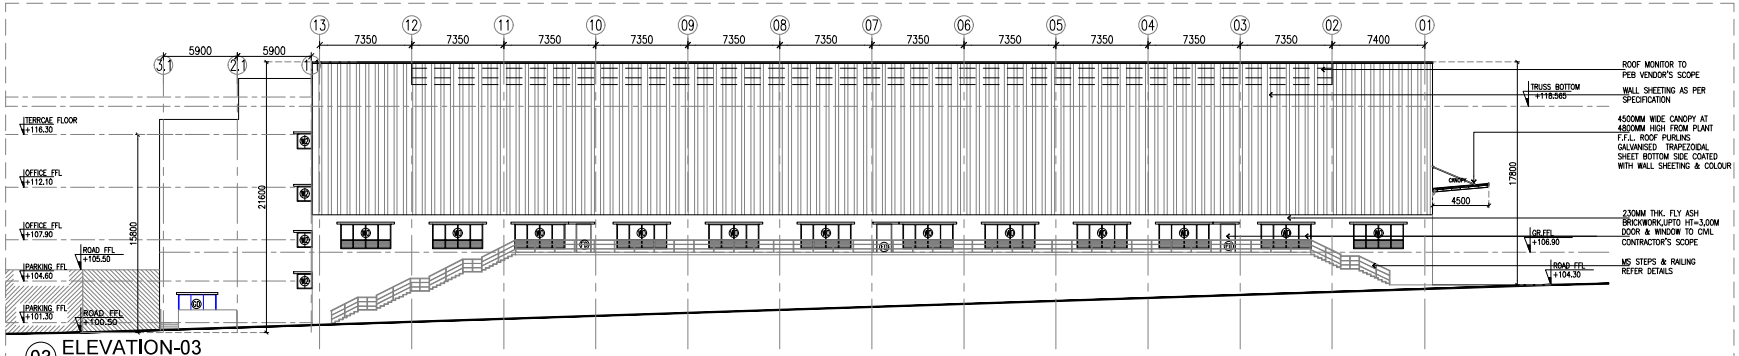

03 ELEVATION-03
SCALE: 1:200

SCHEDULE OF DOORS

S.NO	TYPE	SIZE	SILL	LINTEL FROM FFL	LOCATION
01	FD1	1200 X 2250	–	2250	STAIRCASE
02	FD2	2000 X 2250	–	2250	FAN ROOM
03	GD	3000 X 2250	–	2250	RECEPTION
04	D1	800 X 2250	–	2250	TOILET
05	D2	1200 X 2250	–	2250	OFFICE

SCHEDULE OF WINDOWS

S.NO	TYPE	SIZE	SILL	LINTEL FROM FFL	LOCATION
01	W1	3200 X 2100	150	2250	RECEPTION
02	W2	1200 X 1200	1050	2250	STAIRCASE
03	W3	6050 X 2100	150	2250	OFFICE AREA
04	W4	4700 X 2100	150	2250	OFFICE AREA
05	L1	6050 X 2100	300	2250	PARKING AREA
06	L2	4700 X 2100	300	2250	PARKING AREA

ALL DOORS/WINDOWS OPENING IN WALL ARE CONSTRUCTION OPENING. (i.e. UNPLASTERED SURFACE OF WALL)

HOLD.NO.	DATE	REASON FOR HOLD	SIGNED BY

NO.	24.09.2020	FOR SCHEMATIC APPROVAL	SAGAR	DEEPAK
REV.NO.	DATE	DESCRIPTION FOR REVISION	DRAWN BY	CHECKED BY

PURPOSE:VA

PROJECT MANAGER
CUSHMAN & WAKEFIELD INDIA PVT LTD

OWNER
M/S CRANE PROCESS FLOW TECHNOLOGIES (I) LTD


PROJECT
CRANE CPE BROWNFIELD EXPANSION - SATARA

TITLE
ELEVATION-01,03


N

DEALT	JOB NO	REVISION
DEEPAK	281.01.08.20	A0
SCALE: 1:200	DATE: 24.09.20	DRAWING NO: B1-A-3001

Venkataramanan Associates
AN ISO 9001:2008 CERTIFIED
VISHNU, 1ST FLOOR, PLOT NO.56, BHARATNAGAR HSG. SOC., PUNE 38

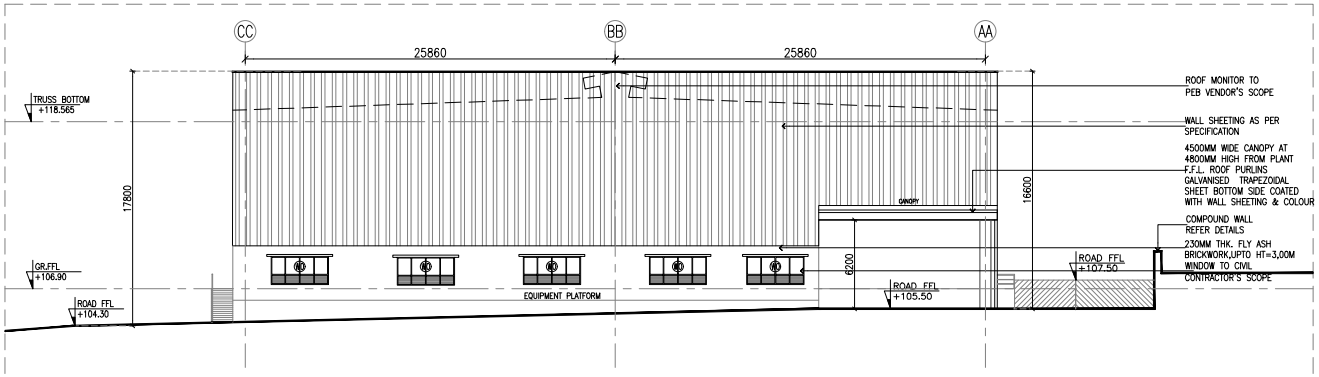

02 ELEVATION-02
SCALE: 1:200

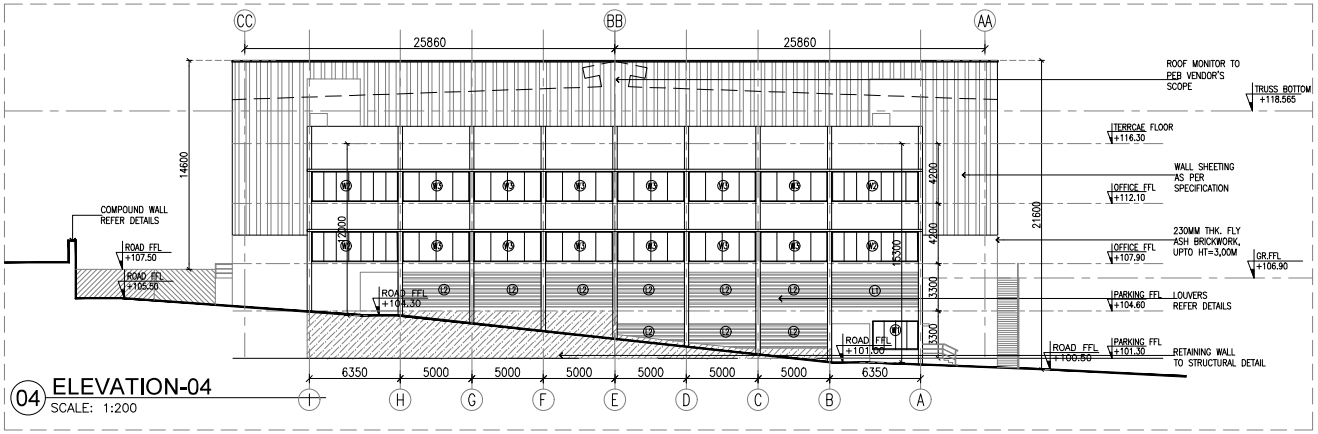

04 ELEVATION-04
SCALE: 1:200

SCHEDULE OF DOORS

S.NO	TYPE	SIZE	SILL	LINTEL FROM FFL	LOCATION
01	FD1	1200 X 2250	–	2250	STAIRCASE
02	FD2	2000 X 2250	–	2250	FAN ROOM
03	GD	3000 X 2250	–	2250	RECEPTION
04	D1	800 X 2250	–	2250	TOILET
05	D2	1200 X 2250	–	2250	OFFICE

SCHEDULE OF WINDOWS

S.NO	TYPE	SIZE	SILL	LINTEL FROM FFL	LOCATION
01	W1	3200 X 2100	150	2250	RECEPTION
02	W2	1200 X 1200	1050	2250	STAIRCASE
03	W3	6050 X 2100	150	2250	OFFICE AREA
04	W4	4700 X 2100	150	2250	OFFICE AREA
05	L1	6050 X 2100	300	2250	PARKING AREA
06	L2	4700 X 2100	300	2250	PARKING AREA

ALL DOORS/WINDOWS OPENING IN WALL ARE CONSTRUCTION OPENING.
(i.e. UNPLASTERED SURFACE OF WALL)

HOLD.NO.	DATE	REASON FOR HOLD	SIGNED BY

NO.	24.09.2020	FOR SCHEMATIC APPROVAL	SAGAR	DEEPAK
REV.NO.	DATE	DESCRIPTION FOR REVISION	DRAWN BY	CHECKED BY

PURPOSE:VA

PROJECT MANAGER
CUSHMAN & WAKEFIELD INDIA PVT LTD

OWNER
M/S CRANE PROCESS FLOW TECHNOLOGIES (I) LTD


PROJECT
CRANE CPE BROWNFIELD EXPANSION - SATARA

TITLE
ELEVATION-02,04


N

DEALT	JOB NO		REVISION
DEEPAK	281.01.08.20		A0
SCALE	DATE	DRAWING NO	
1:200	24.09.20	B1-A-3002	


Venkataramanan Associates
AN ISO 9001 : 2008
VENUS, 1ST FLOOR, PLOT NO.56, BHARATNAGAR HSG. SOC., PUNE 38

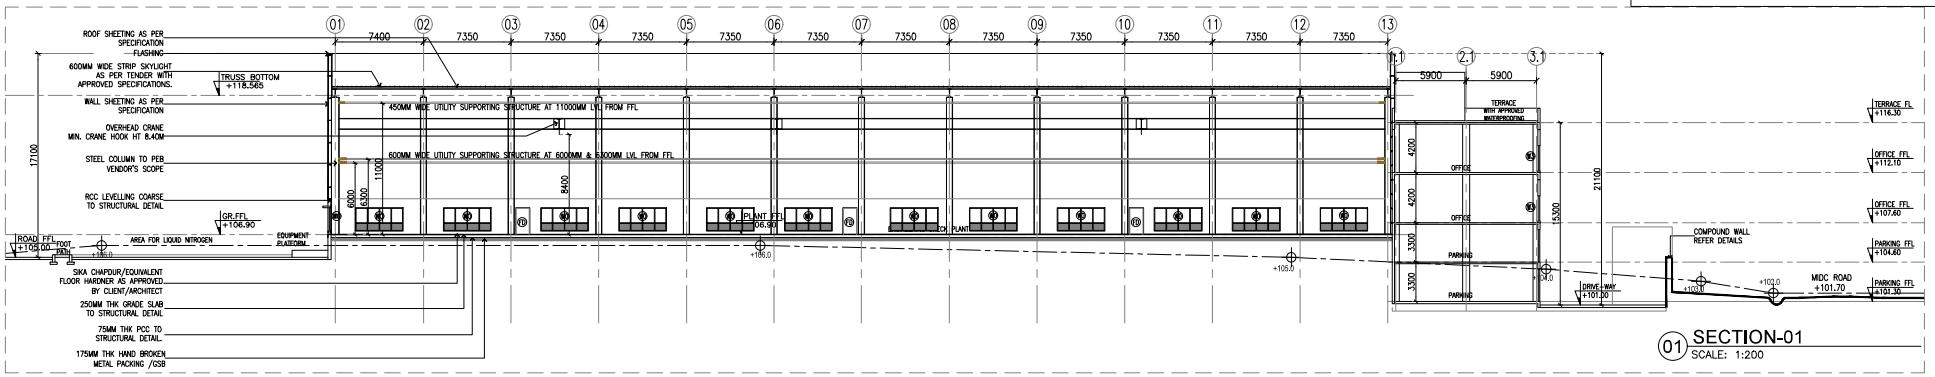

01 SECTION-01
SCALE: 1:200

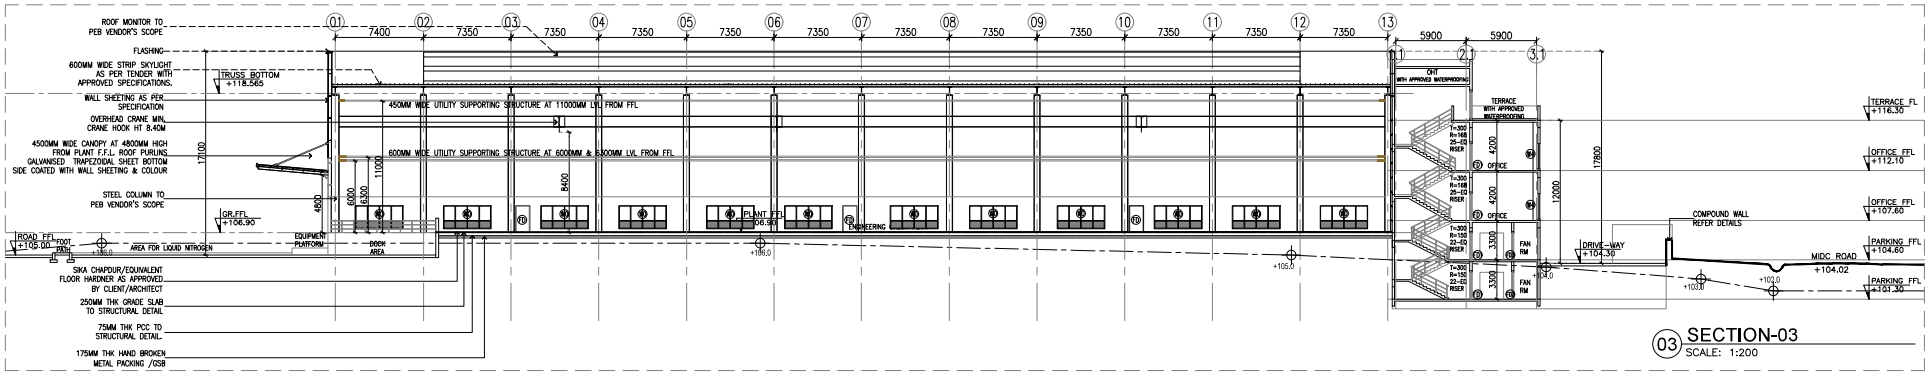

03 SECTION-03
SCALE: 1:200

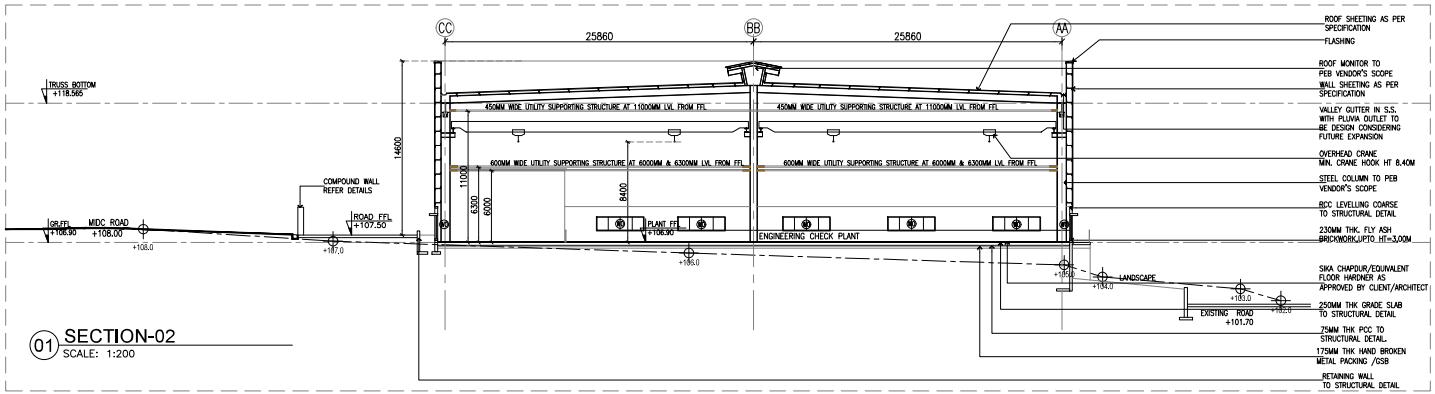

01 SECTION-02
SCALE: 1:200

HOLD.NO.	DATE	REASON FOR HOLD	SIGNED BY

REV.NO.	DATE	DESCRIPTION FOR REVISION	DRAWN BY	CHECKED BY
A0.	24.09.2020	FOR SCHEMATIC APPROVAL	SAGAR	DEEPAK

PURPOSE:VA

PROJECT MANAGER
CUSHMAN & WAKEFIELD INDIA PVT LTD

OWNER
M/S CRANE PROCESS FLOW TECHNOLOGIES (I) LTD


PROJECT
CRANE CPE BROWNFIELD EXPANSION - SATARA

TITLE
SECTION-01,02 & 03


N

DEALT	JOB NO	REVISION
DEEPAK	281.01.08.20	A0
SCALE: 1:200	DATE: 24.09.20	DRAWING NO: B1-A-3101


Venkataramanan Associates
AN ISO 9001:2008 CERTIFIED
MOUNT, 1ST FLOOR, PLOT NO.56, BHARATNAJU HSG. SOC., PUNE 38

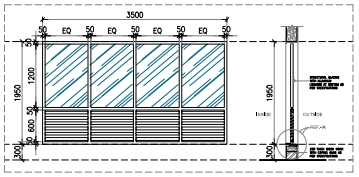


07 ELEVATION OF - W1
SCALE: 1:25
SQU GLAZING WINDOW

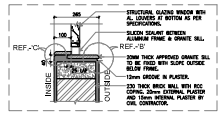


09 DETAIL @ 'A'
SCALE: 1:10

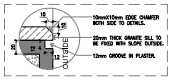


10 DETAIL @ 'B'
SCALE: N.T.S.

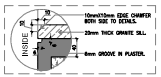

11 DETAIL @ 'C'
SCALE: N.T.S.

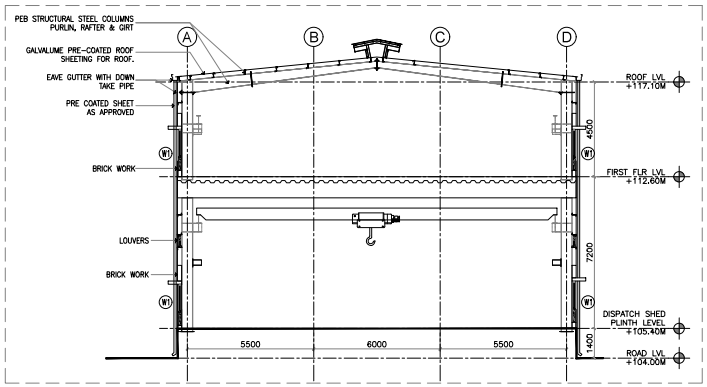


04 SECTION - A
SCALE: 1:100
DISPATCH SHED

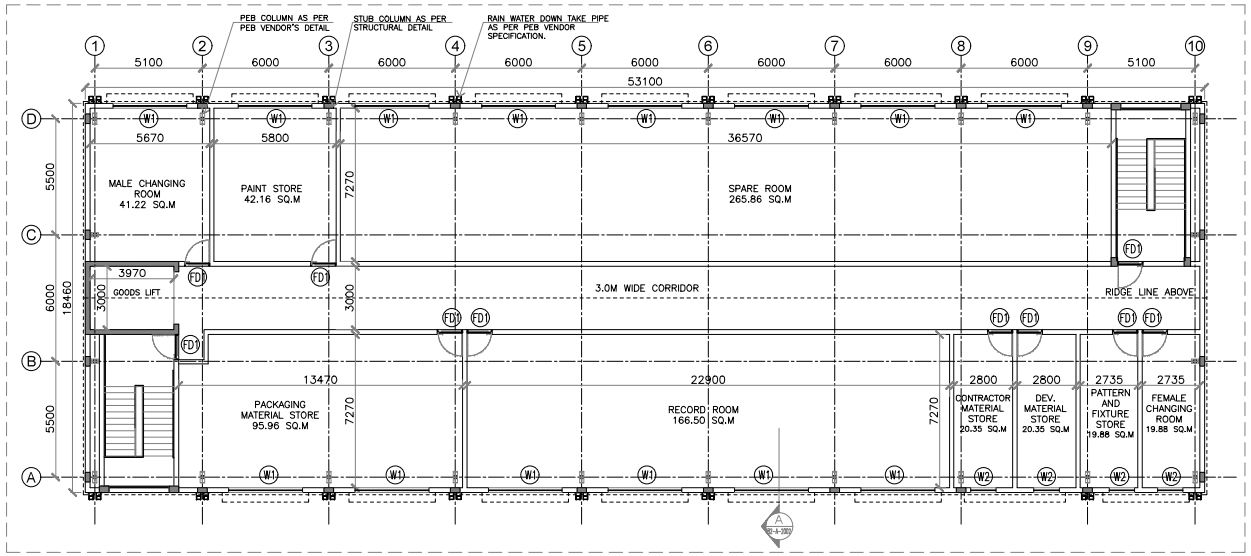

02 FIRST FLOOR PLAN
SCALE: 1:100
DISPATCH SHED

SCHEDULE OF OPENINGS - DOOR					
SR.NO	TYPE	SIZE	SILL	LINTEL (FROM FFL)	LOCATION
01	FD1	1200X2250	–	2250	CASTING, SPARE ROOM, STAIRCASE, RECORD ROOM, PACKAGING, ETC
SCHEDULE OF OPENINGS - WINDOWS					
01	W1	3500X1200	300	2250	DISPATCH SHED, SPARE ROOM, RECORD ROOM, PACKAGING ETC
02	W2	1200X1200	–	2250	CONTRACTOR MATERIAL STORE, DEV.MATERIAL STORE,, PATTERAN AND FIXTURE STORE, FEMALE CHANGING ROOM
SCHEDULE OF OPENINGS - ROLLING SHUTTERS					
01	RS1	4000X3000	–	3000	DOCK AREA
02	RS2	3000X3000	–	3000	FORK LIFT
03	RS3	3000X3000	–	3000	NON-HAZ. WASTE
04	RS4	3000X3000	–	3000	FABRICATION
05	RS5	3000X3000	–	3000	PHOSPHATING
06	RS6	3000X3000	–	3000	SHOT BLASTING

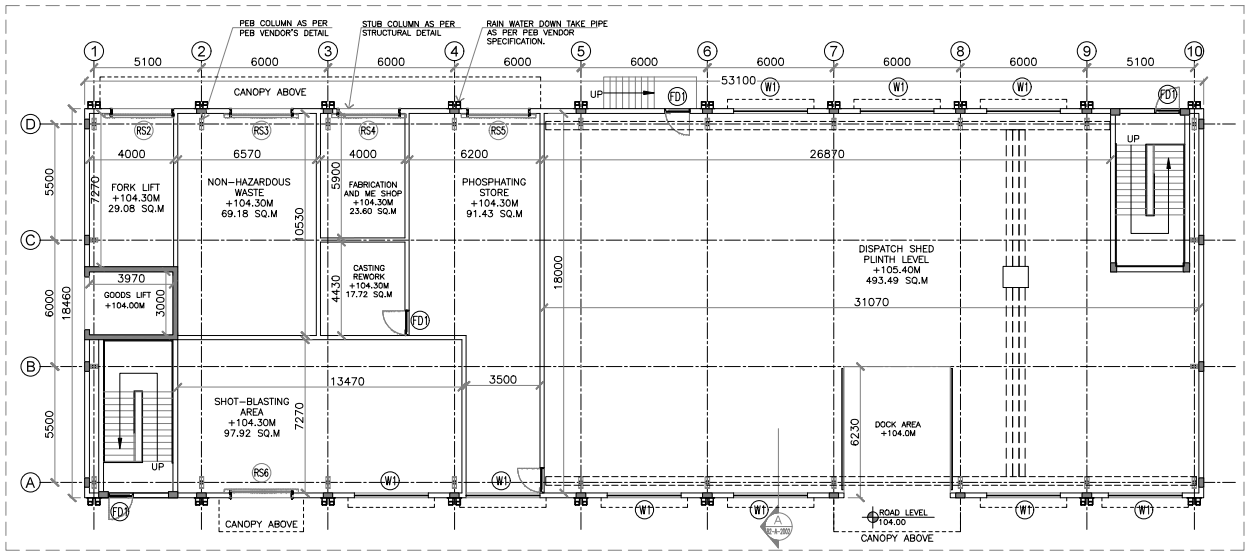

01 GROUND FLOOR PLAN
SCALE: 1:100
DISPATCH SHED

HOLD NO.	DATE	REASON FOR HOLD	SIGNED BY

NO.	DATE	DESCRIPTION FOR REVISION	DRAWN BY	CHECKED BY
0	24.09.2020	FOR SCHEMATIC APPROVAL	PRATIK	DEEPAK

PURPOSE:VA

PROJECT MANAGER
CUSHMAN & WAKEFIELD INDIA PVT LTD

OWNER
M/S CRANE PROCESS FLOW TECHNOLOGIES (I) LTD


PROJECT
CRANE CPE BROWNFIELD EXPANSION - SATARA

TITLE
DISPATCH SHED


N

DEALT	JOB NO		REVISION
DEEPAK	281.01.08.20		A0
SCALE 1:200	DATE 24.09.20	DRAWING NO B3-A-2001	


Venkataramanan Associates
AN ISO 9001:2008 CERTIFIED
'VEDUS', 1ST FLOOR, PLOT NO.52, BHARATIJUNJ HSG. SOC., PUNE 38

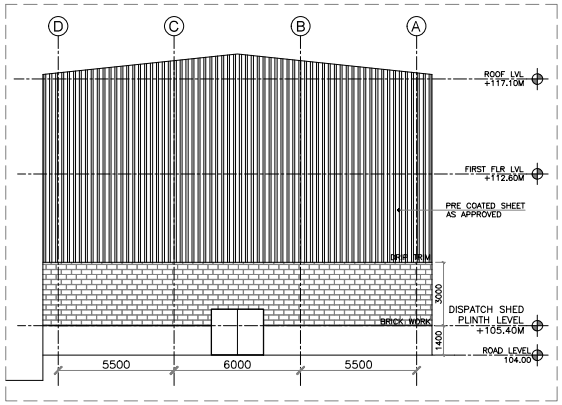

06 ELEVATION
SCALE: 1:100
DISPATCH SHED

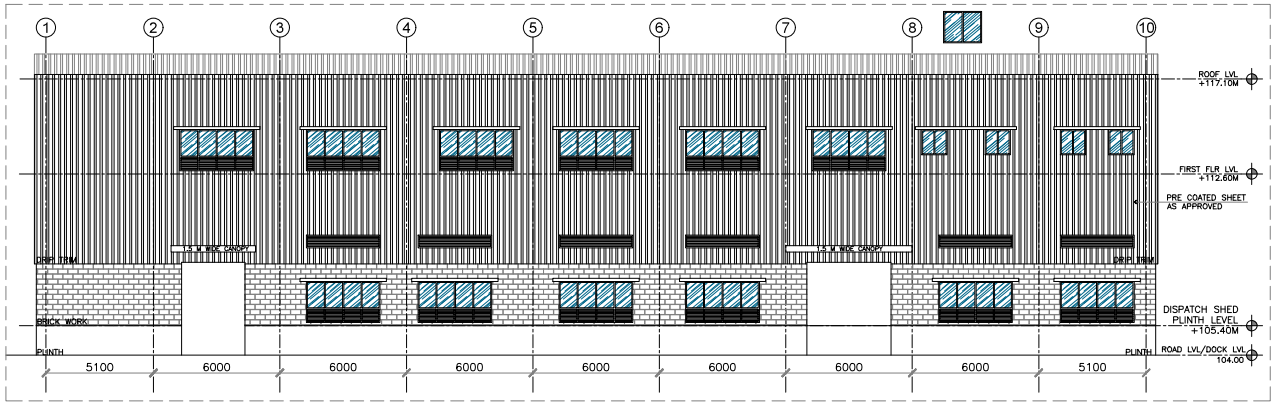

05 ELEVATION
SCALE: 1:100
DISPATCH SHED

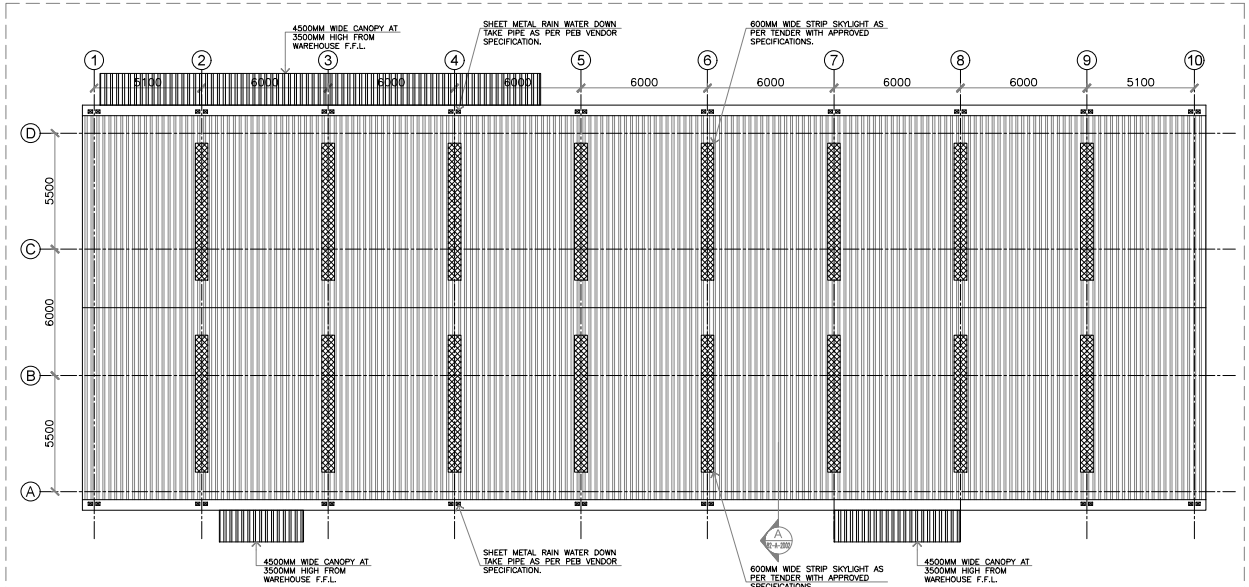

03 ROOF PLAN
SCALE: 1:100
DISPATCH SHED

HOLD NO.	DATE	REASON FOR HOLD	SIGNED BY

REV.NO.	DATE	DESCRIPTION FOR REVISION	DRAWN BY	CHECKED BY
0	24.09.2020	FOR SCHEMATIC APPROVAL	PRATIK	DEEPAK

PURPOSE:VA

PROJECT MANAGER
CUSHMAN & WAKEFIELD INDIA PVT LTD

OWNER
M/S CRANE PROCESS FLOW TECHNOLOGIES (I) LTD


PROJECT
CRANE CPE BROWNFIELD EXPANSION - SATARA

TITLE
DISPATCH SHED

N

DEALT	JOB NO	REVISION
DEEPAK	281.01.08.20	A0
SCALE 1:200	DATE 24.09.20	DRAWING NO B3-A-2002

Venkataramanan Associates
AN ISO 9001:2008 CERTIFIED
'VEDUS', 1ST FLOOR, PLOT NO.52, BHARATKUNJ HSG. SOC., PUNE 38

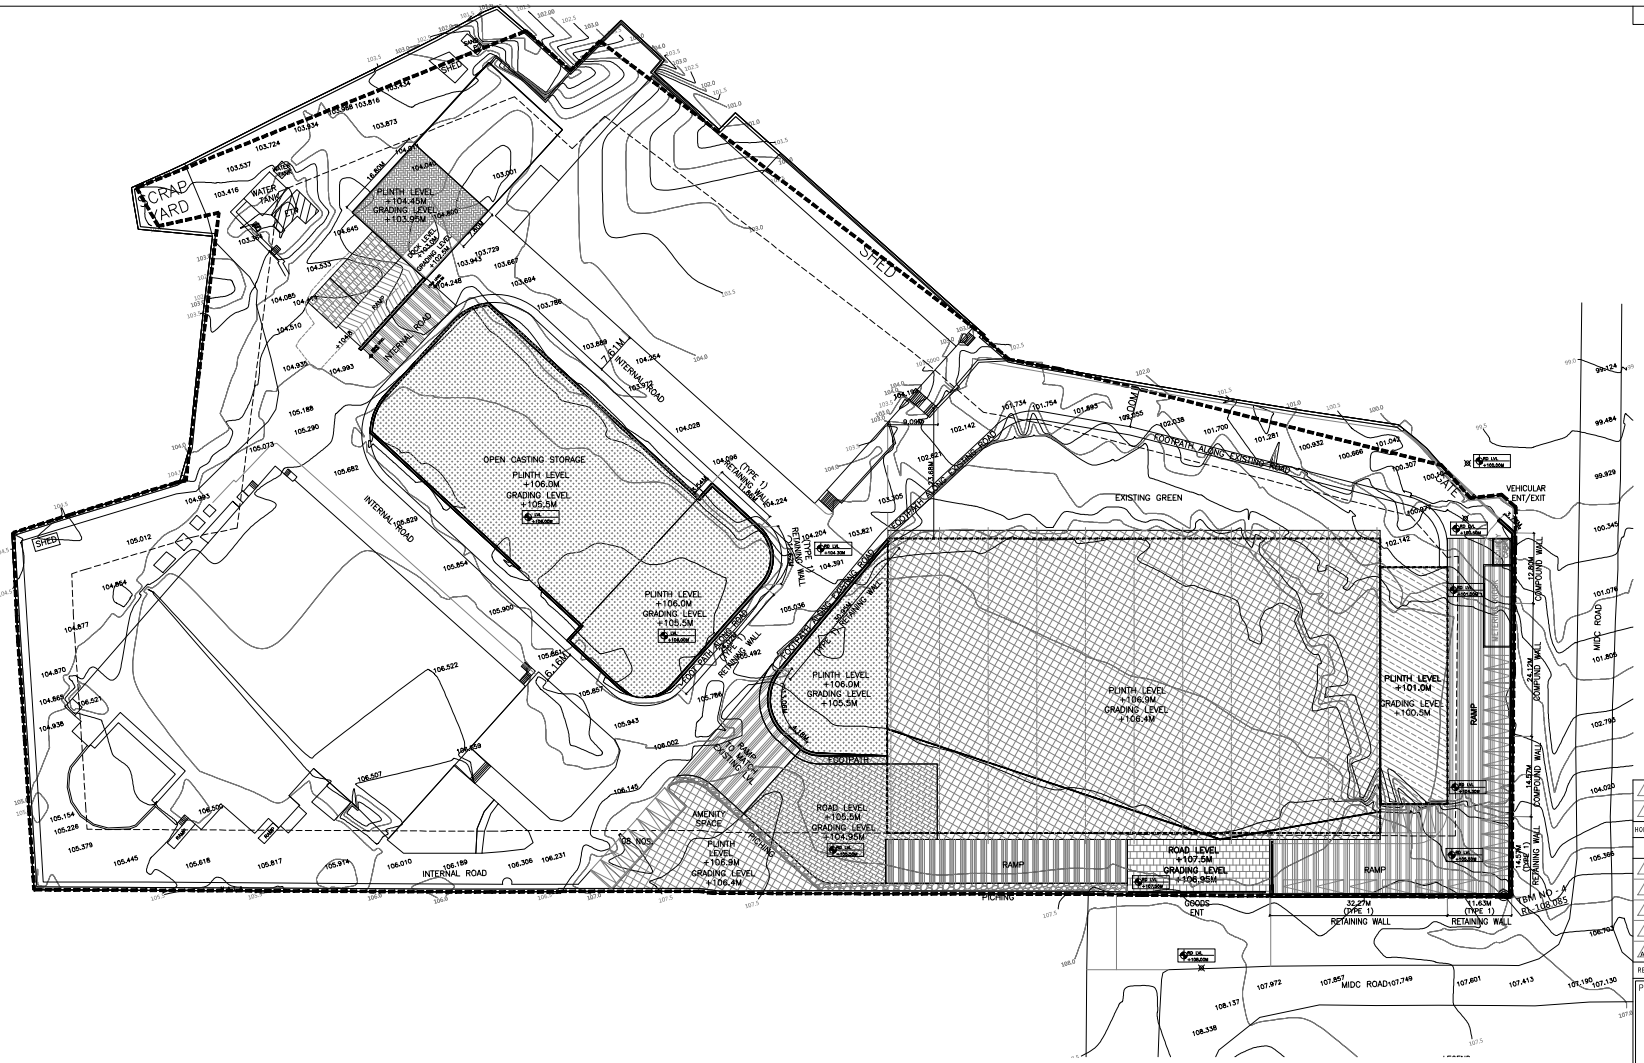

HOLD NO.	DATE	REASON FOR HOLD	SIGNED BY

REV NO.	DATE	DESCRIPTION FOR REVISION	DRAWN BY	CHECKED BY
0	24.09.2020	FOR SCHEMATIC APPROVAL	ALOK	DEEPAK

LEGEND

HATCH INDICATION	PLINTH/ ROAD LEVEL	GRADING LEVEL
	+107.5M	+106.95M
	+106.9M	+106.4M
	+106.0M	+105.5M
	+105.5M	+107.5M
	+104.8	+104.3
	RAMP	

PURPOSE:VA

PROJECT MANAGER
CUSHMAN & WAKEFIELD INDIA PVT LTD

OWNER
M/S CRANE PROCESS FLOW TECHNOLOGIES (I) LTD


PROJECT
CRANE CPE BROWNFIELD EXPANSION - SATARA

TITLE
MASTER PLAN
GRADING PLAN

N

DEALT	JOB NO	REVISION
DEEPAK	281.01.06.20	A0
SCALE 1:200	DATE 24.09.20	DRAWING NO MP-A-1001

Venkataramanan Associates
AN ISO 9001 : 2008
VENUS, 1ST FLOOR, PLOT NO.56, BHARATNAGAR HSG. SOC., PUNE 38

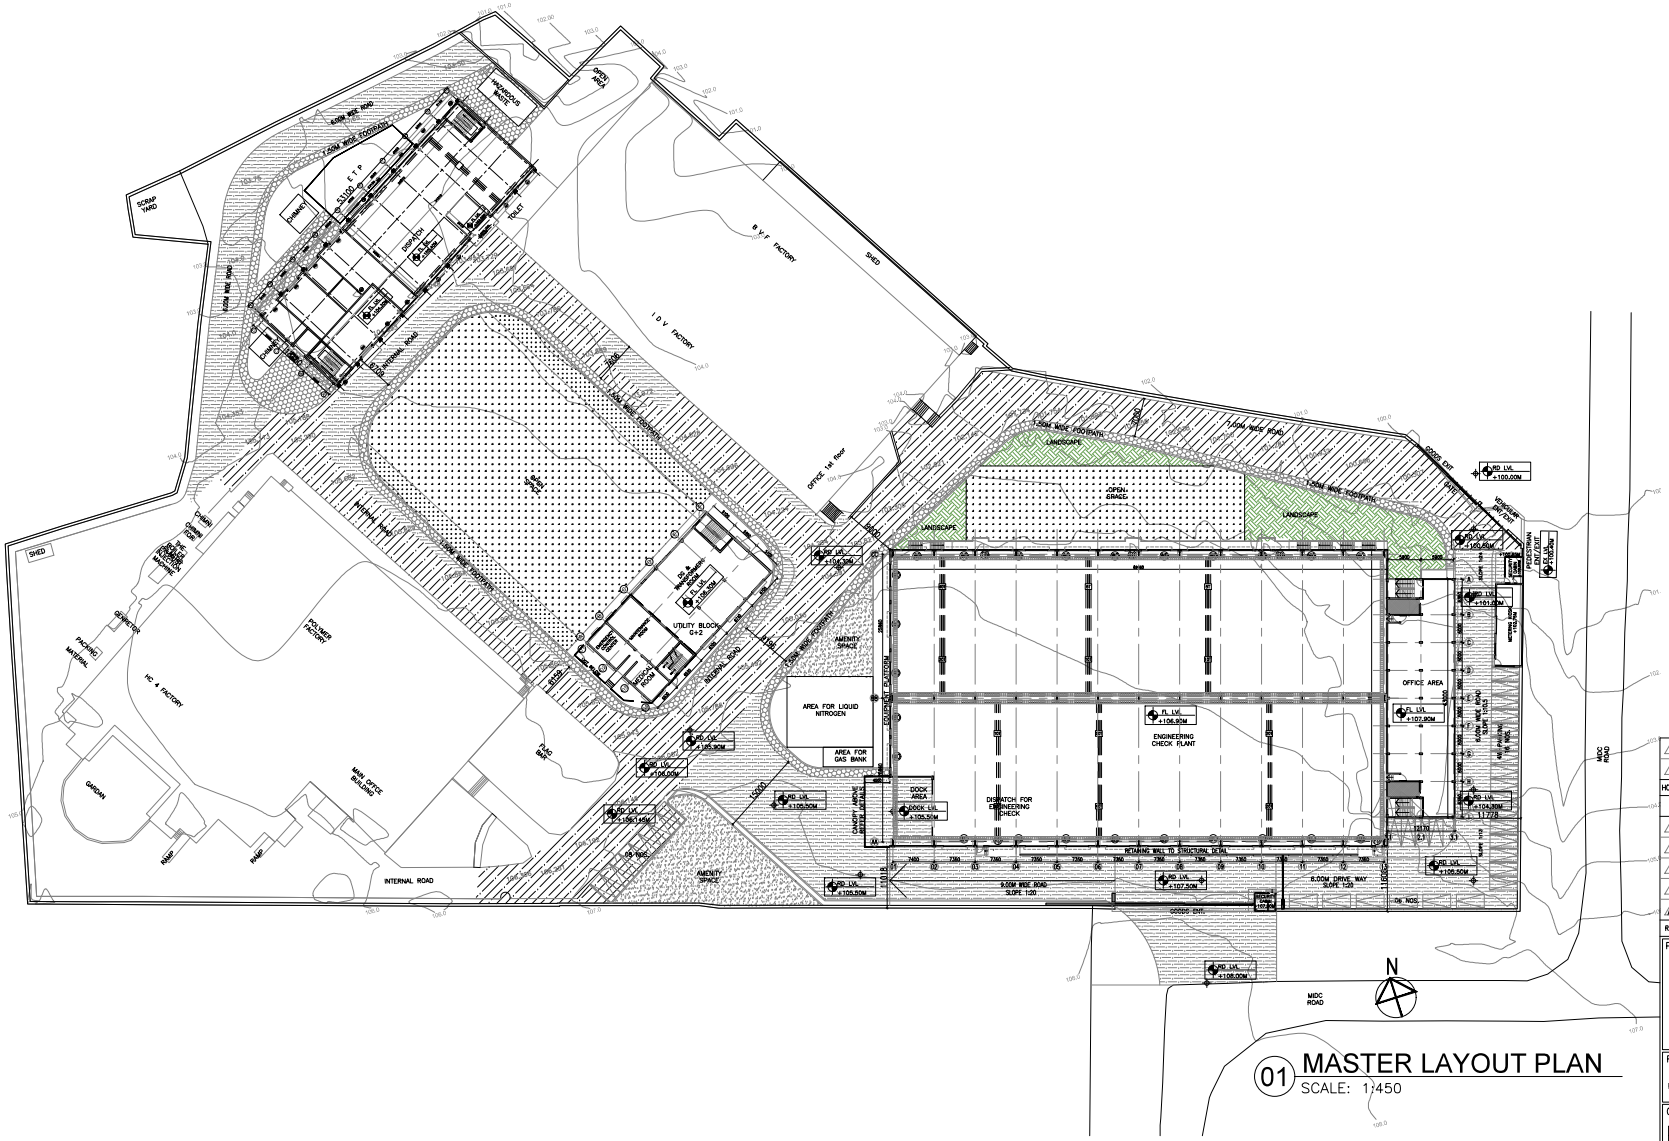

01 MASTER LAYOUT PLAN
SCALE: 1:450

LEGEND	
	EXISTING ROAD AREA
	PROPOSED ROAD AREA
	OPEN SPACE AREA
	LANDSCAPE AREA
	AMENITY SPACE AREA
	1.50M WIDE FOOTPATH

REV.NO.	DATE	DESCRIPTION FOR REVISION	DRAWN BY	CHECKED BY
A0	24.09.2020	FOR SCHEMATIC APPROVAL	SAGAR	DEEPAK

HOLD.NO.	DATE	REASON FOR HOLD	SIGNED BY

PURPOSE:VA

PROJECT MANAGER
CUSHMAN & WAKEFIELD INDIA PVT LTD

OWNER
M/S CRANE PROCESS FLOW TECHNOLOGIES (I) LTD


PROJECT
CRANE CPE BROWNFIELD EXPANSION - SATARA

TITLE
MASTER LAYOUT PLAN

N

DEALT	JOB NO	REVISION
DEEPAK	281.01.08.20	A0
SCALE 1:200	DATE 24.09.20	DRAWING NO MP-A-2001

Venkataramanan Associates
AN ISO 9001:2008 CERTIFIED
VENUS, 1ST FLOOR, PLOT NO.56, BHARATNAGAR HSG. SOC., PUNE 38

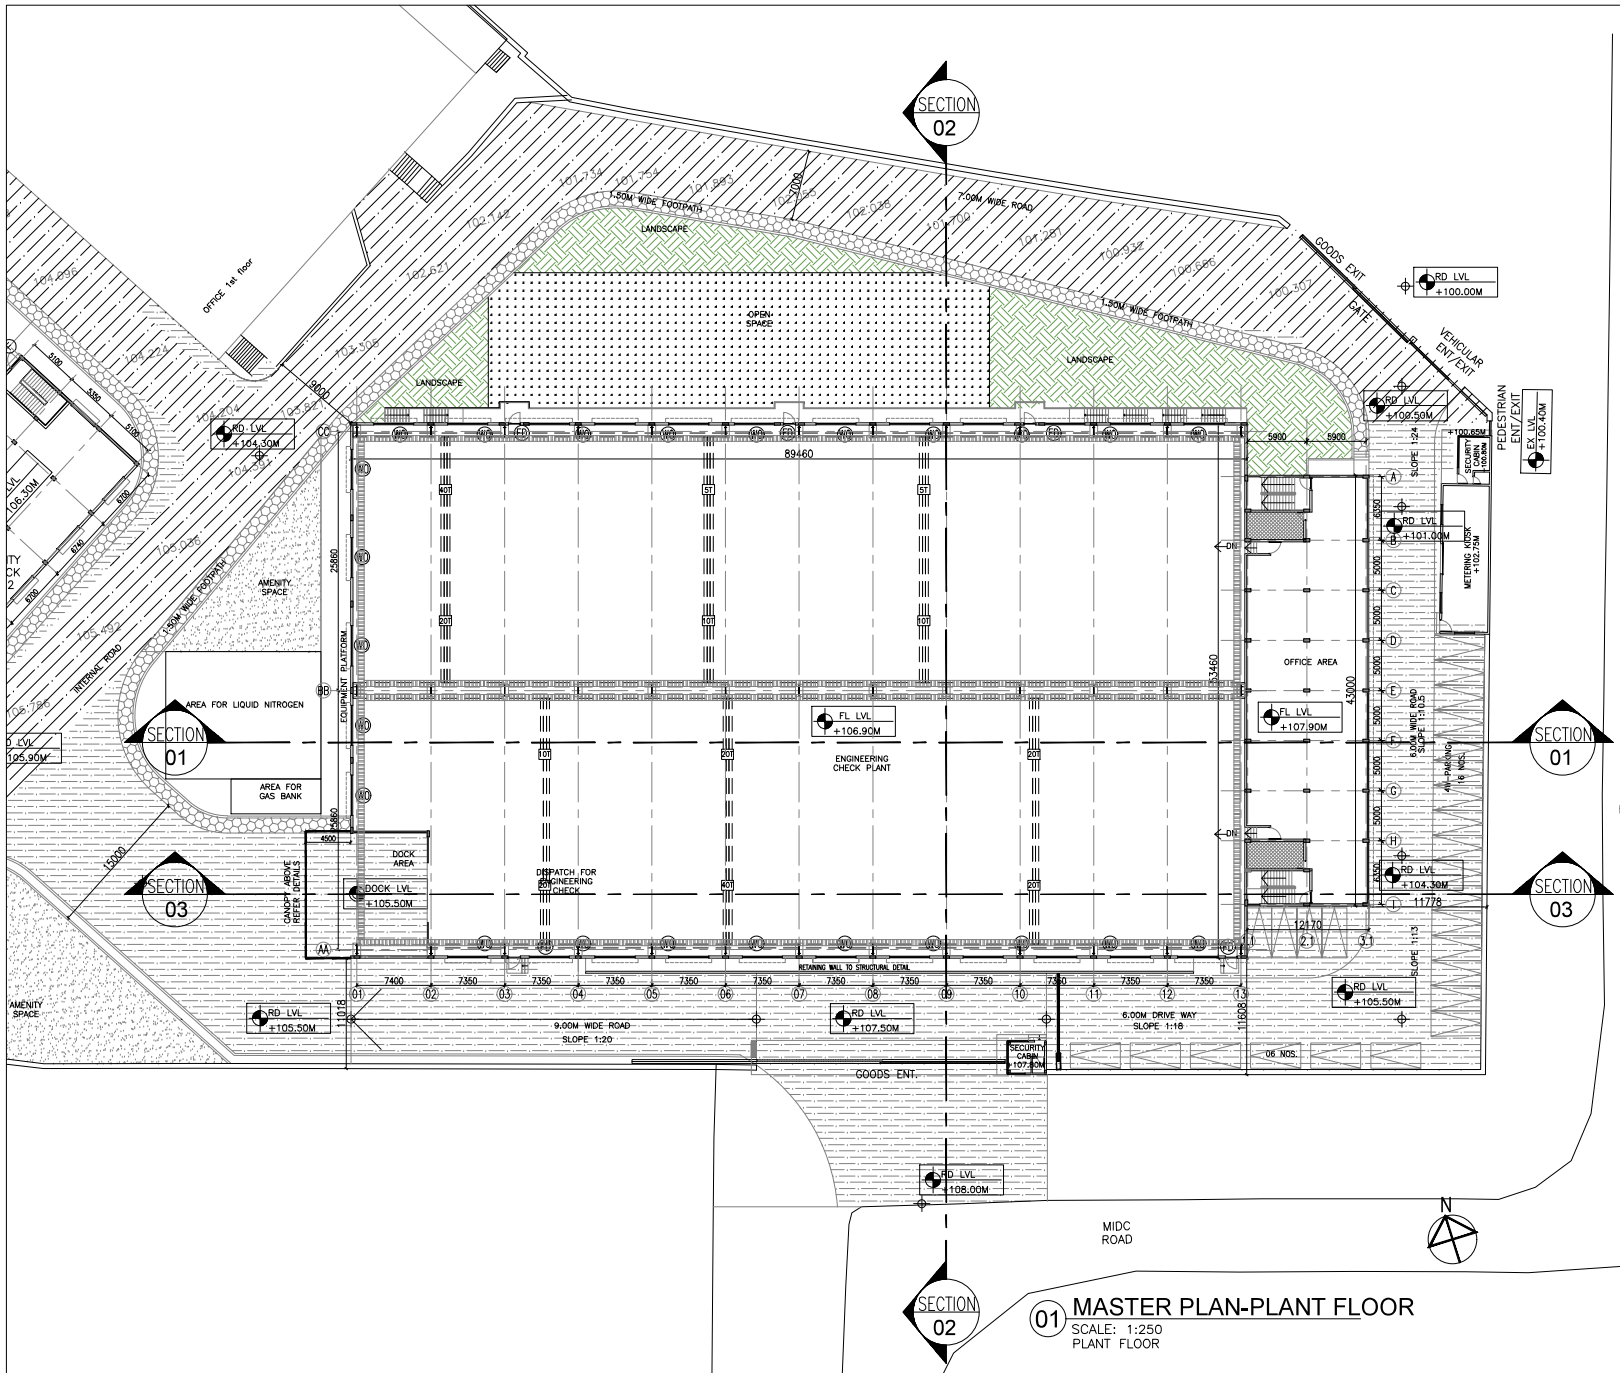

LEGEND

- EXISTING ROAD AREA
- PROPOSED ROAD AREA
- OPEN SPACE AREA
- LANDSCAPE AREA
- AMENITY SPACE AREA
- 1.50M WIDE FOOTPATH

HOLD.NO.	DATE	REASON FOR HOLD	SIGNED BY

NO.	DATE	DESCRIPTION FOR REVISION	DRAWN BY	CHECKED BY
24.09.2020		FOR SCHEMATIC APPROVAL	SAGAR	DEEPAK

PURPOSE:VA

PROJECT MANAGER
CUSHMAN & WAKEFIELD INDIA PVT LTD

OWNER
M/S CRANE PROCESS FLOW TECHNOLOGIES (I) LTD

PROJECT
CRANE CPE BROWNFIELD EXPANSION - SATARA


TITLE
MASTER PLAN LAYOUT
ENGINEERING CHECK PLANT

DEALT	JOB NO	REVISION
DEEPAK	281.01.08.20	A0
SCALE 1:200	DATE 24.09.20	DRAWING NO MP-A-2002


Venkataramanan Associates
AN ISO 9001:2008 CERTIFIED
VISHWAS, 1ST FLOOR, PLOT NO.56, BHARATNAGAR HSG. SOC., PUNE 38

01 MASTER PLAN-PLANT FLOOR

SCALE: 1:250
PLANT FLOOR

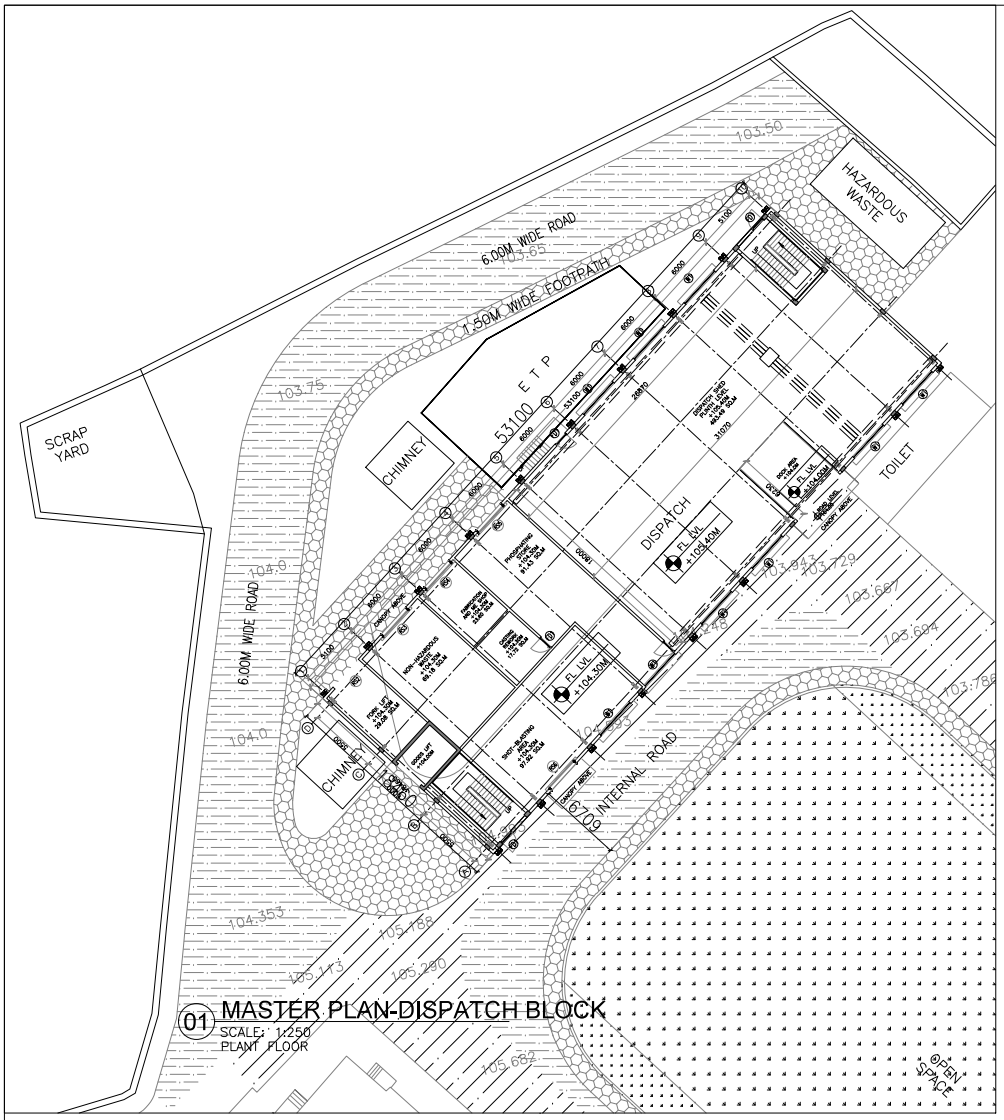

01 MASTER PLAN-DISPATCH BLOCK
SCALE: 1:250
PLANT FLOOR

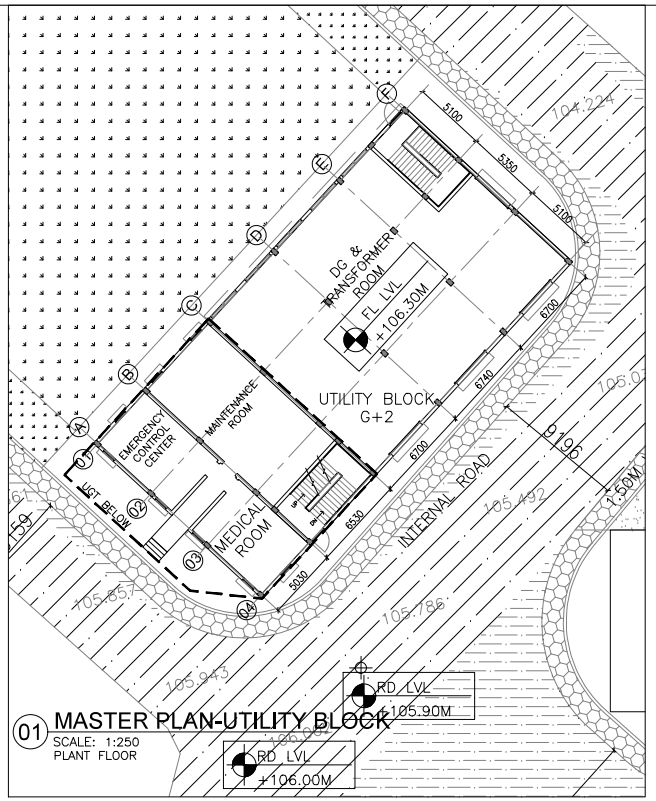

01 MASTER PLAN-UTILITY BLOCK
SCALE: 1:250
PLANT FLOOR

LEGEND

	EXISTING ROAD AREA
	PROPOSED ROAD AREA
	OPEN SPACE AREA
	LANDSCAPE AREA
	AMENITY SPACE AREA
	1.50M WIDE FOOTPATH

HOLD.NO.	DATE	REASON FOR HOLD	SIGNED BY

REV.NO.	DATE	DESCRIPTION FOR REVISION	DRAWN BY	CHECKED BY
A0	24.09.2020	FOR SCHEMATIC APPROVAL	SAGAR	DEEPAK

PURPOSE:VA

PROJECT MANAGER
CUSHMAN & WAKEFIELD INDIA PVT LTD

OWNER
M/S CRANE PROCESS FLOW TECHNOLOGIES (I) LTD


PROJECT
CRANE CPE BROWNFIELD EXPANSION - SATARA

TITLE
MASTER PLAN LAYOUT
DISPATCH & UTILITY BLOCK


N

DEALT	JOB NO		REVISION
DEEPAK	281.01.08.20		A0
SCALE 1:200	DATE 24.09.20	DRAWING NO MP-A-2003	


Venkataramanan Associates
AB SITE TO G + U DAS SINGH
VISHVA, 1ST FLOOR, PLOT NO.56, BHARATNAJ HSG. SOC., PUNE 38

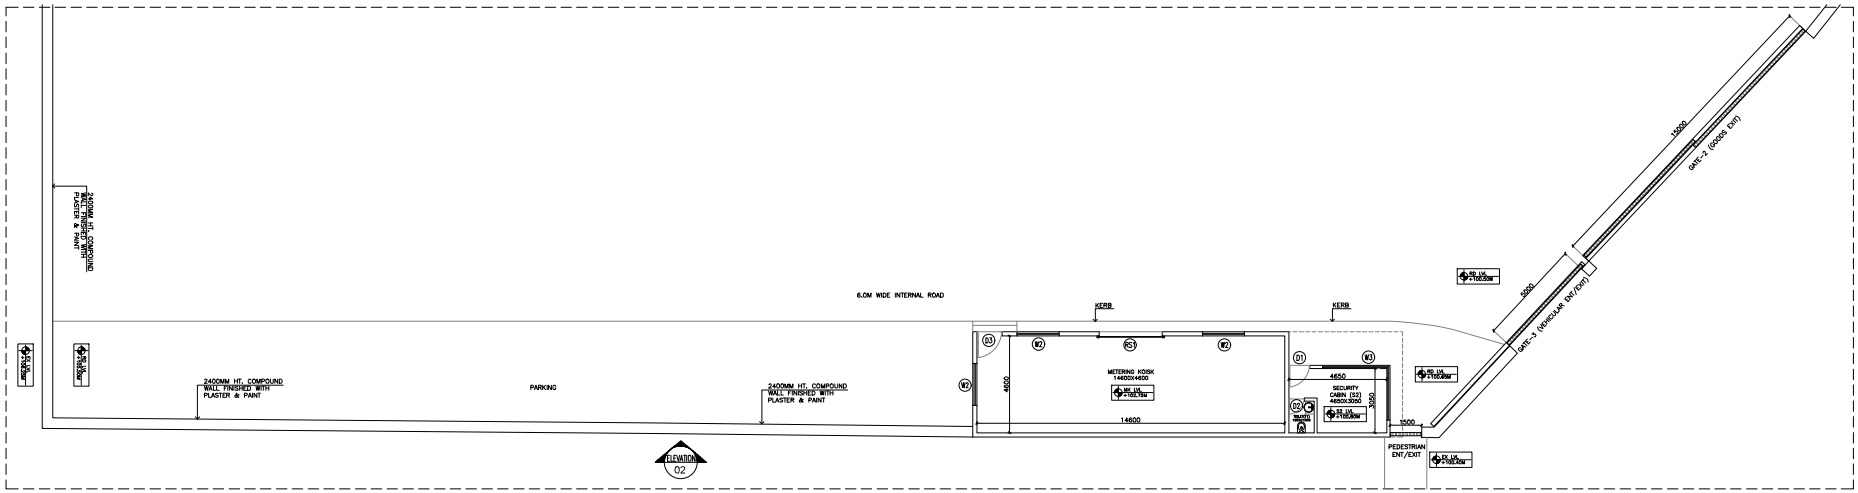


02 GATE -2, GATE - 3, SECURITY CABIN - S2 AND METERING KOISK PLAN
SCALE: 1:125

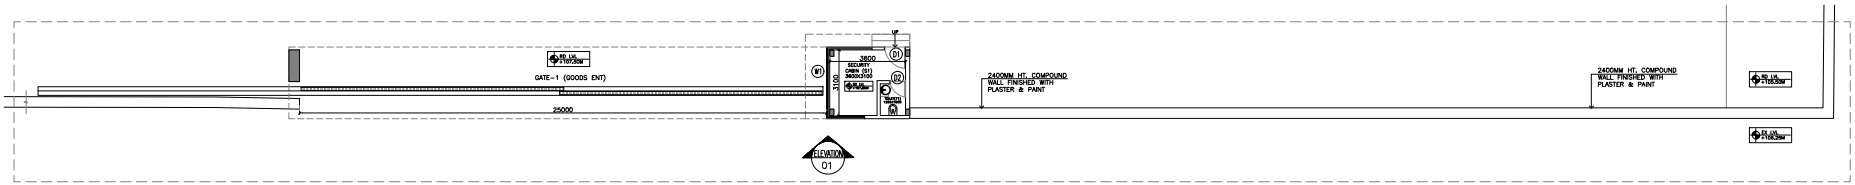

01 GATE -1 AND SECURITY CABIN - S1 PLAN
SCALE: 1:125

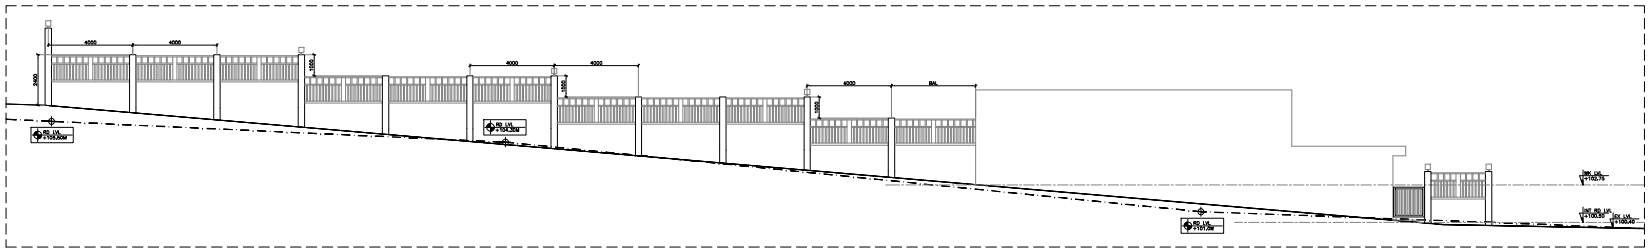

04 ELEVATION - 02
SCALE: 1:125

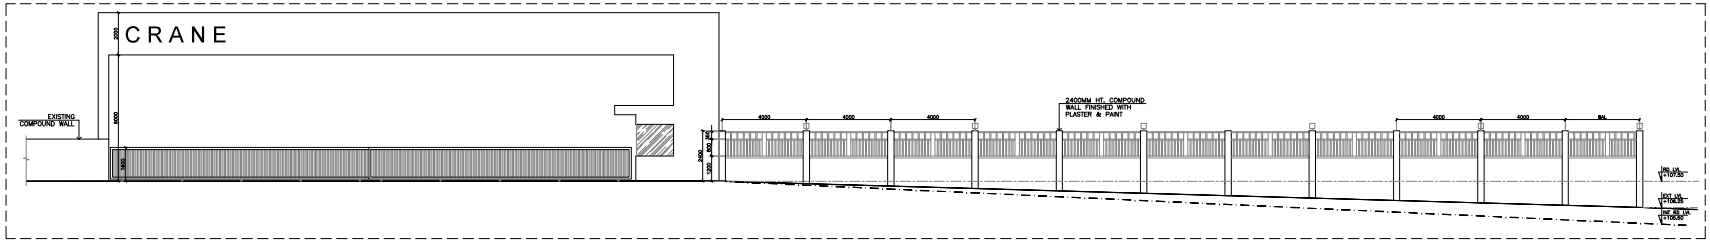

03 ELEVATION - 01
SCALE: 1:125

HOLD.NO.	DATE	REASON FOR HOLD	SIGNED BY

NO.	18.09.2020	FOR SCHEMATIC APPROVAL	PRATIK	DEEPAK
REV.NO.	DATE	DESCRIPTION FOR REVISION	DRAWN BY	CHECKED BY

PURPOSE:VA


PROJECT MANAGER
CUSHMAN & WAKEFIELD INDIA PVT LTD

OWNER
M/S CRANE PROCESS FLOW TECHNOLOGIES (I) LTD

PROJECT
CRANE CPE BROWNFIELD EXPANSION - SATARA

TITLE
ENTRANCE AND SECURITY CABINS

DEALT	JOB NO	REVISION
DEEPAK	281.01.08.20	A0
SCALE 1:125	DATE 23.09.20	DRAWING NO MP-A-3001

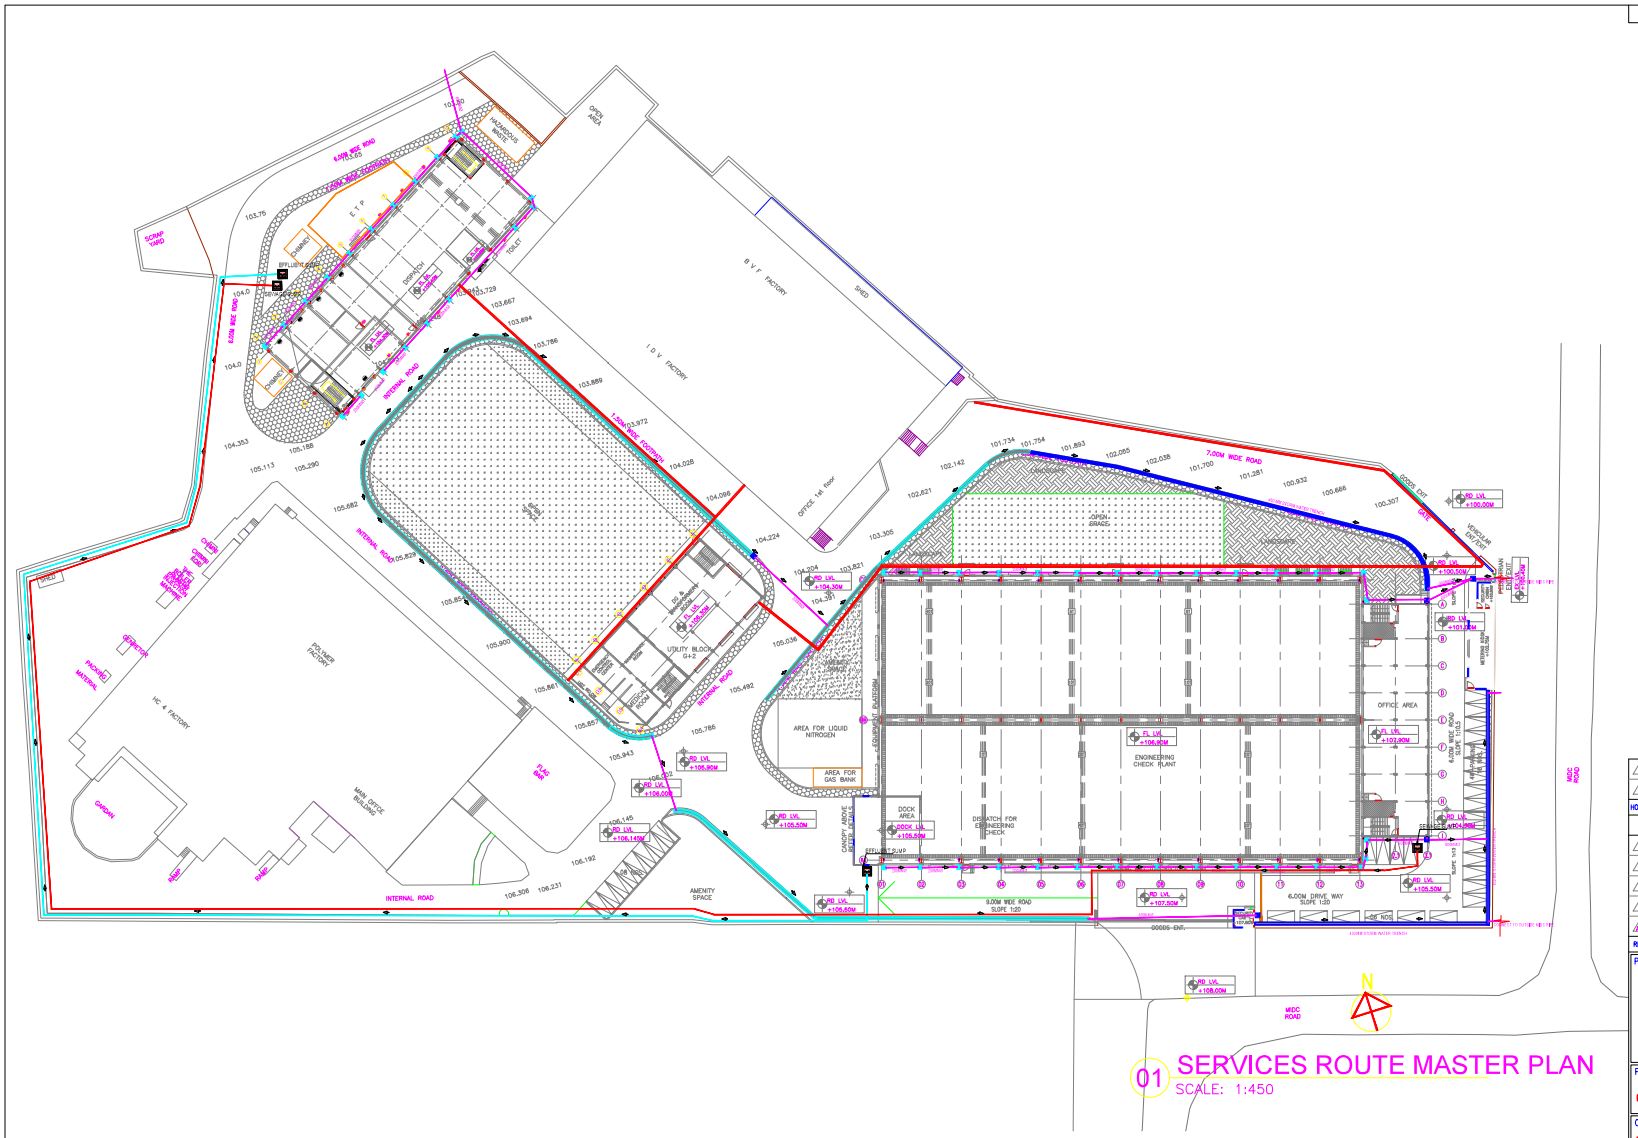

01 SERVICES ROUTE MASTER PLAN
SCALE: 1:450

SEWAGE LEGEND

SEWAGE FLOW DIRECTION SHOWN AS	
150MM DIA RPVC/ PVC EXTERNAL SEWAGE PIPE SHOWN AS	
ASTM SCH 80 uPVC SEWAGE PUMPING LINE SHOWN AS	
300 X 300M P/C GULLY TRAP WITH CHAMBER COVER SHOWN AS	
UNDERGROUND INSTALLATION READYMADE GI & GREASE TRAP OF HDPE MOC (TUPE CAPACITY) SHOWN AS SHAVE AS PER APPROVED MAKE (IET)	
RECTANGULAR INSPECTION CHAMBER FOR DEPTH UPTO 1M, IN MASONARY WITH RCM DOUBLE SEAL RCC HEAVY DUTY COVER SHOWN AS	
600mmD TOP CIRCULAR MANHOLE FOR DEPTH ABOVE 1M, WITH PLAIN DOUBLE WATER SEAL RCC HEAVY DUTY COVER SHOWN AS	
ASTM SCH 80 uPVC SEWAGE PUMPING LINE FOR EFFLUENT	
UTILITY TRENCH SHOWN AS	

LEGEND FOR STORM

450X450MM STORM WATER CAMBER	
900 X 900MM STORM WATER CHAMBER WITH MEDIUM DUTY FRP COVER SHOWN AS (FROM 0.75 M TO 1.5 M DEPTH)	
NP 2CLASS RCC HUME PIPE FOR STORM WATER PIPE	
STORM WATER DOWNTAKE PVC PIPES 6 kg/cm2 grade	
ROAD SIDE SCUPPER	
ROAD SIDE GULLY	
100MM DIA PVC PIPE FROM GULLY TRAP TO CHAMBER	
300 MM WIDE RCC STORM WATER TRENCH WITH HEAVY DUTY PERFORATED COVERS	
450 MM WIDE RCC STORM WATER TRENCH WITH HEAVY DUTY PERFORATED COVERS	
STORM WATER MANHOLE WITH FRP COVER SHOWN AS (FROM 1.5M & ABOVE DEPTH)	

HOLD.NO.	DATE	REASON FOR HOLD	SIGNED BY

REV.NO.	DATE	DESCRIPTION FOR REVISION	DRAWN BY	CHECKED BY
01	30.09.2020	FOR SCHEMATIC APPROVAL	SAGAR	DEEPAK

PURPOSE:VA

PROJECT MANAGER
CUSHMAN & WAKEFIELD INDIA PVT LTD


OWNER
CRANE — M/S CRANE PROCESS FLOW TECHNOLOGIES (I) LTD

PROJECT
CRANE CPE BROWNFIELD EXPANSION - SATARA


TITLE
MASTER LAYOUT PLAN
SERVICES ROUTING PLAN

DEALT	JOB NO	REVISION
DEEPAK	281,01,08,20	A0
SCALE: 1:200	DATE: 30.09.2020	DRAWING NO: MP-SK-2001


Venkataramanan Associates
AN ISO 9001:2008 CERTIFIED
VENUS, 1ST FLOOR, PLOT NO.52, PRAKASHNAGAR HSG. SOC., PUNE 38

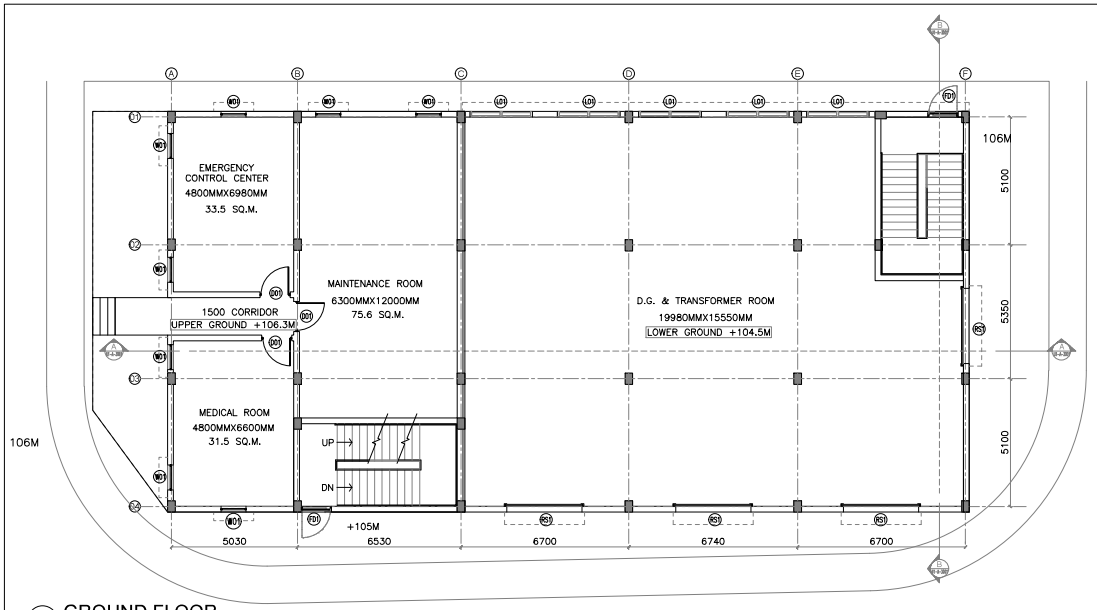

01 GROUND FLOOR
SCALE: 1:100
UTILITY BLOCK

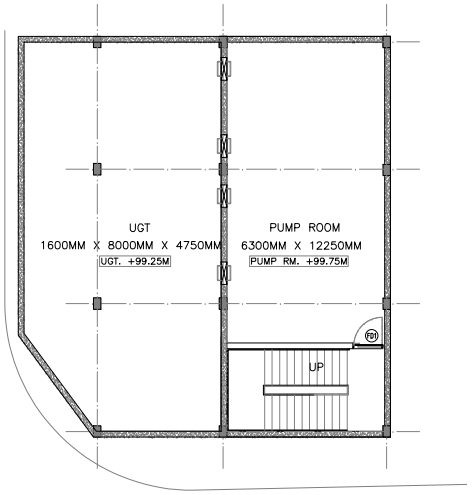

02 U,G,T. LEVEL
SCALE: 1:100
UTILITY BLOCK

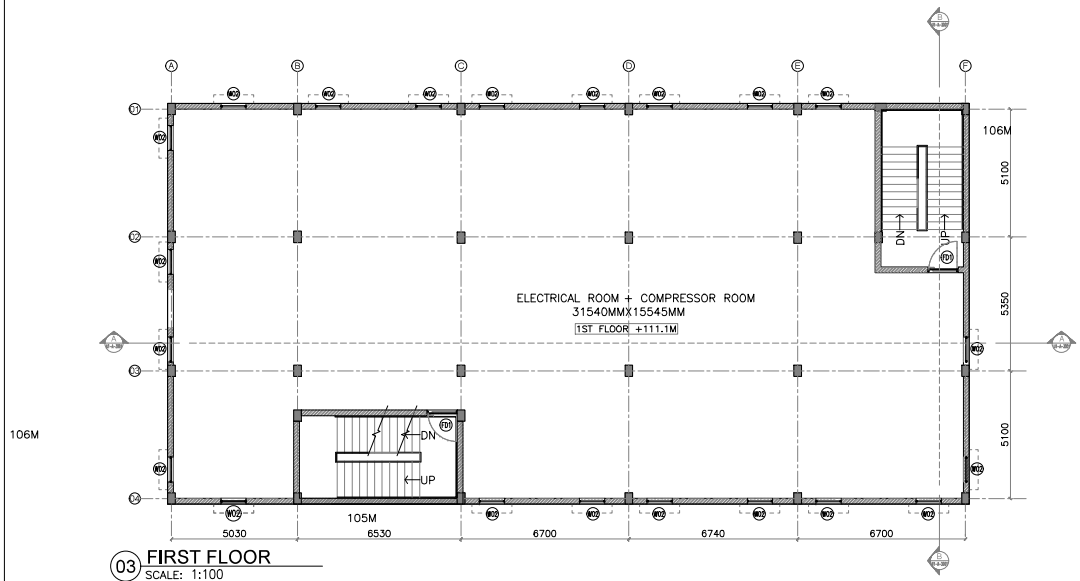

03 FIRST FLOOR
SCALE: 1:100
UTILITY BLOCK

SCHEDULE OF DOORS

S.NO	TYPE	SIZE	SILL	LINTEL FROM FFL	LOCATION
01	FD1	1200 X 2450	–	2250	STAIRCASE
02	D1	1200 X 2450	–	2450	MAINTENANCE ROOM MEDICAL ROOM
03	RS	3000 X 3200	–	3200	D.G AREA

SCHEDULE OF WINDOWS

S.NO	TYPE	SIZE	SILL	LINTEL FROM FFL	LOCATION
01	W1	1000 X 1500	950	2450	MEDICAL ROOM
02	W2	1000 X 2100	350	2450	COMPRESSOR ROOM UPS/RECREATION CENTER
05	L1	2550 X 3100	2900	6000	D.G AREA

ALL DOORS/WINDOWS OPENING IN WALL ARE CONSTRUCTION OPENING.
(i.e. UNPLASTERED SURFACE OF WALL)

HOLD.NO.	DATE	REASON FOR HOLD	SIGNED BY

REV.NO.	DATE	DESCRIPTION FOR REVISION	DRAWN BY	CHECKED BY
A0	24.09.2020	FOR SCHEMATIC APPROVAL	ALOK	DEEPAK

PURPOSE:VA

PROJECT MANAGER
CUSHMAN & WAKEFIELD INDIA PVT LTD

OWNER
M/S CRANE PROCESS FLOW TECHNOLOGIES (I) LTD


PROJECT
CRANE CPE BROWNFIELD EXPANSION - SATARA

TITLE
UTILITY BLOCK
UGT, GROUND & FIRST FLOOR LVL


N

DEALT	JOB NO	REVISION
DEEPAK	281.01.08.20	A0
SCALE: 1:200	DATE: 24.09.20	DRAWING NO: U1-A-2001


Venkataramanan Associates
AN ISO 9001:2008 CERTIFIED
"VISHNU", 1ST FLOOR, PLOT NO.56, BHARATNAGAR HSG. SOC., PUNE 38

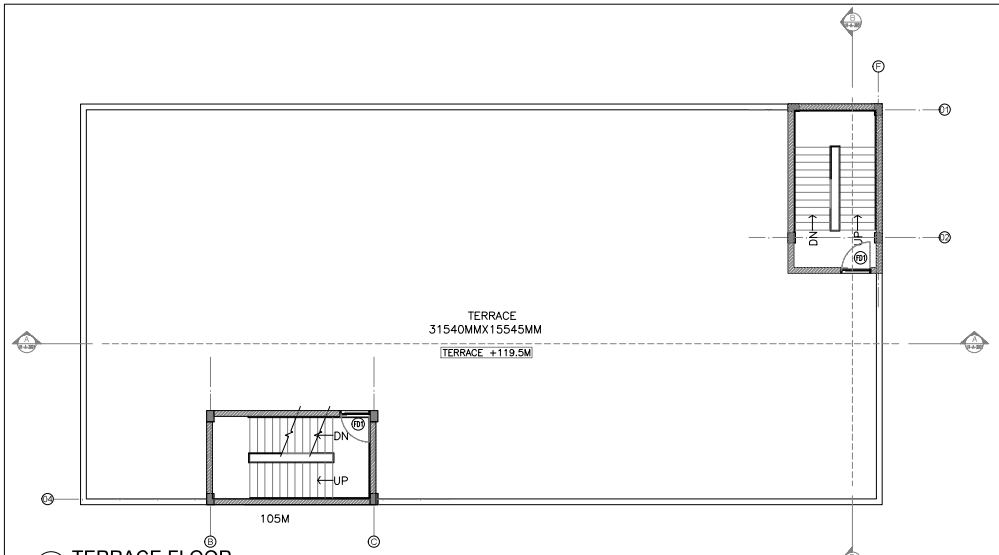

01 TERRACE FLOOR
SCALE: 1:100
UTILITY BLOCK

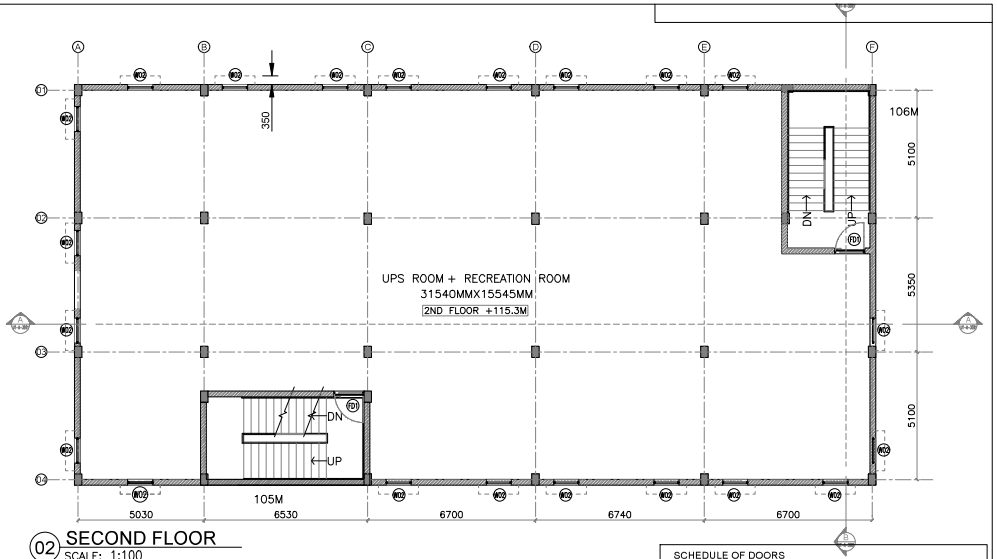

02 SECOND FLOOR
SCALE: 1:100
UTILITY BLOCK

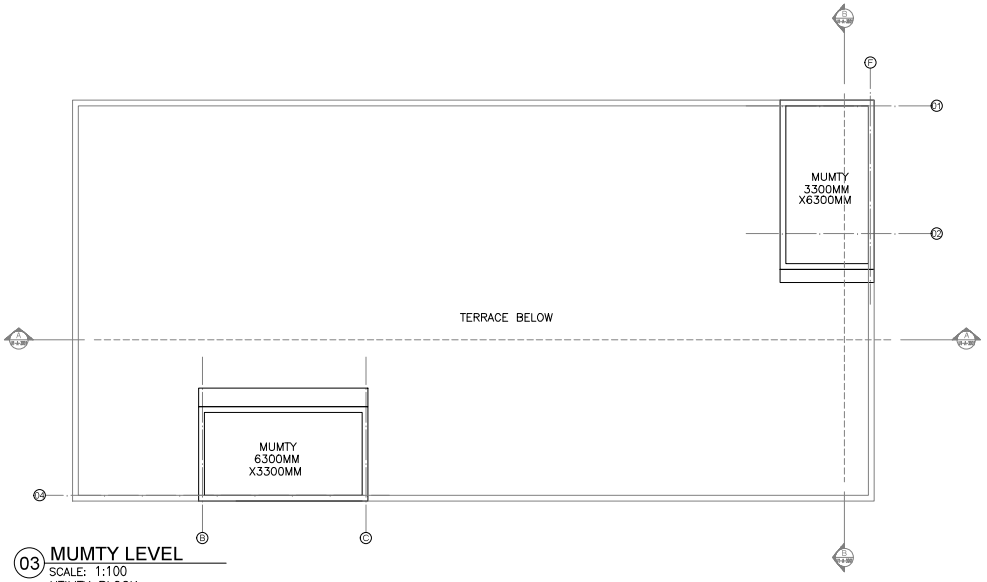

03 MUMTY LEVEL
SCALE: 1:100
UTILITY BLOCK

SCHEDULE OF DOORS

S.NO	TYPE	SIZE	SILL	LINTEL FROM FFL	LOCATION
01	FD1	1200 X 2450	–	2250	STAIRCASE
02	D1	1200 X 2450	–	2450	MAINTENANCE ROOM MEDICAL ROOM
03	RS	3000 X 3200	–	3200	D.G AREA

SCHEDULE OF WINDOWS

S.NO	TYPE	SIZE	SILL	LINTEL FROM FFL	LOCATION
01	W1	1000 X 1500	950	2450	MEDICAL ROOM
02	W2	1000 X 2100	350	2450	COMPRESSOR ROOM UPS/RECREATION CENTER
05	L1	2550 X 3100	2900	6000	D.G AREA

ALL DOORS/WINDOWS OPENING IN WALL ARE CONSTRUCTION OPENING.
(i.e. UNPLASTERED SURFACE OF WALL)

HOLD.NO.	DATE	REASON FOR HOLD	SIGNED BY

REV.NO.	DATE	DESCRIPTION FOR REVISION	DRAWN BY	CHECKED BY
A0	24.09.2020	FOR SCHEMATIC APPROVAL	ALOK	DEEPAK

PURPOSE:VA

PROJECT MANAGER
CUSHMAN & WAKEFIELD INDIA PVT LTD


OWNER
M/S CRANE PROCESS FLOW TECHNOLOGIES (I) LTD

PROJECT
CRANE CPE BROWNFIELD EXPANSION - SATARA


TITLE
UTILITY BLOCK
SECOND & TERRACE FLOOR LVL

DEALT	JOB NO		REVISION
DEEPAK	281.01.08.20		A0
SCALE 1:200	DATE 24.09.20	DRAWING NO U1-A-2002	


Venkataramanan Associates
AN ISO 9001:2008 CERTIFIED FIRM
'VENUS', 1ST FLOOR, PLOT NO.56, BHARATNAGAR HSG. SOC., PUNE 38

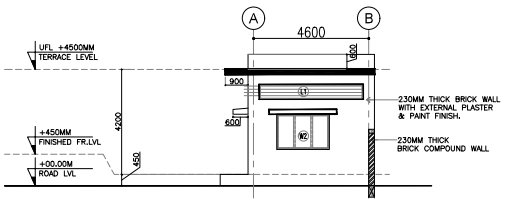


06 SOUTH SIDE ELEVATION
SCALE: 1:100
U9 – METERING KIOSK

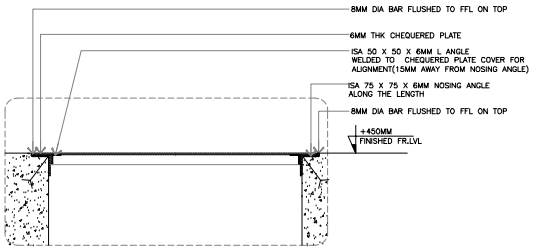


08 TRENCH COVER DETAIL
SCALE: 1:10
U9 – METERING KIOSK

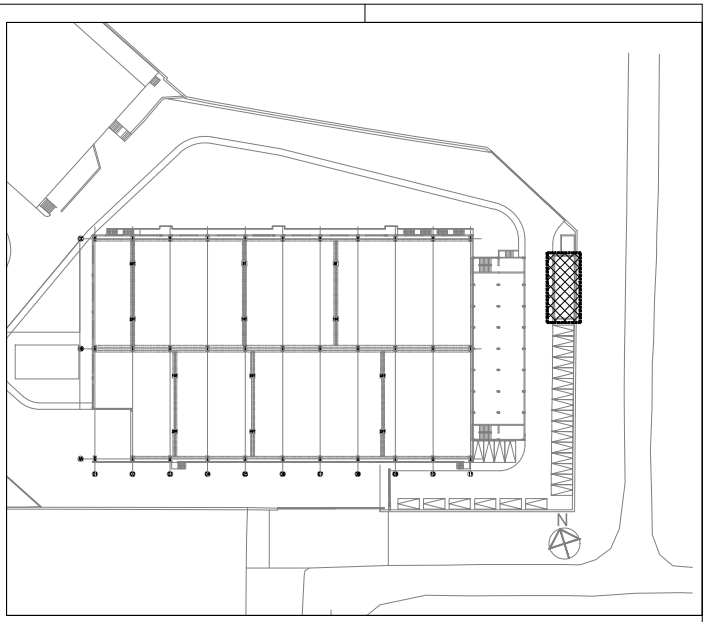


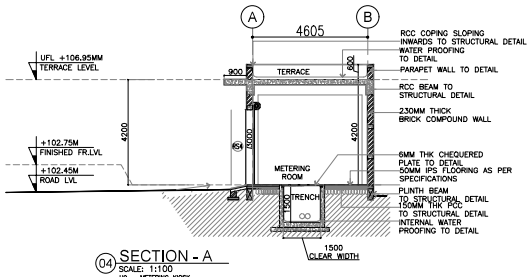


04 SECTION - A
SCALE: 1:100
U9 – METERING KIOSK

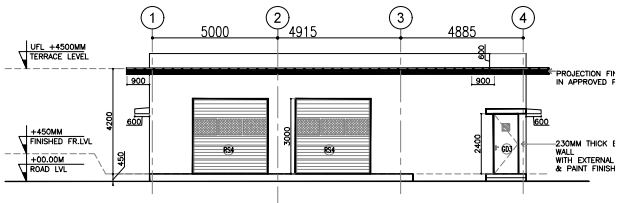

05 WEST SIDE ELEVATION
SCALE: 1:100
U9 – METERING KIOSK

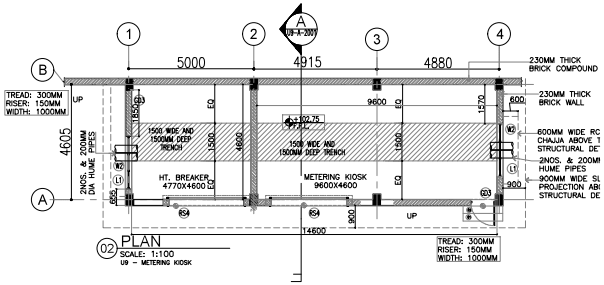

02 PLAN
SCALE: 1:100
U9 – METERING KIOSK

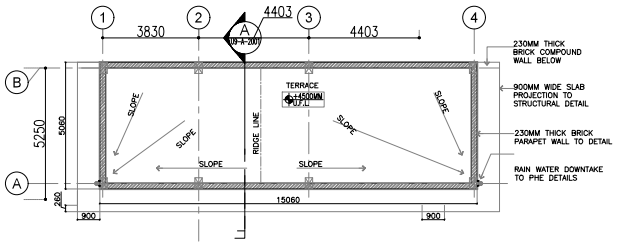

03 TERRACE PLAN
SCALE: 1:100
U9 – METERING KIOSK

LEGEND:

	230MM THICK BRICK WALL
	RCC COLUMN TO STRUCTURAL DETAIL
	TILE DROP
	2 NOS. & 200MM DIA HUME PIPE BOTTOM TO MATCH TRENCH BOTTOM

SCHEDULE OF DOORS & WINDOWS

S.NO	TYPE	SIZE	CILL	LINTEL	LOCATION	DESCRIPTION	QTY
01	GD3	1000 X 2400	FFL	2400	METERING KIOSK	SINGLE LEAF EQUAL SHUTTER – METAL DOOR	02
02	RS4	3000 X 3000	FFL	3000	METERING KIOSK	ROLLING SHUTTER WITH GRILL	02
03	ME	2100 X 1400	1000	2400	METERING KIOSK	ALUMINIUM SLIDING WINDOW	02
04	L1	4800 X 600	3000	3600	METERING KIOSK	ALUMINIUM POWDER COATED FIXED LOUVERS	02

HOLD.NO.	DATE	REASON FOR HOLD	SIGNED BY

NO.	24.09.2020	FOR SCHEMATIC APPROVAL	ALOK	DEEPAK
REV.NO.	DATE	DESCRIPTION FOR REVISION	DRAWN BY	CHECKED BY

PURPOSE:VA

PROJECT MANAGER
CUSHMAN & WAKEFIELD INDIA PVT LTD


OWNER
M/S CRANE PROCESS FLOW TECHNOLOGIES (I) LTD

PROJECT
CRANE CPE BROWNFIELD EXPANSION - SATARA


TITLE
METERING KIOSK

DEALT	JOB NO	REVISION
DEEPAK	281.01.08.20	A0
SCALE: 1:200	DATE: 24.09.20	DRAWING NO: U1-A-2003


Venkataramanan Associates
AN ISO 9001:2008 CERTIFIED
402/403, 1ST FLOOR, PLOT NO.36, BHARATNAGAR HSG. SOC., PUNE 38

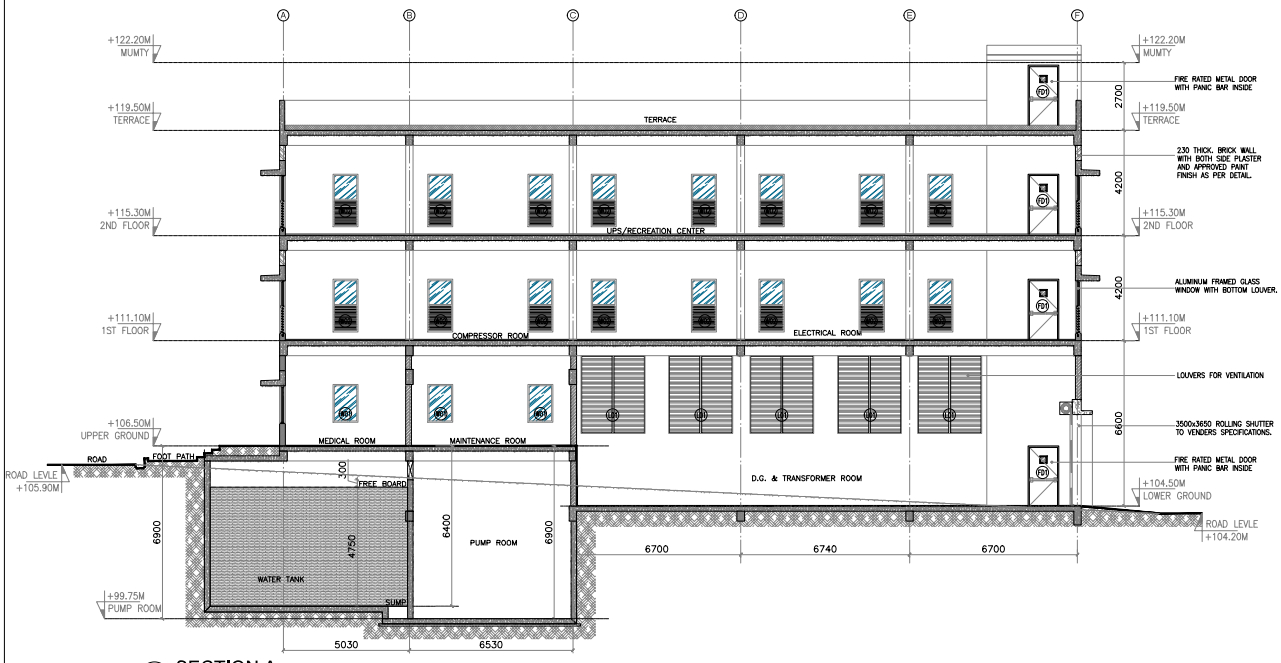

01 SECTION A
SCALE: 1:100
UTILITY BLOCK

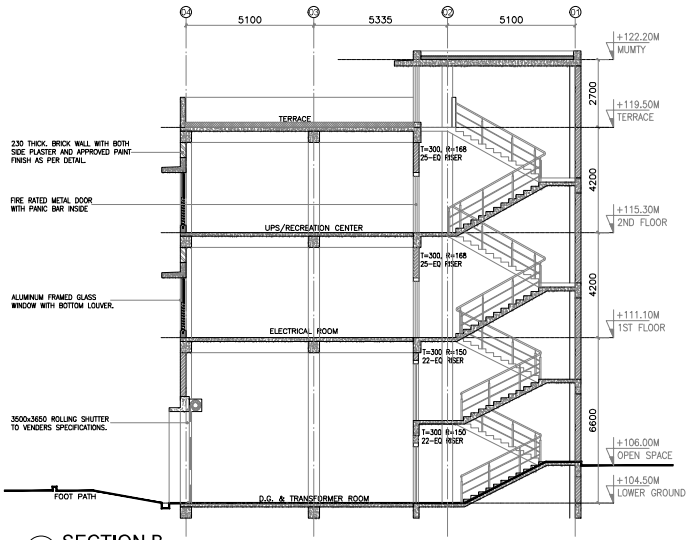

02 SECTION B
SCALE: 1:100
UTILITY BLOCK

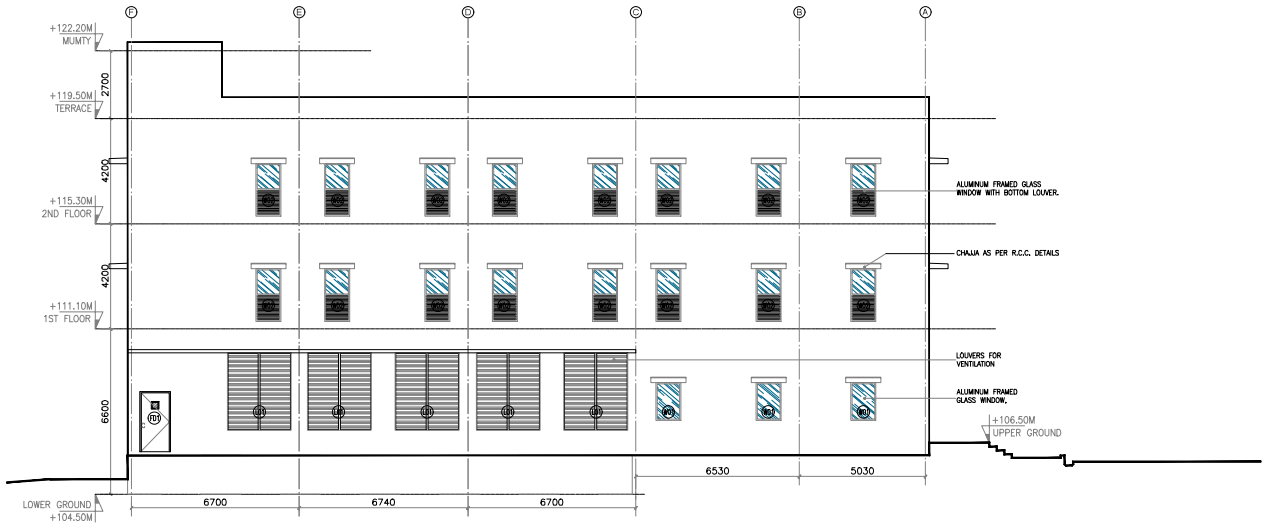

03 ELEVATION F
SCALE: 1:100
UTILITY BLOCK

HOLD.NO.	DATE	REASON FOR HOLD	SIGNED BY

REV.NO.	DATE	DESCRIPTION FOR REVISION	DRAWN BY	CHECKED BY
A0	24.09.2020	FOR SCHEMATIC APPROVAL	ALOK	DEEPAK

PURPOSE:VA

PROJECT MANAGER
CUSHMAN & WAKEFIELD INDIA PVT LTD

OWNER
M/S CRANE PROCESS FLOW TECHNOLOGIES (I) LTD

PROJECT
CRANE CPE BROWNFIELD EXPANSION - SATARA

TITLE
UTILITY BLOCK
ELEVATION & SECTION

DEALT	JOB NO	REVISION
DEEPAK	281.01.08.20	A0
SCALE: 1:200	DATE: 24.09.20	DRAWING NO: U1-A-3001

Venkataramanan Associates
AN ISO 9001:2008 CERTIFIED
VENUS, 1ST FLOOR, PLOT NO.56, BHARATNAGAR HSG. SOC., PUNE 38