TOP FRAME STIFFENING DETAILS

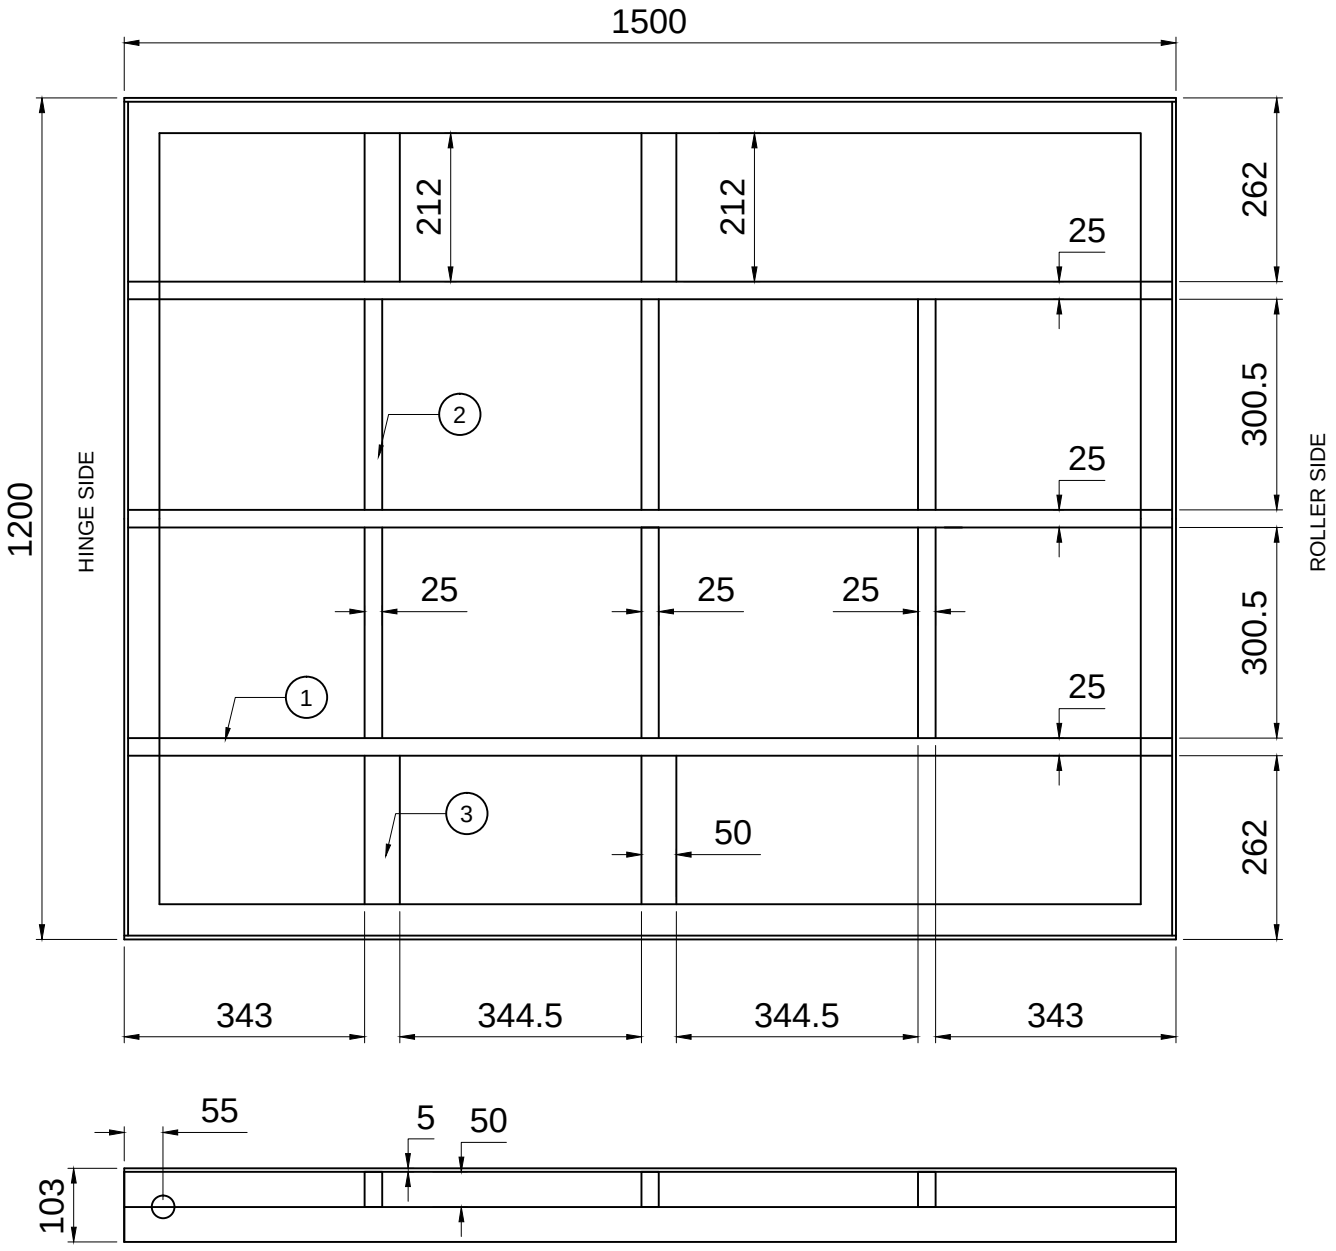

3.	FLAT 50 X 5 X 212L	4NOS
2.	R.TUBE 50 X 25 X 3 THK X 300L	6NOS
1.	R.TUBE 50 X 25 X 3 THK X 1488L	3NOS
SR.NO	DESCRIPTION	QTY.

This drawing & design is the property of NIHVA TECHNOLOGIES. Not to be sold or copied to any other concern.

TITLE : -
TOP FRAME STIFFENINIG

NIHVA TECHNOLOGIES PVT. LTD.

NIHVA TECHNOLOGIES PVT. LTD. PUNE
Tel : 020 66304033
Email:- info@nihva.com
Website:- www.nihva.com

	SIGN	DATE
DRAWN	P.A	04.10.18
CHECK	R.D	04.10.18
REV.		
APPROVAL		

If any queries contact : projects@nihva.com

ALL DIMENSION ARE IN mm

CLIENT -

PROJECT -

SITE -

DWG. NO. : NIHVA/18-19/MFG/NSL/1018/003

SCALE: NTS | WT: | SHEET: 01 OF 01