


PRODUCED BY AN AUTODESK EDUCATIONAL PRODUCT

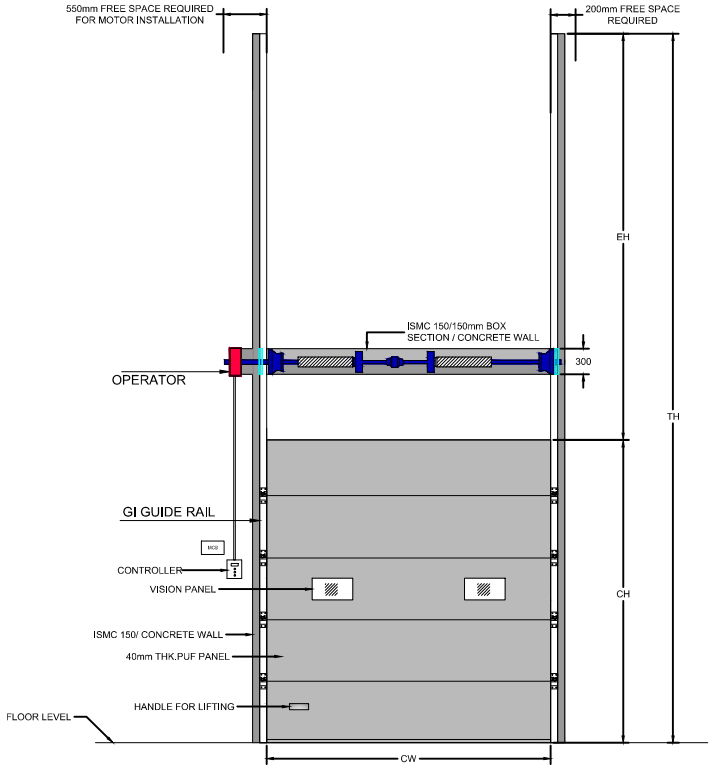


INSIDE VIEW

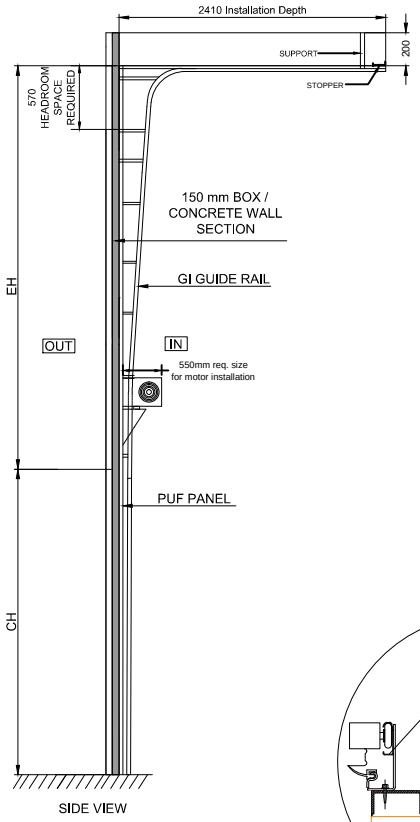

SIDE VIEW

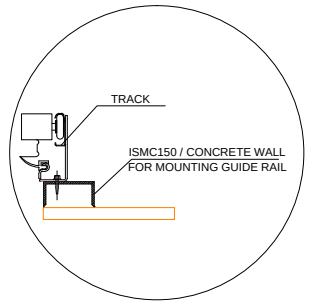

GUIDE DETAIL

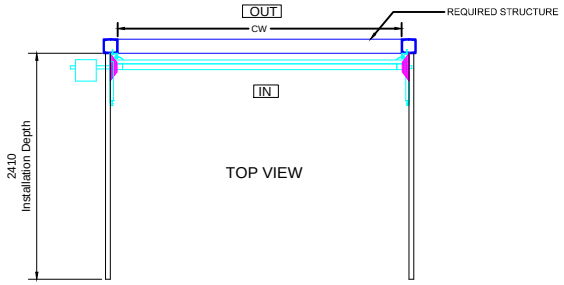

TOP VIEW

R01	SURAJ		1).HEIGHT CHANGED. 2).GUIDE DETAIL ADDED.
REV NO	DRAWN	SIGN	DESCRIPTION

SR NO	CLEAR WIDTH	CLEAR HEIGHT	QTY	TH	EH
01	4000mm	4000mm	1	6900	2700

TOLERANCE: ±10mm

This drawing & design is the property of NIHVA TECHNOLOGIES. Not to be sold or copied to any other concern.

TITLE: SECTIONAL DOOR (HL)

NIHVA TECHNOLOGIES PVT. LTD. PUNE
Tel : 020 66304033
Website:- www.nihva.com Email:- info@nihva.com

	NAME	SIGN	DATE
DRAWN	SURAJ		16/07/17
CHECK	VIKRANT		16/07/17
APPROVAL	R.D		16/07/17

CLIENT -PROJECTSPOOL ENGG. SERVICE PVT. LTD.
PROJECT -
SITE - PUNE.
If any queries contact : design@nihva.com
DWG. NO. : NIHVA/18-19/0088/R01 REV: 0
ALL DIMENSION ARE IN mm
SCALE: NTS WT: SHEET: 01 OF 01

PRODUCED BY AN AUTODESK EDUCATIONAL PRODUCT
PRODUCED BY AN AUTODESK EDUCATIONAL PRODUCT
PRODUCED BY AN AUTODESK EDUCATIONAL PRODUCT