

TECHNICAL SPECS FOR SWING GATE		
SL NO.	SPECIFICATION	
1	OPENING LENGTH	3800MM
2	OPENING HEIGHT	1500MM
3	OUTER TUBE	100X100X4
4	INNER TUBE	32X32X2.6
5	OPERATION	MANUAL

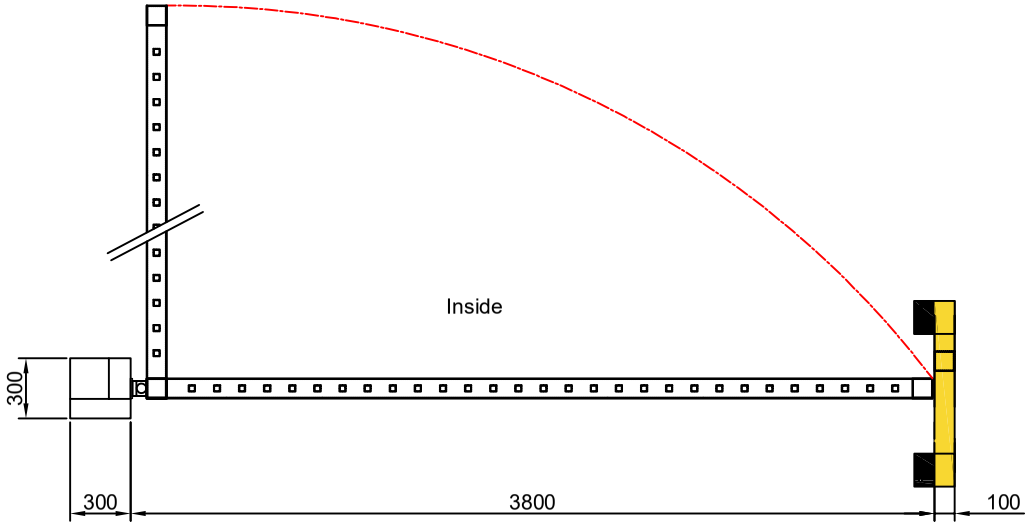

Note:-

1. All dimension are in mm.
2. All civil work is in client scope.
3. Swing gate size will be 3800x1500mm
   (200mm Space required for supporting structure)

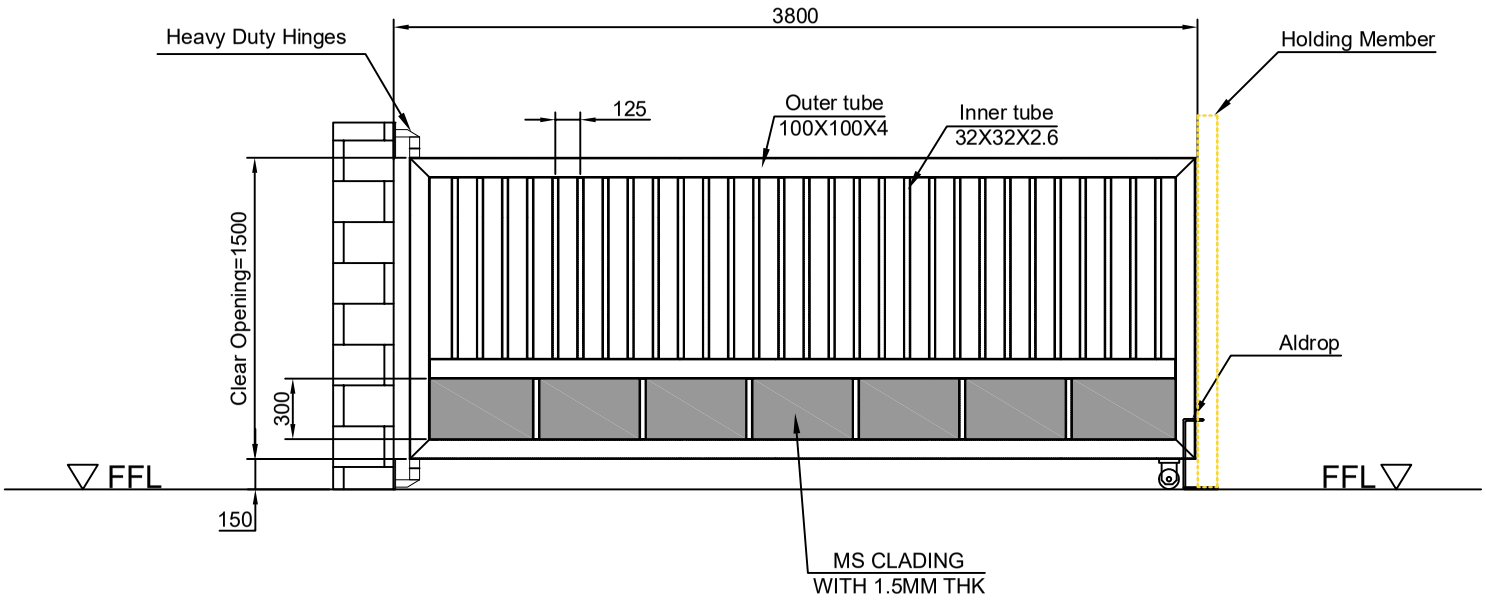

This drawing & design is the property of NIHVA TECHNOLOGIES. Not to be sold or copied to any other concern.

TITLE:- SWING GATE

NIHVA TECHNOLOGIES PVT. LTD.
NIHVA TECHNOLOGIES PVT. LTD. PUNE
Tel : 020 66304033
Email:- info@nihva.com
Website:- www.nihva.com

	NAME	DATE	SIGN
DRAWN	SUJATA.B	03/01/2022	
CHECK	G.PATIL	03/01/2022	
APPRD.	A.K	03/01/2022	

CLIENT - Fanidhar Mega Food Park Private Limited
LOCATION - GUJARAT
PRODUCT - SWING GATE
If any queries contact : design@nihva.com
DWG NO:-NIHVA/21-22/CLT/0296 REV- 0
ALL DIMENSION ARE IN mm
SCALE: NTS SCALE:-- 1:1 SHEET: 01 OF 01

Rev No.	Revision	Date	Revised By
1.	Clear Height of the gate changed 1800mm to 1500mm	08/01/2022	Sujata
2.	Aldrop and Holding Member for the to be added.	08/01/2022	Sujata