

STRUCTURE MOUNTED DOUBLE WALL ROLLING SHUTTER FITTED FROM OUTSIDE

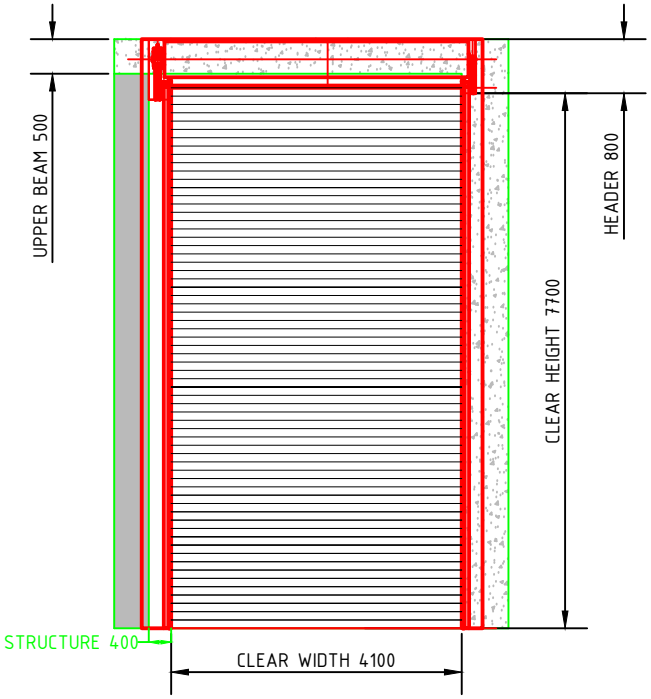


REQUIRED CLEAR SIZE 4515 X 8000
ACTUAL CLEAR SIZE 4100 X 7700

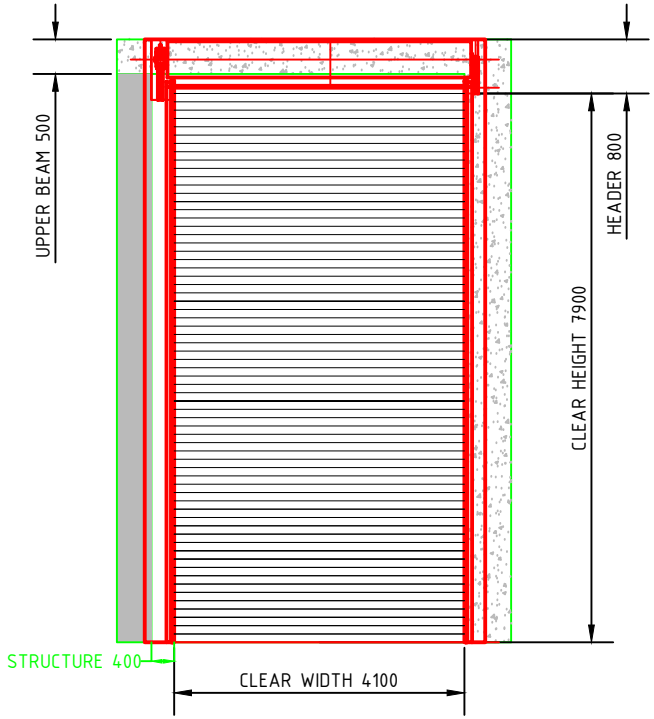

REQUIRED CLEAR SIZE 4515 X 8200
ACTUAL CLEAR SIZE 4100 X 7900



Main Slats
Double Wall Rolling Shutter

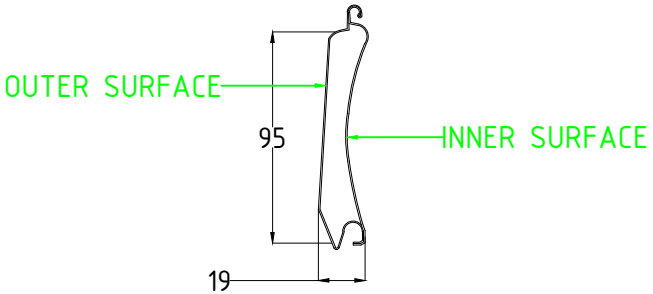

DIMENSION :

CLEAR WIDTH	CLEAR HEIGHT	QUANTITY
4100 mm	7900 mm	
4100 mm	7700 mm	

MATERIAL :

THICKNESS :

NOTE:-
1. THIS IS A REFERENCE DRAWING.
2. THIS DRAWING REPRESENTS THE FITMENT OF ROLLING ON OUTER WALL.
3. CLEAR WIDTH WILL BE REDUCED 400 MM BECAUSE OF THE UNAVAILABILITY OF THE STRUCTURE FOR MOTOR AND GUIDE MOUNTING.

NIHVA TECHNOLOGIES PVT. LTD.
NIHVA TECHNOLOGIES PVT. LTD. PUNE
Email:- info@nihva.com
Website:- www.nihva.com

TITLE:
DOUBLE WALL ROLLING SHUTTER FITTED FROM OUTSIDE

CLIENT'S APPROVAL :

CLIENT - SEZ BIOTECH
PROJECT -
SITE LOCATION - PUNE
DWG. NO. : NIHVA/20-21/0205/REF-OS

SCALE: NTS	WT:	SHEET:1 OF 1
DRAWN BY: G.P.		DATE: 09-09-2021
CHECKED BY: A.K.		DATE: 09-09-2021
APPROVED BY : V.T.		DATE: 09-09-2021

If any queries contact : design@nihva.com
NOTE: ALL DIMENSIONS ARE IN mm

THIS DRAWING & DESIGN IS THE PROPERTY OF NIHVA TECHNOLOGIES. NOT TO BE SOLD OR COPIED TO ANY OTHER CONCERN.