




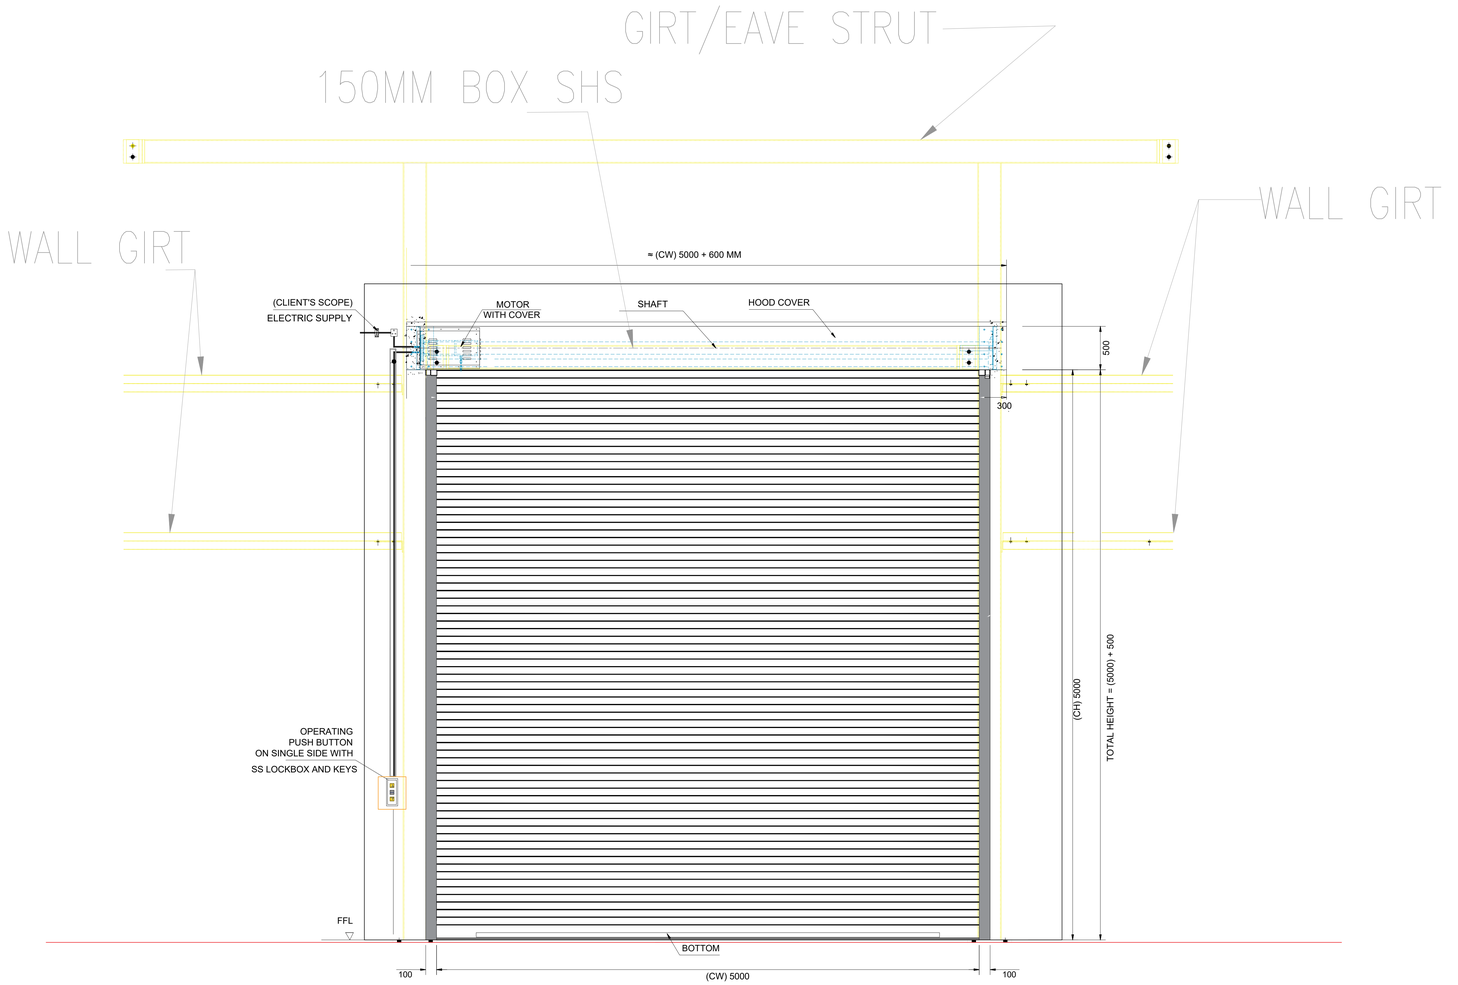

INSIDE ELEVATION

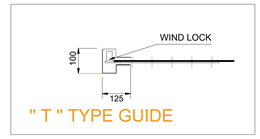

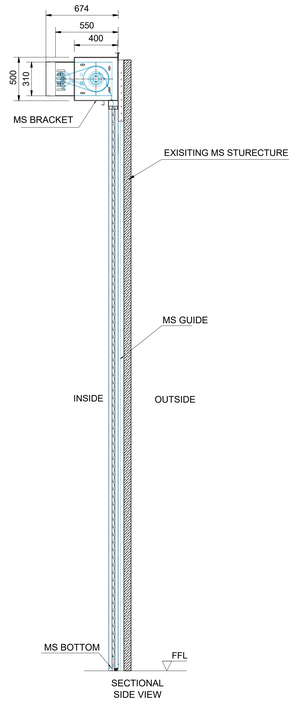

TECHNICAL SPECIFICATION:-

SR.	SPECIFICATION	DETAILS
1.	Description & Drive	Motorized Rolling Shutter (Direct Drive With CE Certificated)
2.	Location Area	Inside
3.	Mounting Surface	MS STRACTURE
4.	Slat	AS PER NIHVA STD.
5.	Bottom Profile	MS Plate 100 x 2.5 mm thick with Angle Stiffner with rubber seal
6.	Guide Profile	M.S." T " Shape profile 100 x 3 mm Thk.
7.	Hood Cover & Motor Cover	Made of GI Sheet Thickness 0.9 mm
8.	Surface finish	SYNTHETIC ENAMEL PAINT RAL SHADE 9002
9	Accessories	Push Button Single side

SHUTTER SIZES :-

SR.	CLEAR WIDTH	CLEAR HEIGHT	QTY.
01	5000 mm	5000 mm	3

Note :-

1. All Dimension are in mm
2. This drawing is only for understanding purpose

This drawing & designing is the property of NIHVA TECHNOLOGIES. Not to be sold or copied to any other concern.

TITLE :- MOTORISED ROLLING SHUTTER			NIHVA TECHNOLOGIES PVT. LTD. PUNE Tel : 020 66304033 Email:- info@nihva.com Website:- www.nihva.com
	NAME	DATE	CLIENT - SMP INFRASTRUCTURE PVT. LTD.
DRAWN	B.S.	13/02/2025	PROJECT - ROLLING SHUTTER
CHECK	V.M.	13/02/2025	FORMAT NO - NIHVA-DD-F-03
APPROVAL	V.T.	13/02/2025	DWG. NO. : NIHVA/24-25/SMP/250124 / REV-02
			SCALE: NTS / WT: / SHEET: 01 OF 01
ALL DIMENSION ARE IN mm			If any queries contact : design@nihva.com