




Elevation 1

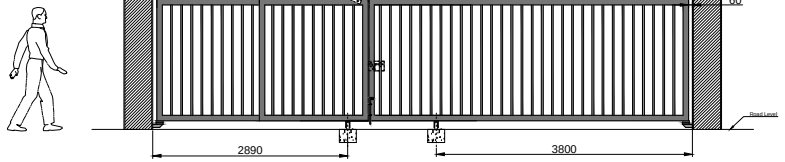


Elevation 2

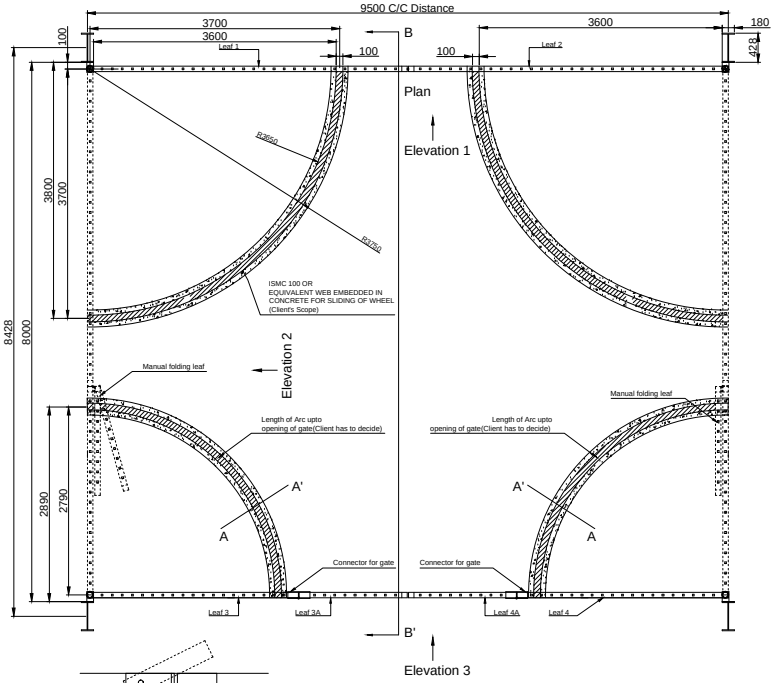


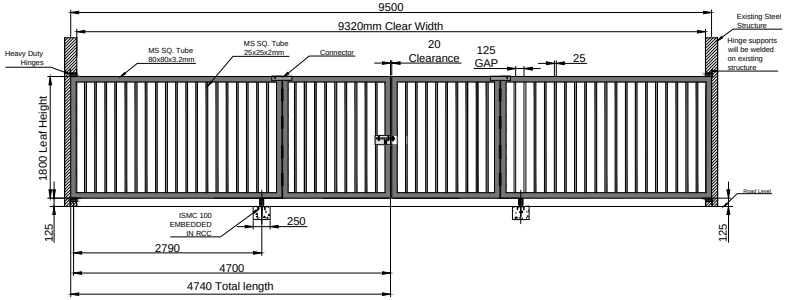


Elevation 3

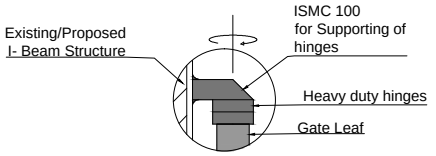

Detail view of A

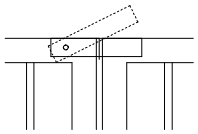

Connector Details

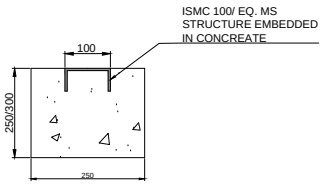

SECTION A-A'

NOTE-
1. ALL REQUIRED CIVIL WORK WILL BE IN CLIENTS SCOPE.
2. ONE COAT OF RED OXIDE & TWO COAT OF APPROVED RAL SHADE WILL BE GIVEN TO THE GATE.

Color- 1. For Outer Boundry Golden Yellow RAL 1004
2. For Inner Tubes Marine blue RAL 5002

Color Shade are as per previously approved gates. Client has to confirm the same.

SR NO	TUBE SPECIFICATION	
01	MS 80X80X3.2mm	OUTER FRAME
02	MS 25X25X2mm	INNER PATTERN

TOLERANCE - ±10mm

This drawing & design is the property of NIHVA TECHNOLOGIES. Not to be sold or copied to any other concern.

TITLE

ASSEMBLY

NIHVA TECHNOLOGIES PVT. LTD.
NIHVA TECHNOLOGIES PVT. LTD. PUNE
Tel : 020 66304033
Email:- info@nihva.com
Website:- www.nihva.com

	NAME	SIGN	DATE
DRAWN	OMKAR		12-01-2018
CHECK	PRADEEP		12-01-2018
APPRD.	PRADEEP		12-01-2018

CLIENT -

PROJECT -

SITE LOCATION -

If any queries contact : design@nihva.com

DWG. NO. : NIHVA/17-18/0335/R03

REV- 3

ALL DIMENSION ARE IN mm

SCALE: NTS

WT:

SHEET: 01 OF 01