
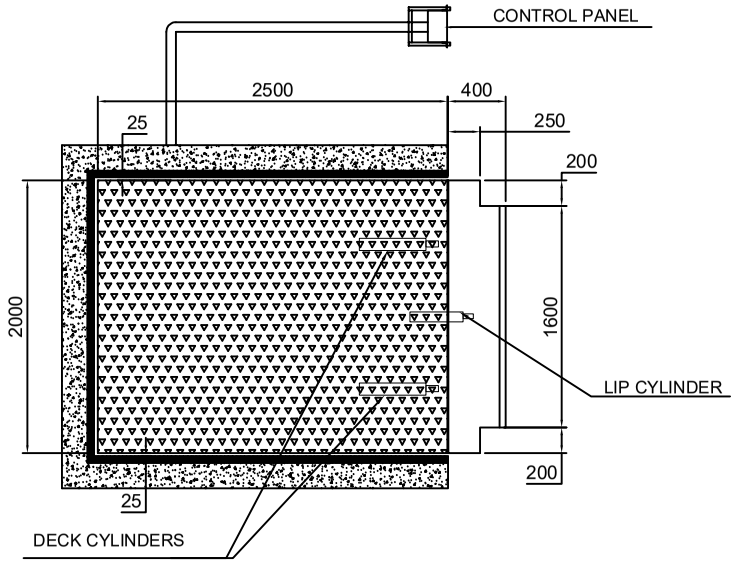
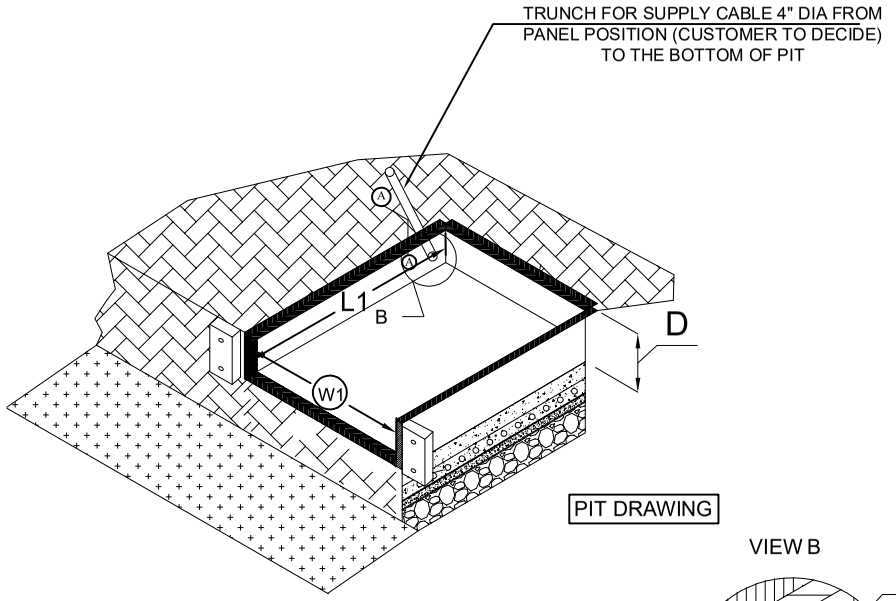
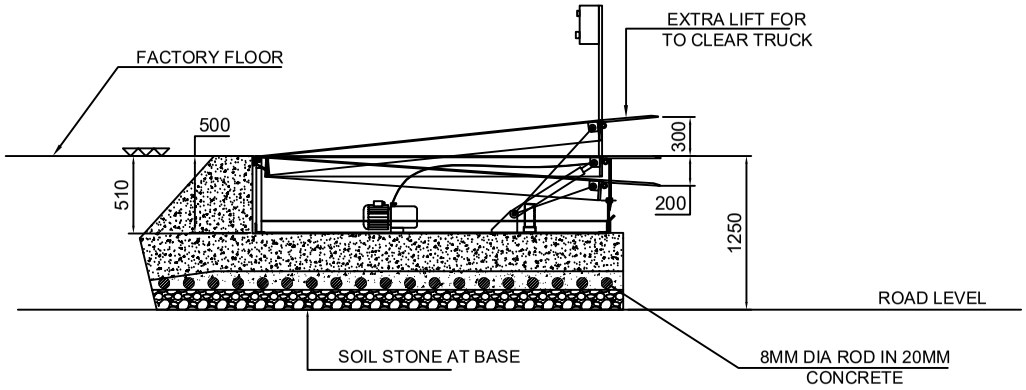
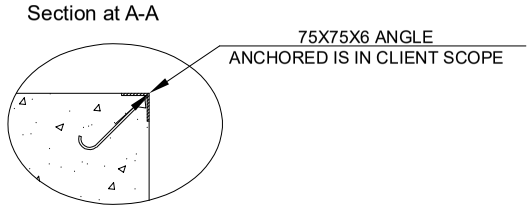



PIT DRAWING

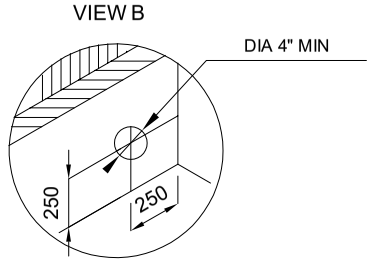


Capacity:- 10TON

| DOCK LEVELER SIZE | WIDTH (W) | LENGTH ( L) | HEIGHT (H) | LIP (C) LENGTH |
|---|---|---|---|---|
| | 2000 | 2500 | 500 | 400 |
| PIT DIMENSION | WIDTH (W 1) | LENGTH ( L 1) | DEPTH (D) | |
| DL | 2050 | 2550 | 510 | |

NOTE:-

1.ALL DIMENSION ARE IN MM
2. PROPER DRAINAGE SHOULD BE DONE
3. TRENCH AS SHOWN SHOULD BE MADE BY DECIDING THE POWER PACK POSITION.
4. LEVEL OF THE PIT SHOULD BE PLAIN AND SHOULD TAKE AT LEAST 18000 KG FLOOR LOADING
5. INSTALLLATION AND FABRICATION TOLERANCE FOR PLATFROM SIZE WILL BE ± 20 MM.
6. PIT,DUCT FOR HOSES & ALL CIVIL WORK IN CLIENT SCOPE
7.SURFACE FINISH: APPROVED RAL CODE 1004.

| Rev No. | Revision | Date | Revised By |
|---|---|---|---|
| | | | |

This drawing & design is the property of NIHVA TECHNOLOGIES. Not to be sold or copied to any other concern.

TITLE:- DOCK LEVELER GA DRAWING

NIHVA TECHNOLOGIES PVT. LTD.

| | NAME | DATE | SIGN |
|---|---|---|---|
| DRAWN | SUJATA | 15/07/2023 | |
| CHECK | | | |
| APPRD. | | | |

If any queries contact : design@nihva.com

ALL DIMENSION ARE IN mm

CLIENT - ASIAN PAINT

LOCATION - RAJKOT

PRODUCT - DOCK LEVELER

DWG NO:-NIHVA/22-23/CLT/0152_RJKT | REV- 0

SCALE: NTS | SCALE:-- 1:1 | SHEET: 01 OF 01