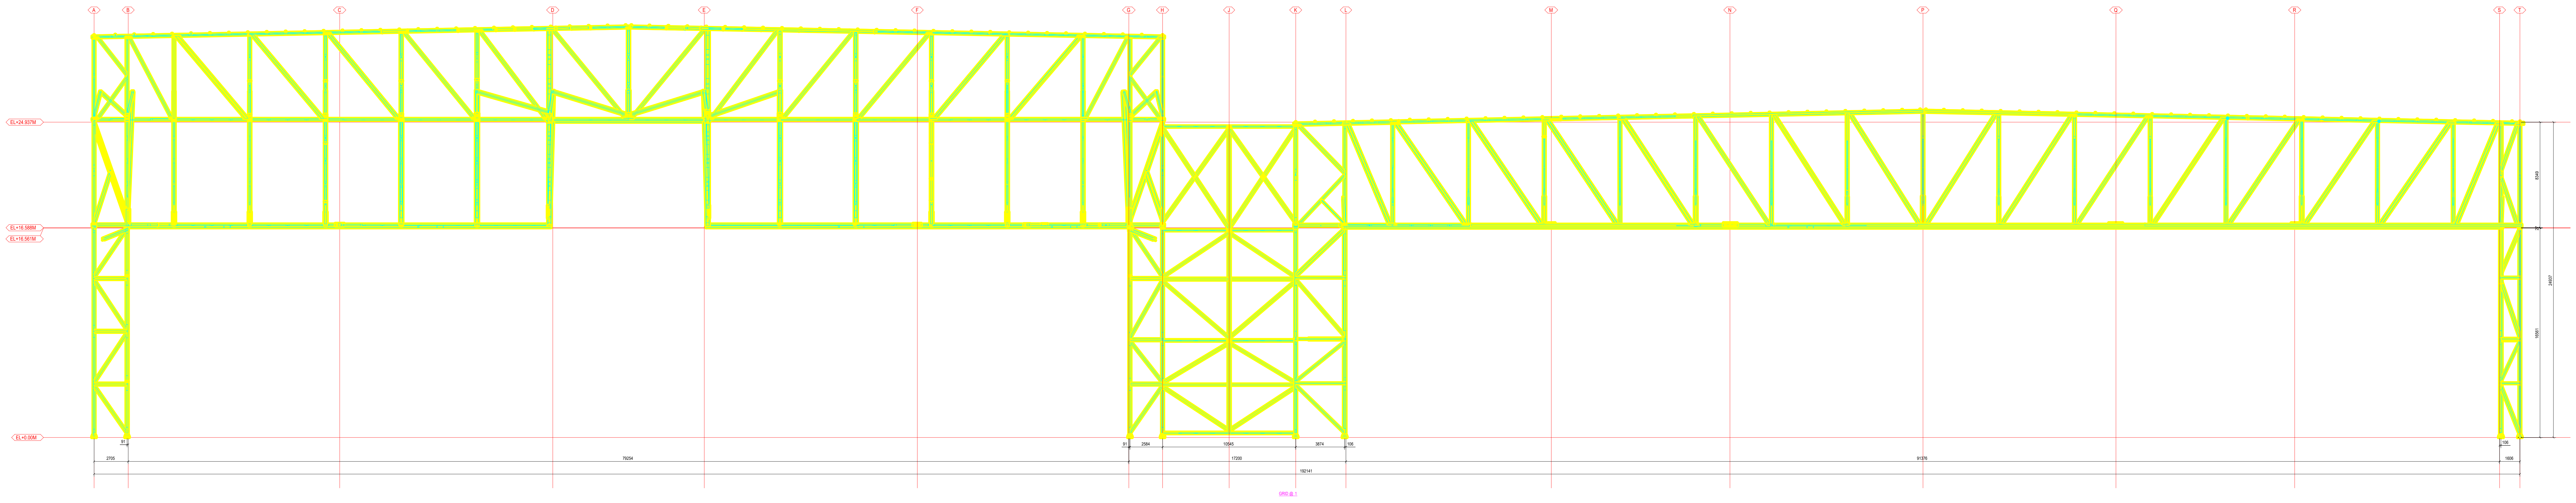
A
B
C
D
E
F
G
H
J
K
L
M
N
P
Q
R
S
T
EL+24.937M
EL+16.588M
EL+16.561M
EL+0.00M
8349
27
16561
24937
91
2705
79254
2584
10545
3874
106
17200
91376
1606
192141
GRID @ 1

0	ISSUED FOR APPROVAL	05.11.22	IMS	HAB	HAB
REV.NO.	DESCRIPTION.	REV.DATE	DRAWN.	CHKD.	APPD.

DWG.TITLE :- DETAIL DRAWING FOR 84MTR

PROJECT	MEGADOOR INSTALLATION AT HYDRABAD AIRPORT
CLIENT	GMR

SALT Design Services

NIHVA

NIHVA TECHNOLOGIES PVT. LTD.

SALT DESIGN SERVICES

NIHVA TECHNOLOGIES
PVT. LTD. PUNE
Tel : 020 66304033
Email:- info@nihva.com
Website:- www.nihva.com

DRAWN :RRK	CHECKED : HAB	SCALE: 1:100
APPROVED : HAB	JOB CODE. : 1729	DATE: 05.11.2022

DWG.NO: SALT_1729_FDN_01_R0 (SH-1OF1) REV. - R0 SIZE. - A1

A1 [841 x 594]