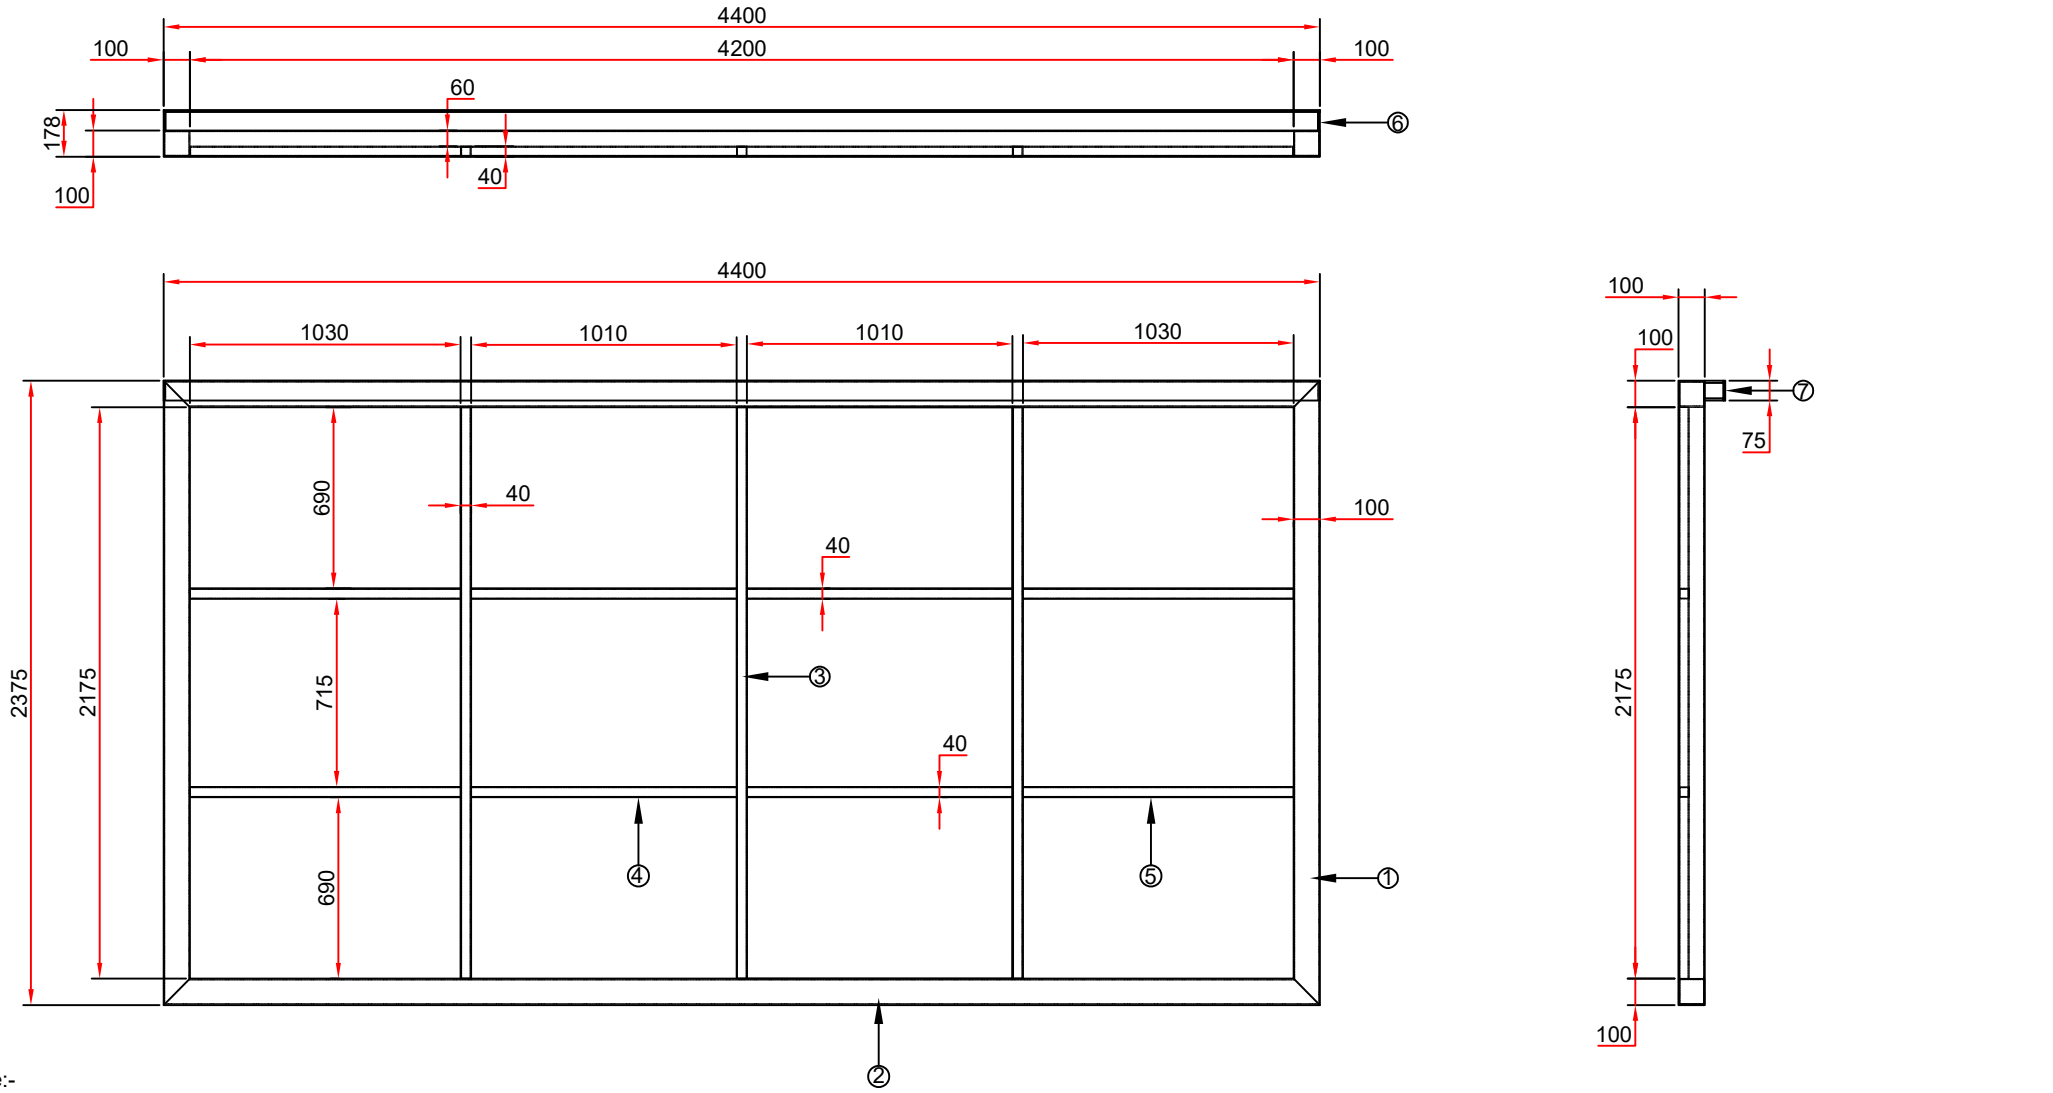


Note:-

1.All Dimension are in MM

2.Kindly Maintain the Given dimension

BOM			
SL NO.	DESCRIPTION	SPECIFICATION	QTY
1	MS SQ. TUBE	100X100X4X2375L	2NOS
2	MS SQ. TUBE	100X100X4X4400L	2NOS
3	MS SQ. TUBE	40X40X3.2X2175L	3NOS
4	MS SQ. TUBE	40X40X3.2X1010L	4NOS
5	MS SQ. TUBE	40X40X3.2X1030L	4NOS
6	MS FLAT	75X8X70L	2NOS
7	MS FLAT	75X8X4400L	1NO

Rev No.	Revision	Date	Revised By

This drawing & design is the property of NIHVA TECHNOLOGIES. Not to be sold or copied to any other concern.

TITLE:- Master Sliding Leaf (E18 GATE)

	NAME	DATE	SIGN
DRAWN	SUJATA	21/07/2022	
CHECK	M.S	21/07/2022	
APPRD.	A.K	21/07/2022	

If any queries contact : design@nihva.com

ALL DIMENSION ARE IN mm

NIHVA TECHNOLOGIES PVT. LTD.

NIHVA TECHNOLOGIES PVT. LTD. PUNE
Tel : 020 66304033
Email:- info@nihva.com
Website:- www.nihva.com


CLIENT - OC Specialities


LOCATION - Solapur


PRODUCT - Master Sliding Leaf | QTY-01

DWG NO:- NIHVA/22-23/MFG/0042 | REV-00

SCALE: NTS | SCALE:-- 1:1 | SHEET: 01 OF 01

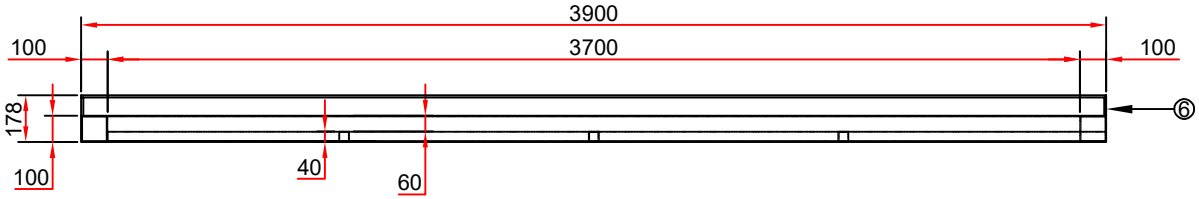

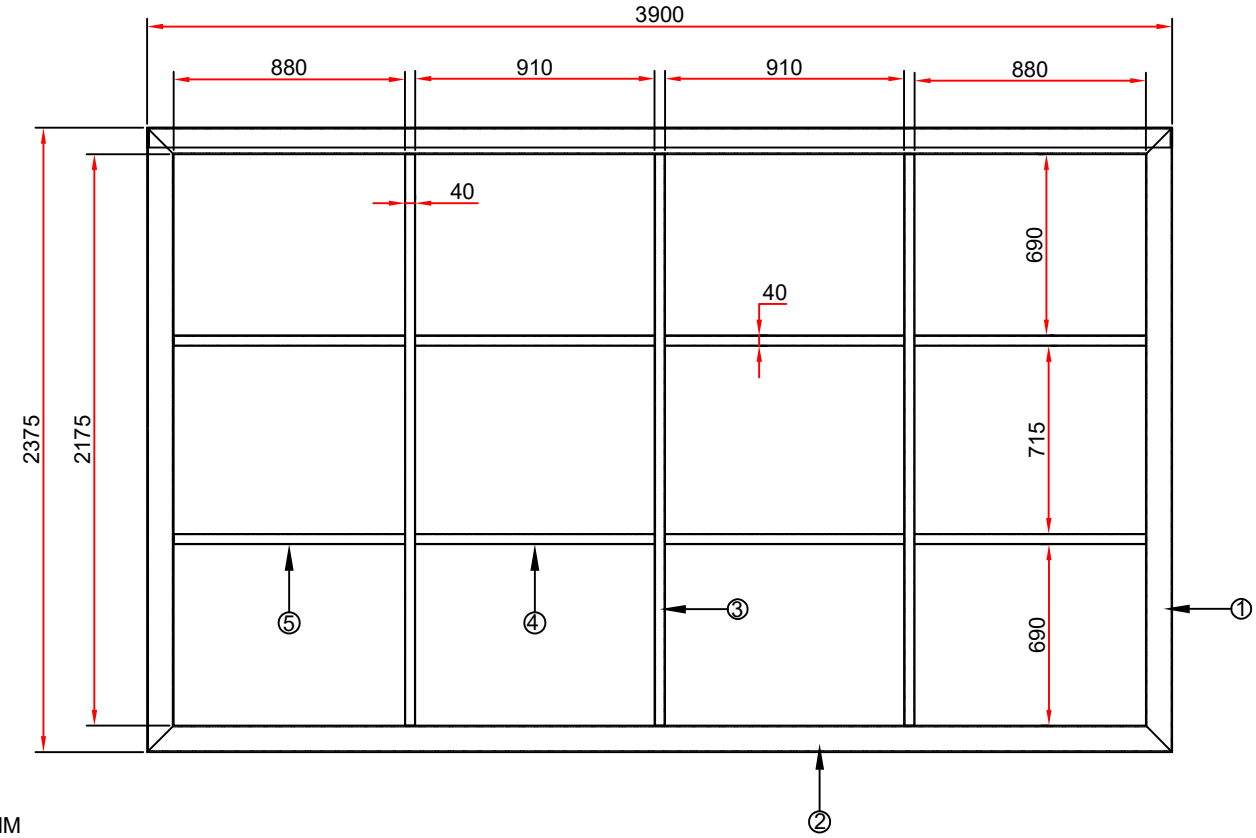

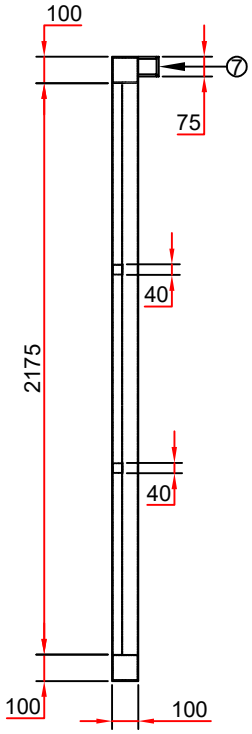

Note:-

1.All Dimension are in MM

2.Kindly Maintain the Given dimension

3.Given BOM Material in table For Single leaf

BOM FOR SINGLE LEAF

SL NO.	DESCRIPTION	SPECIFICATION	QTY
1	MS SQ. TUBE	100X100X4X2375L	2NOS
2	MS SQ. TUBE	100X100X4X3900L	2NOS
3	MS SQ. TUBE	40X40X3.2X2175L	3NOS
4	MS SQ. TUBE	40X40X3.2X910L	4NOS
5	MS SQ. TUBE	40X40X3.2X880L	4NOS
6	MS FLAT	75X8X70L	2NOS
7	MS FLAT	75X8X3900L	1NO

Rev No.	Revision	Date	Revised By

QTY- 02Nos

This drawing & design is the property of NIHVA TECHNOLOGIES. Not to be sold or copied to any other concern.

TITLE:- Sliding Leaf1(E18 GATE)

NIHVA TECHNOLOGIES PVT. LTD.

NIHVA TECHNOLOGIES PVT. LTD. PUNE
Tel : 020 66304033
Email:- info@nihva.com
Website:- www.nihva.com

	NAME	DATE	SIGN
DRAWN	SUJATA	21/07/2022	
CHECK	M.S	21/07/2022	
APPRD.	A.K	21/07/2022	


CLIENT - OC Specialities


LOCATION - Solapur


PRODUCT - Sliding leaf | QTY- 02Nos

If any queries contact : design@nihva.com | DWG NO:- NIHVA/22-23/MFG/0044 | REV-00

ALL DIMENSION ARE IN mm | SCALE: NTS | SCALE:-- 1:1 | SHEET: 01 OF 01

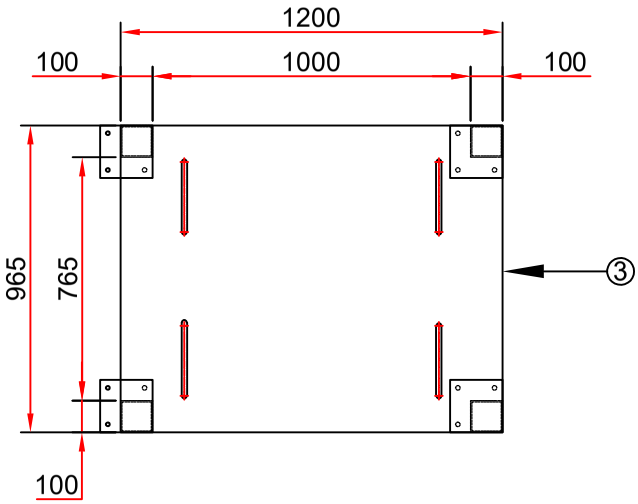

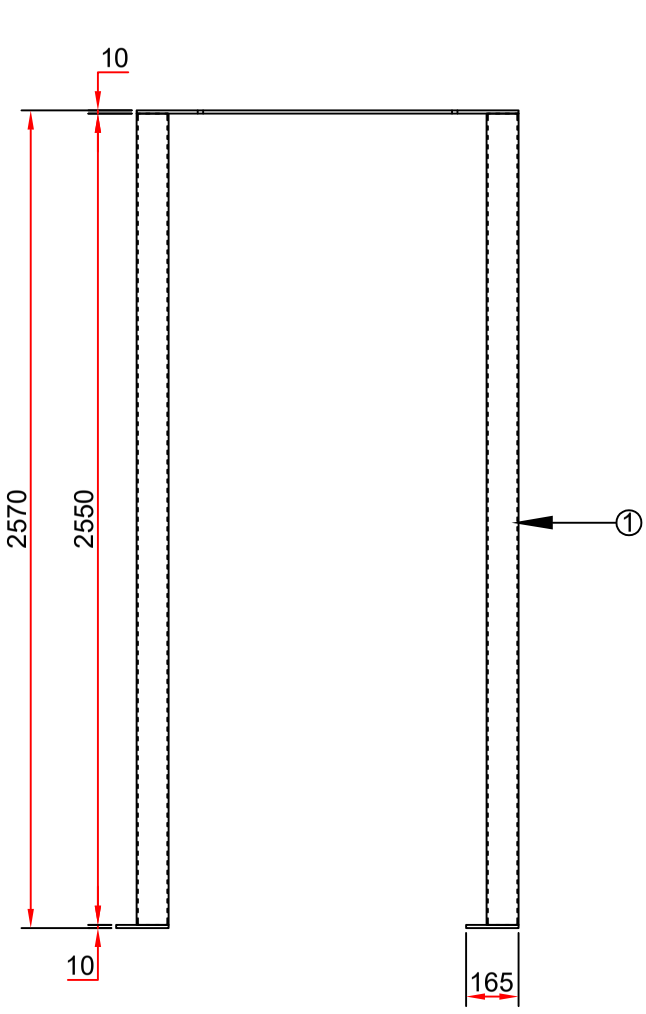

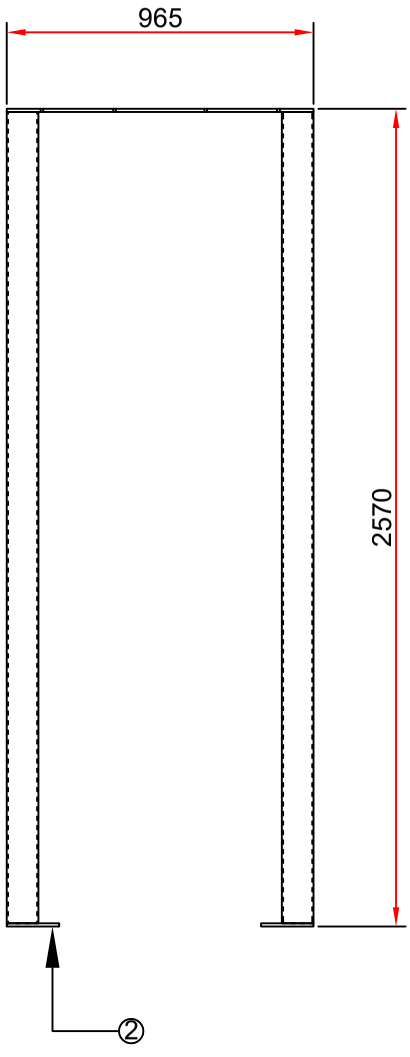

BOM FOR POST			
SL NO.	DESCRIPTION	SPECIFICATION	QTY
1	MS SQ. TUBE	100X100X4X2550L	4NOS
2	POST SUPPORT PLATE	165X165X10THK	4NOS
3	ROLLER SUPPORT PLATE	1200X965X10THK	1NO

Rev No.	Revision	Date	Revised By

This drawing & design is the property of NIHVA TECHNOLOGIES. Not to be sold or copied to any other concern.

TITLE:- POST(E18 GATE)

NIHVA TECHNOLOGIES PVT. LTD.

NIHVA TECHNOLOGIES PVT. LTD. PUNE
Tel : 020 66304033
Email:- info@nihva.com
Website:- www.nihva.com

	NAME	DATE	SIGN
DRAWN	SUJATA	21/07/2022	
CHECK	M.S	21/07/2022	
APPRD.	A.K	21/07/2022	

If any queries contact : design@nihva.com

ALL DIMENSION ARE IN mm


CLIENT - OC Specialities


LOCATION - Solapur

PRODUCT - Motor side Post | QTY:-1 NO

DWG NO:-NIHVA/22-23/MFG/0045 | REV- 0

SCALE: NTS | SCALE:-- 1:1 | SHEET: 01 OF 01

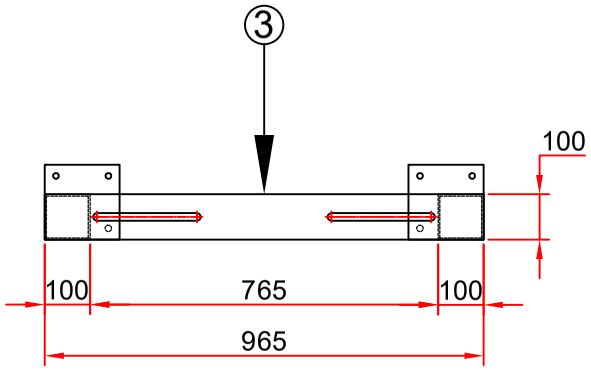

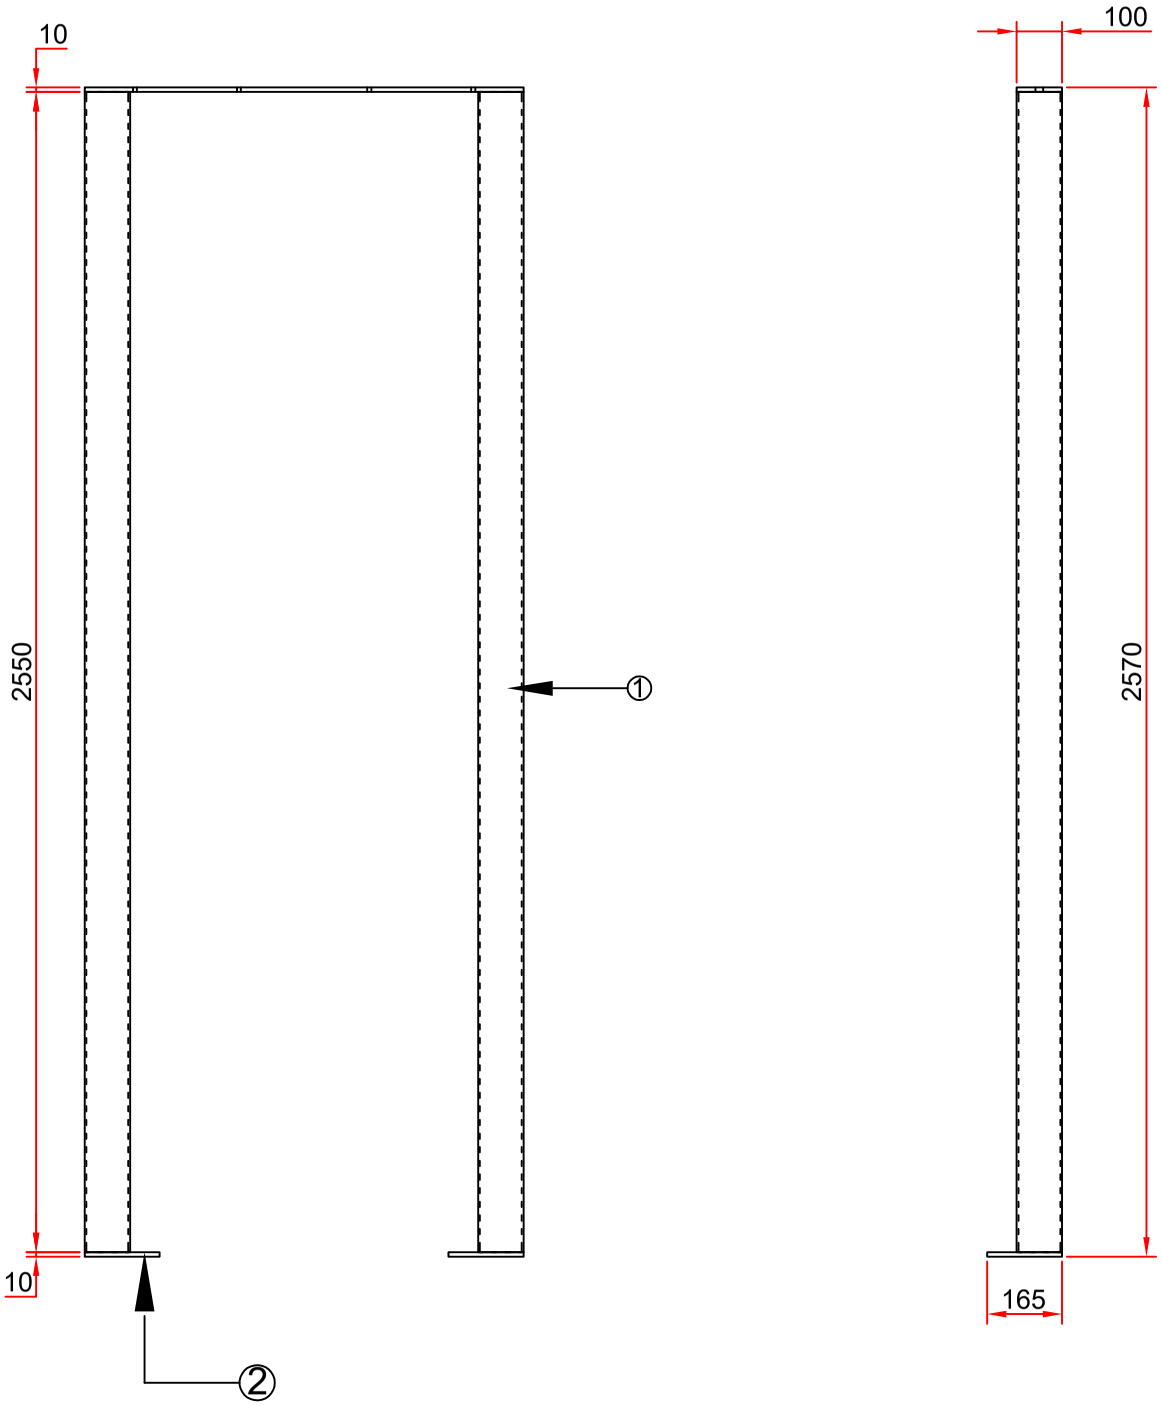

BOM FOR POST			
SL NO.	DESCRIPTION	SPECIFICATION	QTY
1	MS SQ. TUBE	100X100X4X2550L	2NOS
2	POST SUPPORT PLATE	165X165X10THK	2NOS
3	ROLLER SUPPORT PLATE	965X100X10THK	1NO

Rev No.	Revision	Date	Revised By

This drawing & design is the property of NIHVA TECHNOLOGIES. Not to be sold or copied to any other concern.

TITLE:- POST (E18 GATE)

NIHVA TECHNOLOGIES PVT. LTD.

NIHVA TECHNOLOGIES PVT. LTD. PUNE
Tel : 020 66304033
Email:- info@nihva.com
Website:- www.nihva.com

	NAME	DATE	SIGN
DRAWN	SUJATA	21/07/2022	
CHECK	M.S	21/07/2022	
APPRD.	A.K	21/07/2022	

If any queries contact : design@nihva.com

ALL DIMENSION ARE IN mm


CLIENT - OC Specialities

LOCATION - Solapur


PRODUCT - End Post1 | QTY:-1 NO


DWG NO:-NIHVA/22-23/MFG/0046 | REV- 0

SCALE: NTS | SCALE:-- 1:1 | SHEET: 01 OF 01

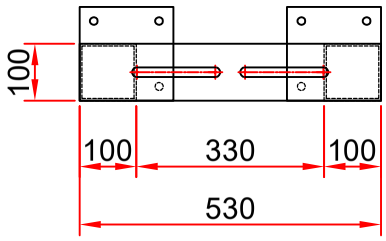

BOM FOR POST			
SL NO.	DESCRIPTION	SPECIFICATION	QTY
1	MS SQ. TUBE	100X100X4X2550L	2NOS
2	POST SUPPORT PLATE	165X165X10THK	2NOS
3	ROLLER SUPPORT PLATE	530X100X10THK	1NO

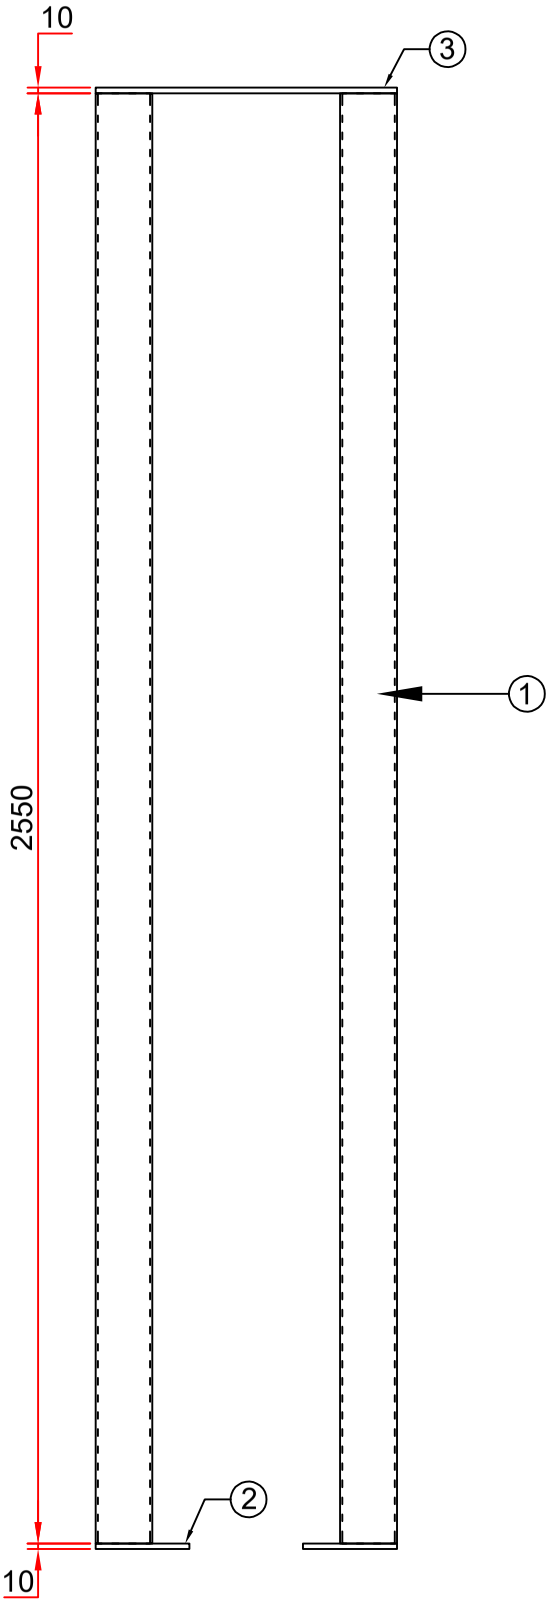

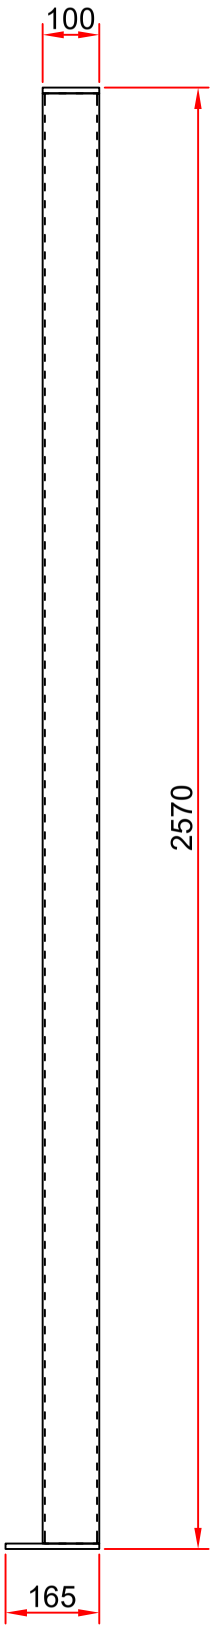

This drawing & design is the property of NIHVA TECHNOLOGIES. Not to be sold or copied to any other concern.

TITLE:- POST (E18 GATE)

NIHVA TECHNOLOGIES PVT. LTD.

NIHVA TECHNOLOGIES PVT. LTD. PUNE
Tel : 020 66304033
Email:- info@nihva.com
Website:- www.nihva.com

	NAME	DATE	SIGN
DRAWN	SUJATA	21/07/2022	
CHECK	M.S	21/07/2022	
APPRD.	A.K	21/07/2022	

If any queries contact : design@nihva.com

ALL DIMENSION ARE IN mm

CLIENT - OC Specialities


LOCATION - Solapur


PRODUCT -End Post2 | QTY:-1 NO


DWG NO:-NIHVA/22-23/MFG/0047 | REV- 0


SCALE: NTS | SCALE:-- 1:1 | SHEET: 01 OF 01

Rev No.	Revision	Date	Revised By

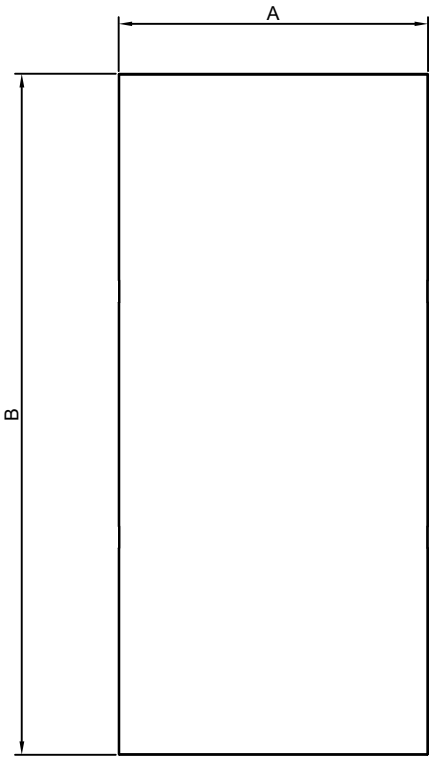

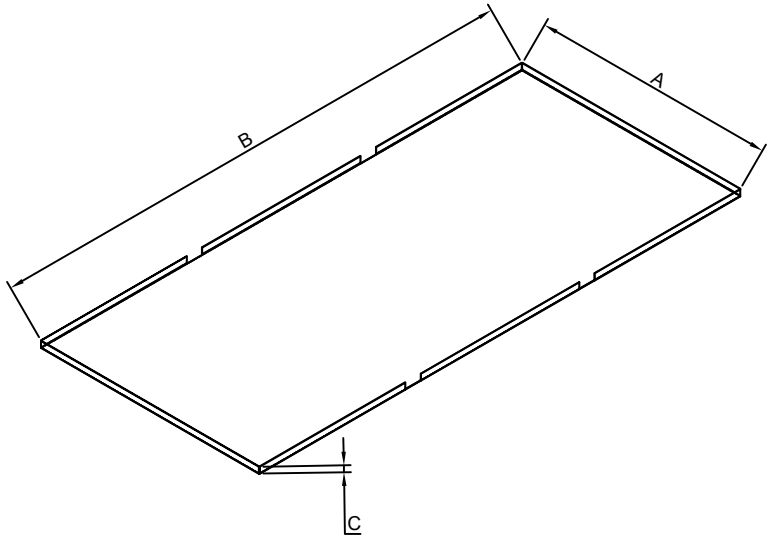

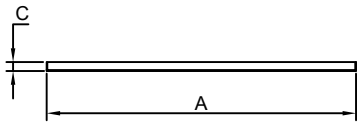

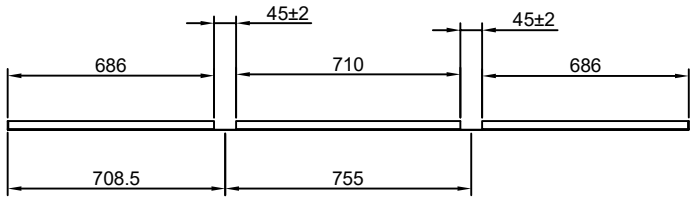

NOTE:-

1.ALL DIMENSION ARE IN MM.

2.KINDLY MAINTAIN THE DIMESTION OF THE TRAY.

3.IF HAVE ANY QUERIES DO LET ME KNOW.

DIMENSIONS FOR TRAY					
SL NO.	A±2MM	B±2MM	C	THICKNESS	QTY
1	1027	2172	25	1.2	2NOS
2	1007	2172	25	1.2	2NOS
3	877	2172	25	1.2	4NOS
4	907	2172	25	1.2	4NOS

This drawing & design is the property of NIHVA TECHNOLOGIES. Not to be sold or copied to any other concern.

TITLE:- TRAY (E18 GATE)

NIHVA TECHNOLOGIES PVT. LTD.

NIHVA TECHNOLOGIES PVT. LTD. PUNE
Tel : 020 66304033
Email:- info@nihva.com
Website:- www.nihva.com

	NAME	DATE	SIGN
DRAWN	SUJATA	25/07/2022	
CHECK	M.S	25/07/2022	
APPRD.	A.K	25/07/2022	

If any queries contact : design@nihva.com

ALL DIMENSION ARE IN mm


CLIENT - Nihva Technologies Pvt Ltd

LOCATION -Pune

PRODUCT - Tray | QTY-

DWG NO:- NIHVA/22-23/VDR/0045 | REV-00

SCALE: NTS | SCALE:-- 1:1 | SHEET: 01 OF 01

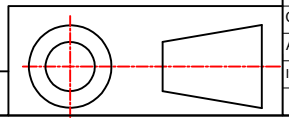

Rev No.	Revision	Date	Revised By