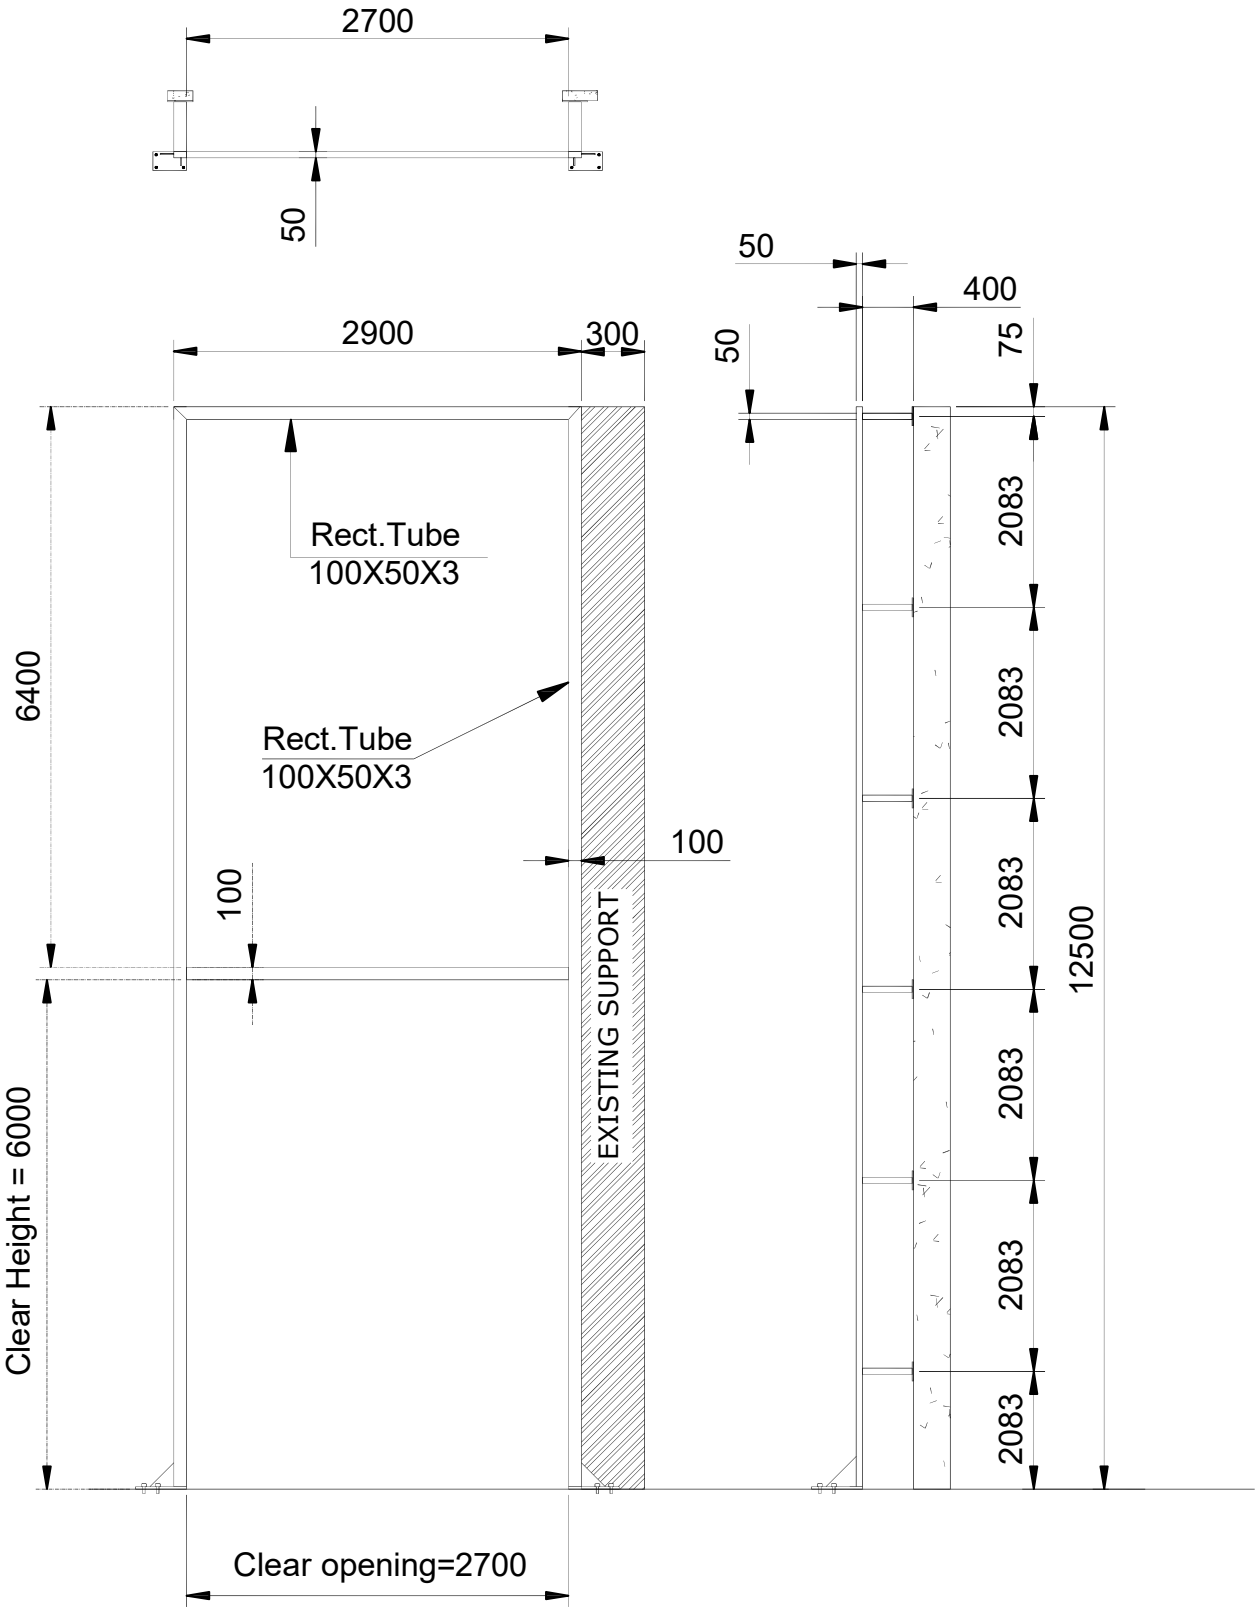


NOTE:-

1.All dimension are in MM

2.Required all civil work will be Client scope

3.Required 100X50X3 rect tubular structure will be client scope

This drawing & design is the property of NIHVA TECHNOLOGIES. Not to be sold or copied to any other concern.

TITLE:- MS Rect.tubular structure - VL				NIHVA TECHNOLOGIES PVT. LTD. PUNE Tel.: 020 66304033 Email:- info@nihva.com Website:- www.nihva.com	
	NAME	DATE	SIGN		
DRAWN	S.J	13-06-2024		CLIENT - FERRERO INDIA	
CHECK	B.B	13-06-2024		LOCATION - PUNE	
APPRD.	V.T	13-06-2024		PRODUCT -	QTY :- 01 NOS
If any queries contact : design@nihva.com				DWG NO:-NIHVA/24-25/XX00	REV- 0
ALL DIMENSION ARE IN mm				SCALE:NTS	SCALE:-- 1:1 SHEET: 01 OF 01

Rev No.	Revision	Date	Revised By