
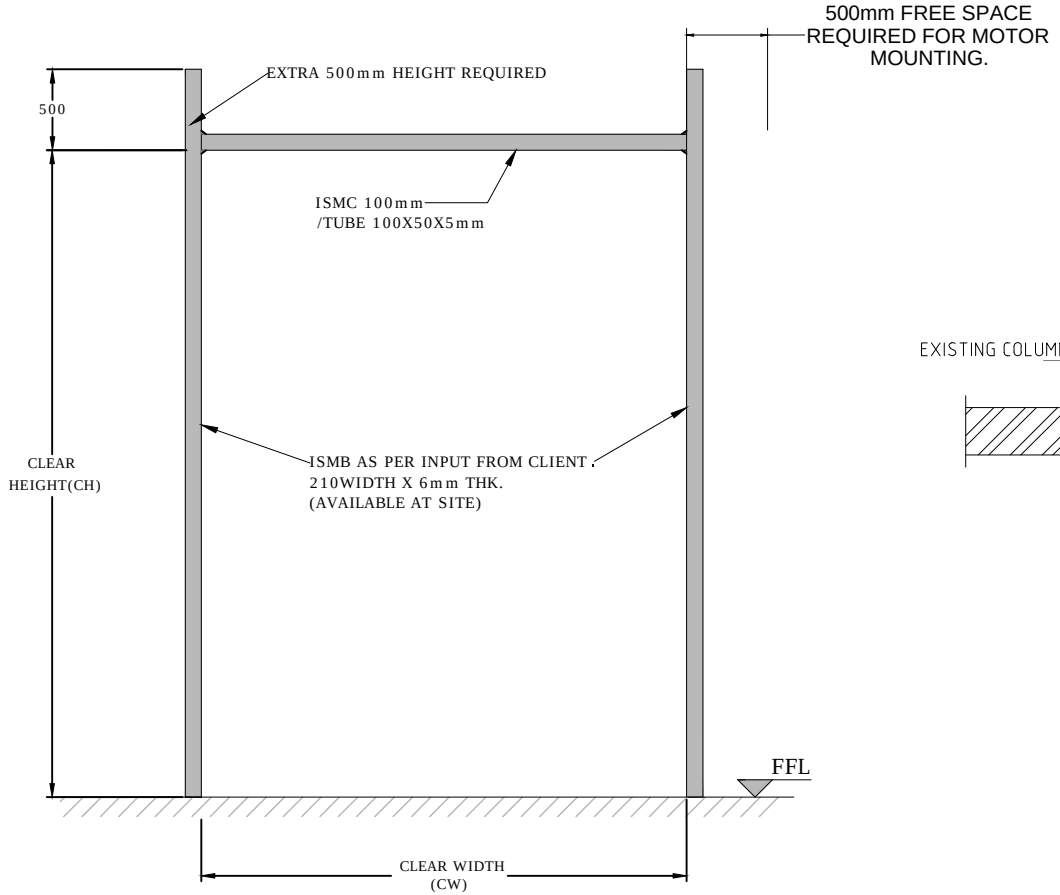


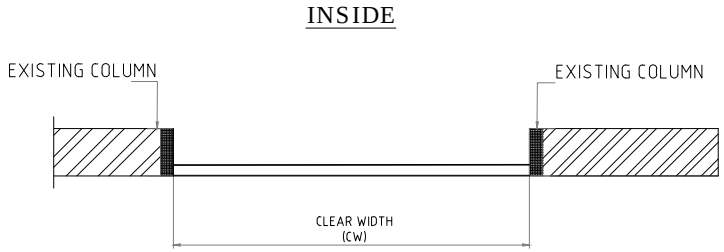

PLAN

NOTE: REQUIRED STRUCTURE FOR DOOR SHALL BE IN CLIENT'S SCOPE.

REV:- 25-06-2018.
1. MOUNTING MS TUBE/ISMC CHANGED ISMB

CLEAR WIDTH (CW)	CLEAR HEIGHT (CH)	QUANTITY
3000	4000	07

Tolerance:- ±10mm

This drawing & designing is the property of NIHVA TECHNOLOGIES. Not be sold or copy to any other concern.

TITLE
STRUCTURE FOR HIGH SPEED DOOR (RR 300 S).

NIHVA TECHNOLOGIES PVT. LTD.
NIHVA TECHNOLOGY PVT. LTD. PUNE
Tel : 020 66304033
Email:- info@nihva.com
Website:- www.nihva.com

	NAME	SIGN	DATE
DRAWN	SURAJ		30/05/18
CHECK	PRADEEP		30/05/18
APPRD.	PRADEEP		30/05/18

CLIENT - BECRICAP
PROJECT-
SITE:- CHAKAN.
ALL DIMENSION ARE IN mm
DWG. NO. - NIHVA/18-19/0046/R01
REV:- 01
If any queries contact : design@nihva.com
SCALE: NTS
WT:
SHEET: 01