

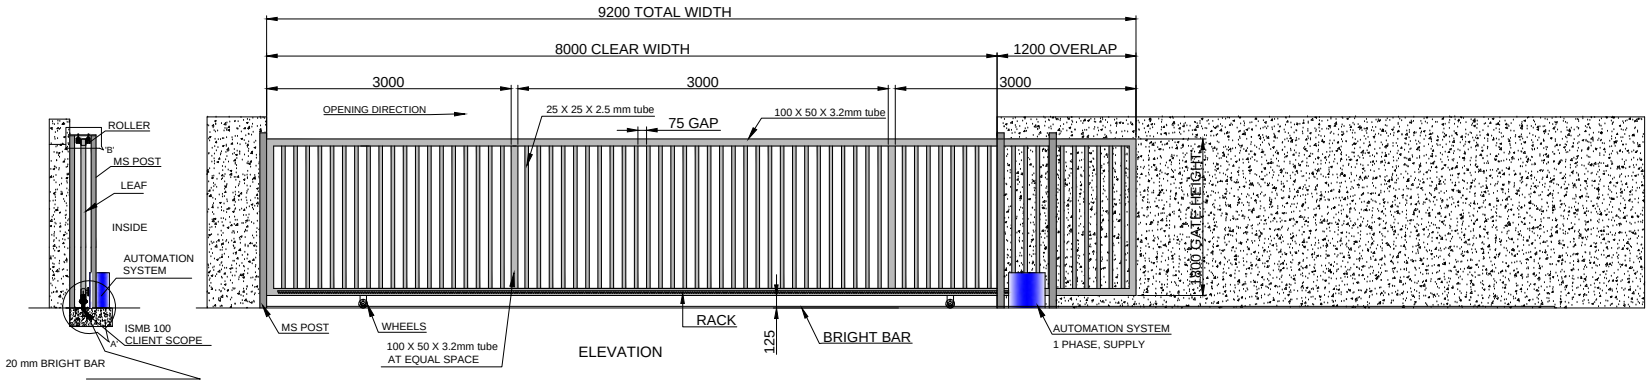



ELEVATION

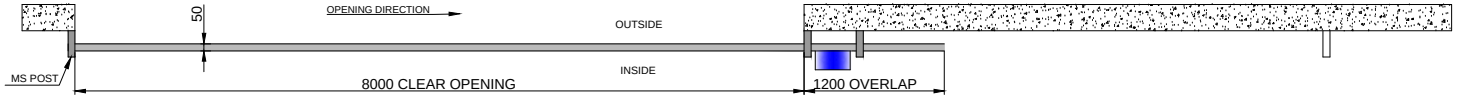


CLOSE POSITION PLAN VIEW

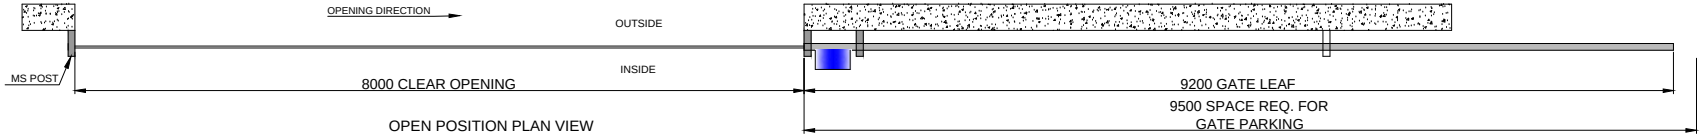

OPEN POSITION PLAN VIEW

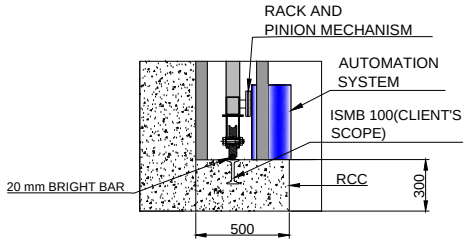

DETAIL VIEW OF A

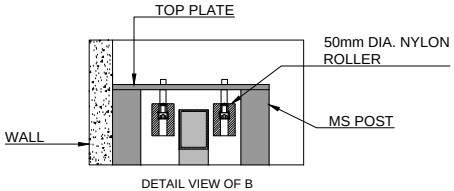

DETAIL VIEW OF B

NOTE-
1. ALL REQUIRED CIVIL WORK WILL BE IN CLIENTS SCOPE.
2. TWO COATS OF PRIMER AND TWO COATS OF SYNTHETIC ENAMEL PAINT OF APPROVE SHADE.
3. SAFETY ACCESSORIES : FLASHING LIGHT, SAFETY PHOTOCELL.
4. GATE LEAF WILL BE IN TWO/THREE PARTS FOR TRANSPORTATION & WILL BE WELD TOGETHER ON SITE.

GATE QTY : 2 NOS

TOLERANCE- ±10mm

This drawing & design is the property of NIHVA TECHNOLOGIES. Not to be sold or copied to any other concern.

TITLE	AUTOMATIC SLIDING GATE			NIHVA TECHNOLOGIES PVT. LTD. PUNE Tel : 020 66304033 Email:- info@nihva.com Website:- www.nihva.com	
	NAME	SIGN	DATE		
DRAWN	P.A		30.01.2020	CLIENT -	
CHECK	G.J		30.01.2020	PROJECT -	
APPRD.				SITE LOCATION -	
If any queries contact : design@nihva.com				DWG. NO. : NIHVA/19-20/VDR/299	REV- R00
ALL DIMENSION ARE IN mm				SCALE: NTS	WT: SHEET: