


SR.NO	DESCRIPTION	QTY
1	SQ.TUBE 30 X 30 X 3THK X 874L	4 NOS
2	SQ.TUBE 30 X 30 X 3THK X 1990L	2 NOS
3	SQ.TUBE 30 X 30 X 3THK X 1930L	2 NOS
4	SQ.TUBE 30 X 30 X 3THK X 407L	4 NOS
5	FLAT 50 X 16 THK X 100L	2 NOS
6	FLAT 50 X 10 THK X 100L	2 NOS
7	FLAT 50 X 16 THK X 75L	4 NOS
8	FLAT 50 X 10 THK X 75L	4 NOS

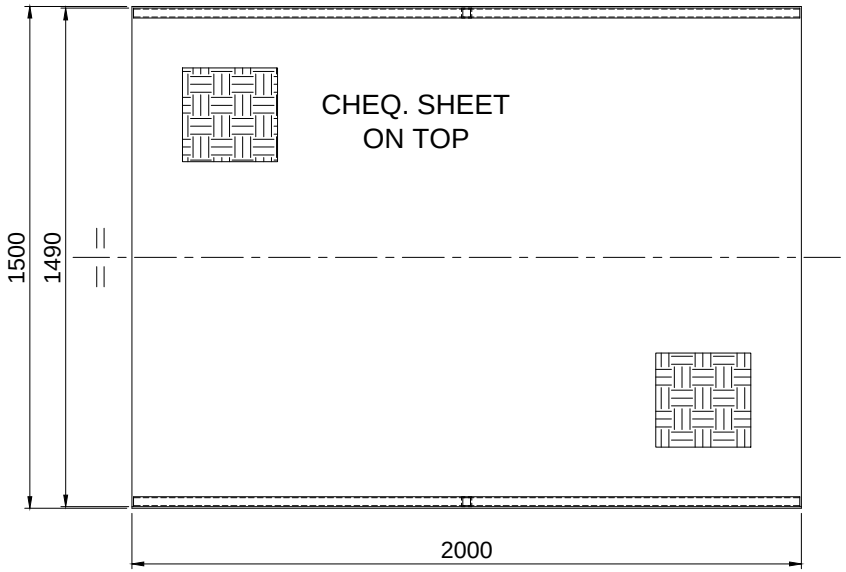

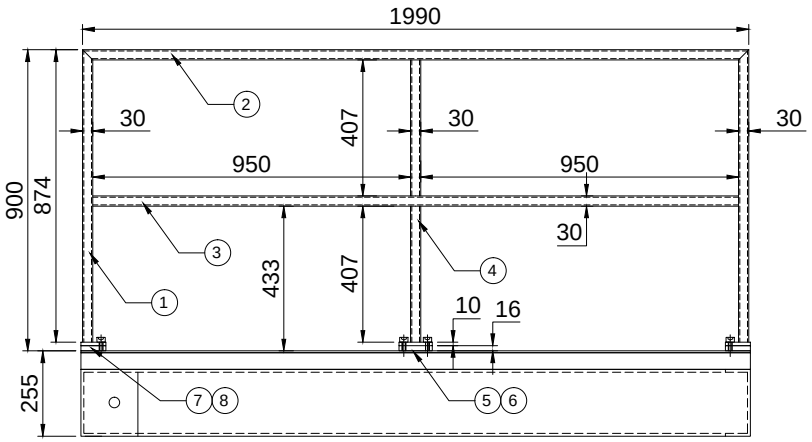

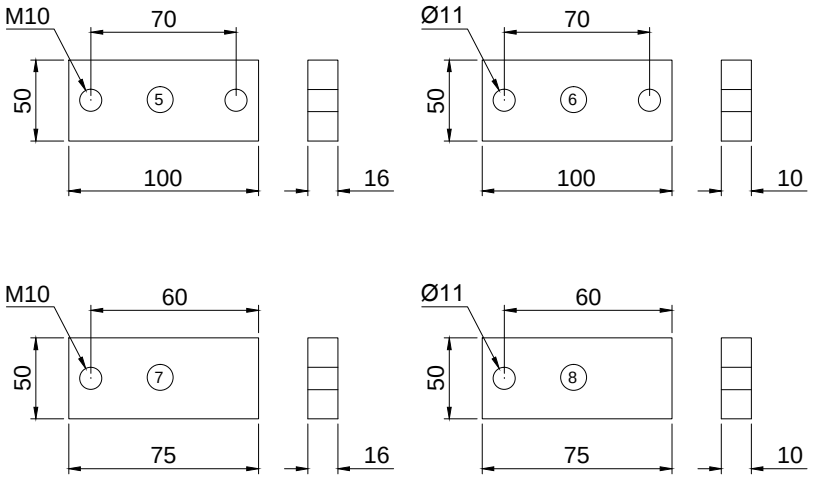

This drawing & design is the property of NIHVA TECHNOLOGIES. Not to be sold or copied to any other concern.

TITLE : -

RAILING ASSLY

	SIGN	DATE
DRAWN	P.A	10.01.19
CHECK	R.D	10.01.19
REV.		
APPROVAL		

If any queries contact : projects@nihva.com

ALL DIMENSION ARE IN mm

NIHVA TECHNOLOGIES PVT. LTD.

NIHVA TECHNOLOGIES PVT. LTD. PUNE
Tel : 020 66304033
Email:- info@nihva.com
Website:- www.nihva.com

CLIENT -

PROJECT -

SITE -

DWG. NO. : NIHVA/18-19//MFG/NSCL327/12

SCALE: NTS | WT: | SHEET: 01 OF 01