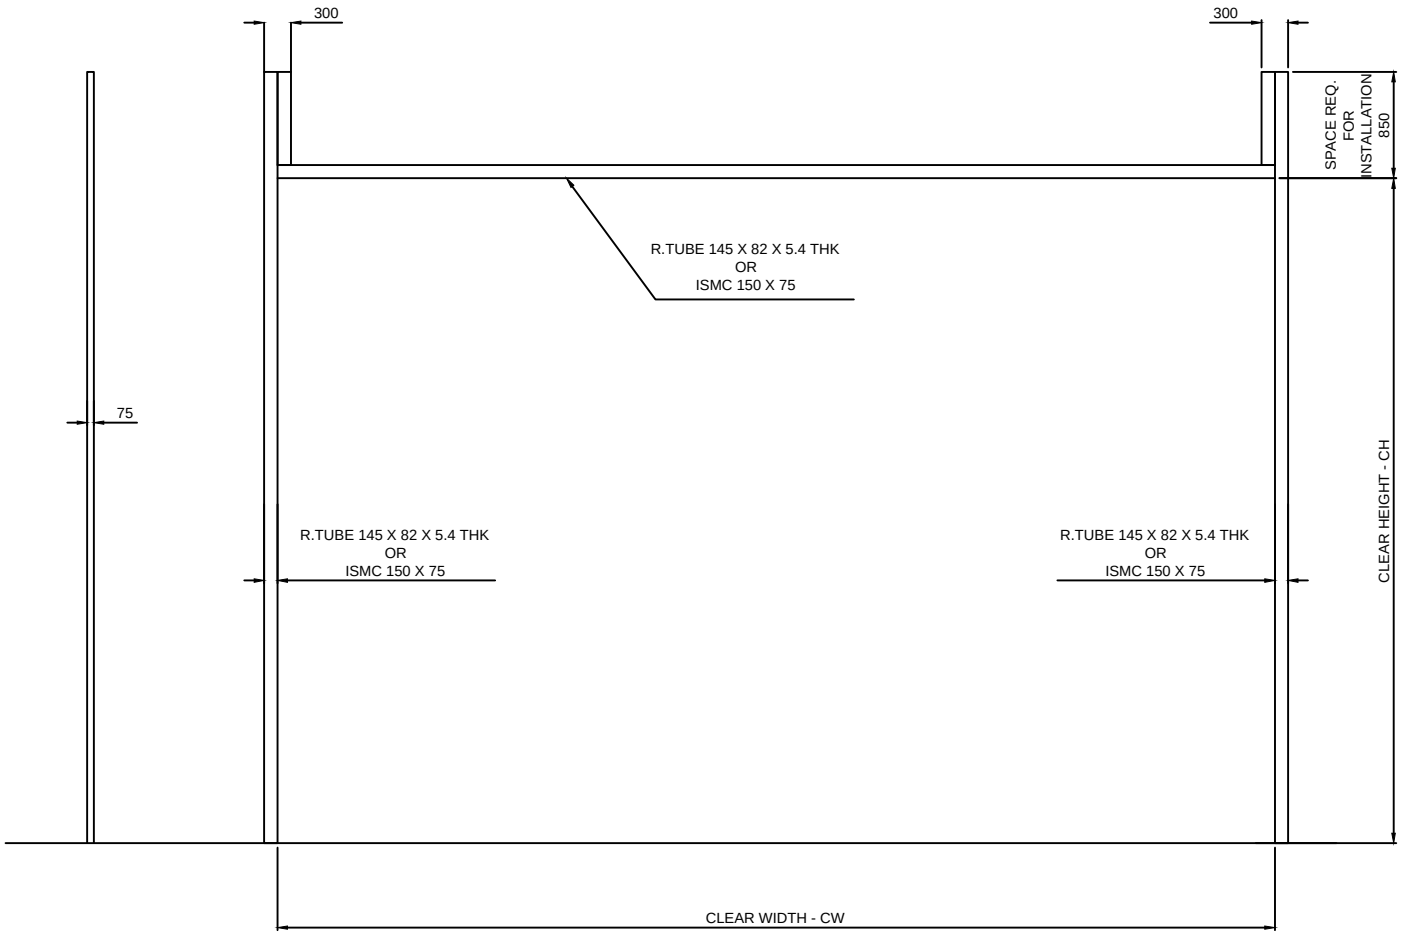


TOLERANCE ± 10 MM.

SR NO	CW CLEAR WIDTH	CH CLEAR HEIGHT	QTY
3	6500	4000	01 NO
2	7000	8000	7 NOS
1	7500	8000	2 NOS

This drawing & design is the property of NIHVA TECHNOLOGIES. Not to be sold or copied to any other concern.

TITLE: MOTORIZED ROLLING SHUTTER STRUCTURE

NIHVA TECHNOLOGIES PVT. LTD.

NIHVA TECHNOLOGIES PVT. LTD. PUNE
Tel : 020 66304033
Email:- info@nihva.com
Website:- www.nihva.com

	NAME	SIGN	DATE
DRAWN	P.A		20.01.2020
CHECK	G.J		20.01.2020
APPRD.			

CLIENT - HIRANANDANI

PROJECT -

SITE LOCATION -

If any queries contact : design@nihva.com

DWG. NO. : NIHVA/19-20/0200 REV- 0

ALL DIMENSION ARE IN mm

SCALE: NTS WT: SHEET: 01 OF 01