
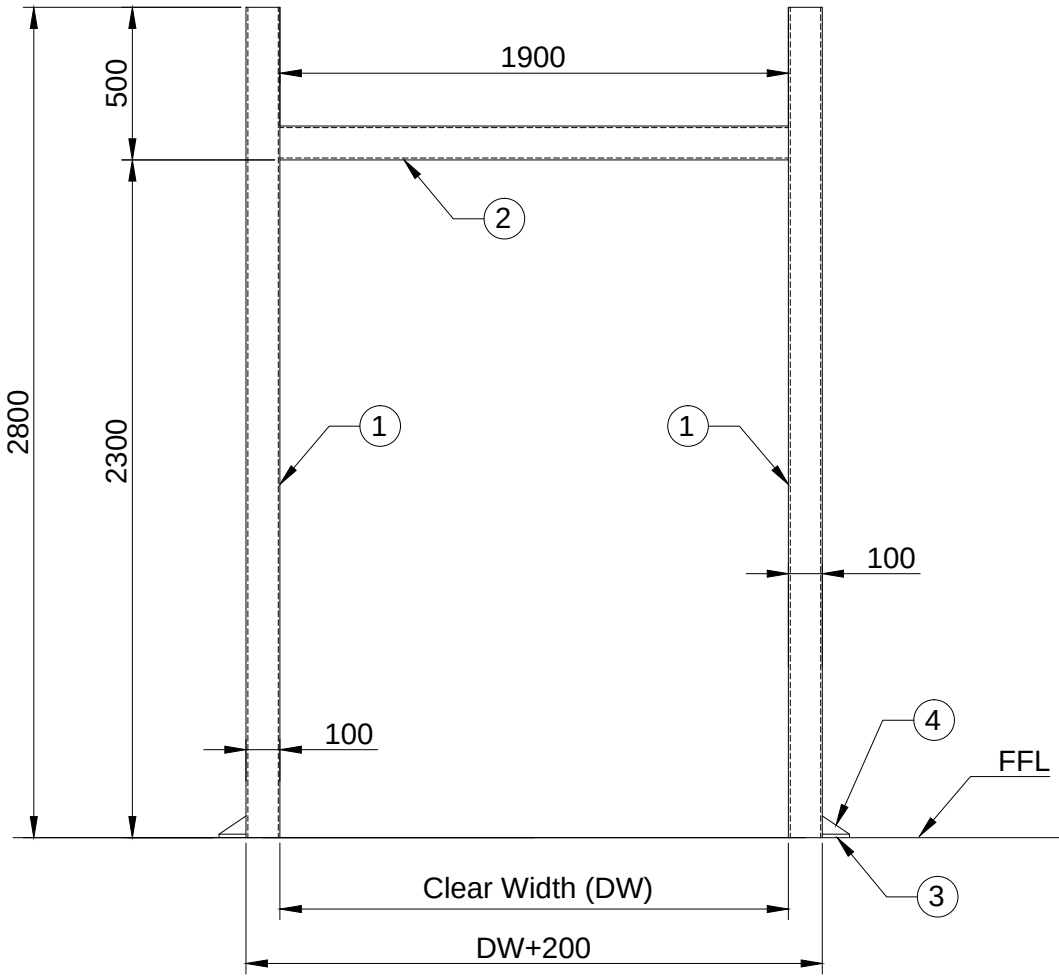


Elevation

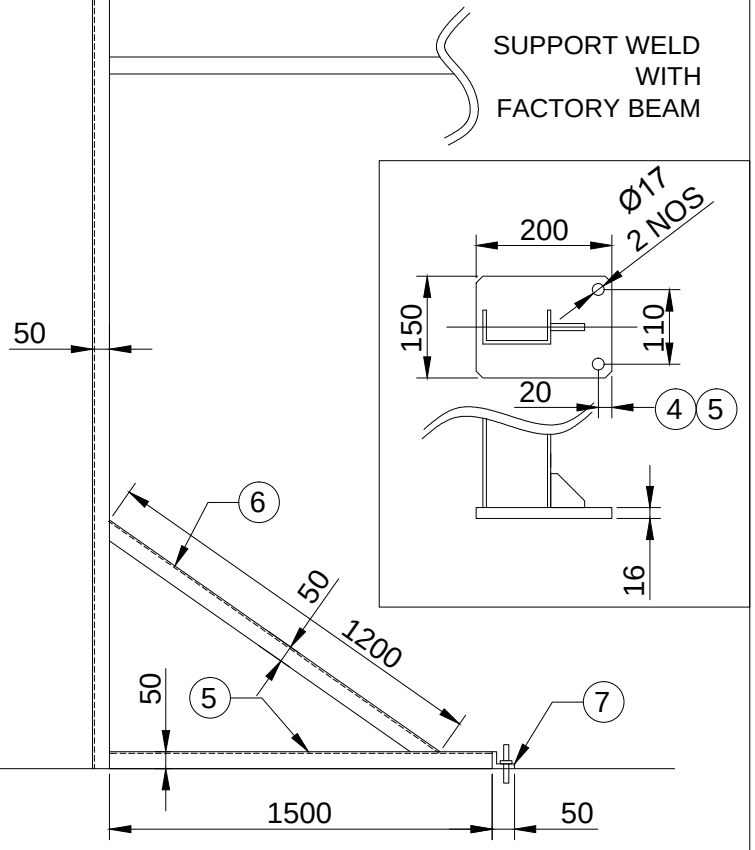

SIDE VIEW

1. ISMC 100 X 50 X 2800L = 2 NOS
2. ISMC 100 X 50 X 1900L = 1 NO
3. FLAT 150 X 16 X 200L = 2 NOS
4. RIB 50 X 10 X 50L = 2 NOS
5. ISMC 100 X 50 X 1500L = 2 NOS
6. ISMC 100 X 50 X 1200L = 2 NOS (NOTCH)
7. ISA 50 X 50 X 5 X 100L = 2 NOS.
8. ANCHOR BOLT M16 X 125L = 8 NOS

DOOR DIMENSION			
SR NO	DW	DH	QUANTITY
1	1900	2300	01

This drawing & designing is the property of NIHVA TECHNOLOGIES. Not to be sold or copied to any other concern.

TITLE: STRUCTURE FOR HSD HS9020GHY

NIHVA TECHNOLOGIES PVT. LTD.
NIHVA TECHNOLOGIES PVT. LTD. PUNE
Tel : 020 66304033
Email:- info@nihva.com
Website:- www.nihva.com

	NAME	SIGN	DATE
DRAWN	SURAJ		28/12/18
CHECK	PRADEEP		28/12/18
APPROVAL	R.D		28/12/18

If any queries contact : design@nihva.com

ALL DIMENSION ARE IN mm

CLIENT -

PROJECT -

SITE - PUNE.

DWG. NO. : NIHVA/18-19/VDR/296 REV- 0

SCALE: NTS WT: SHEET: 01 OF 01