


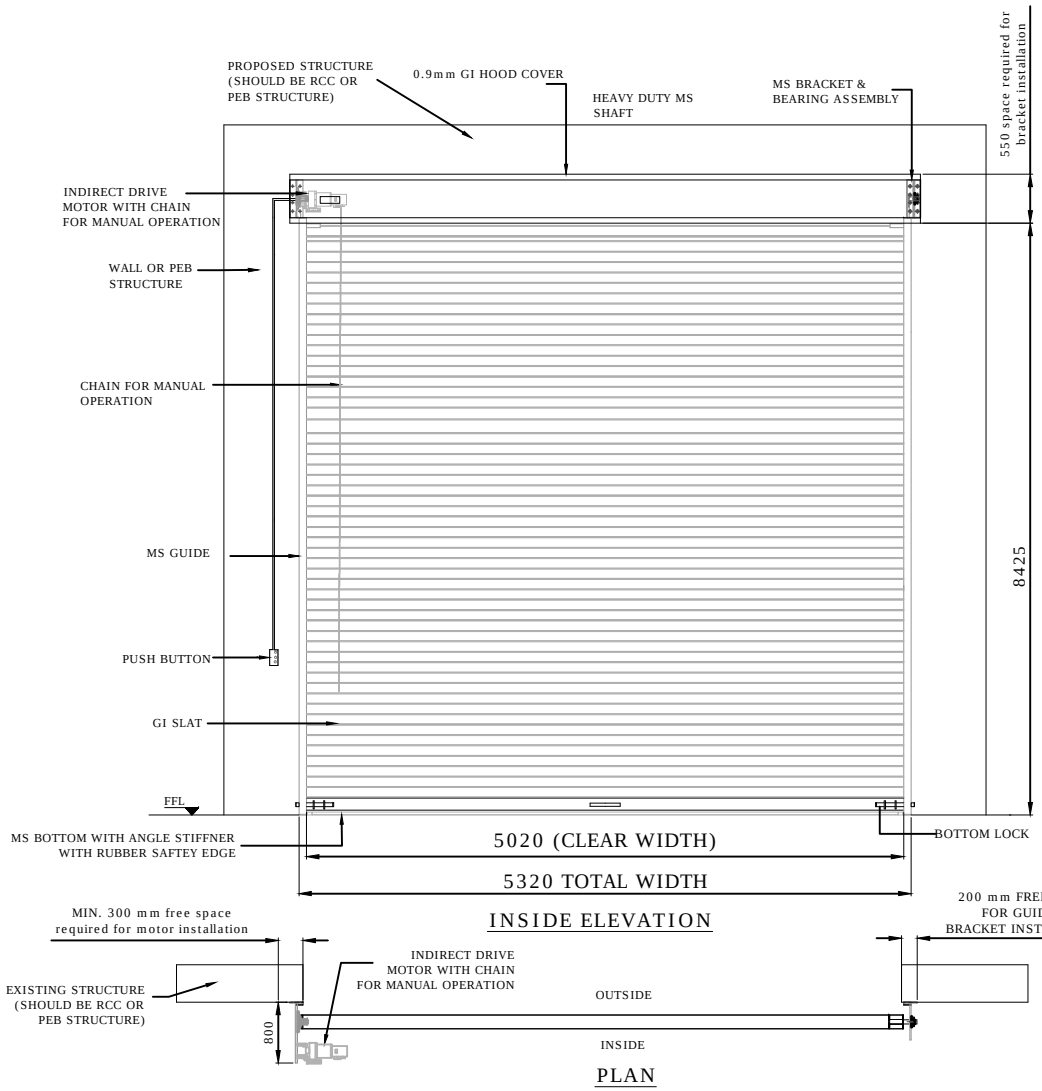


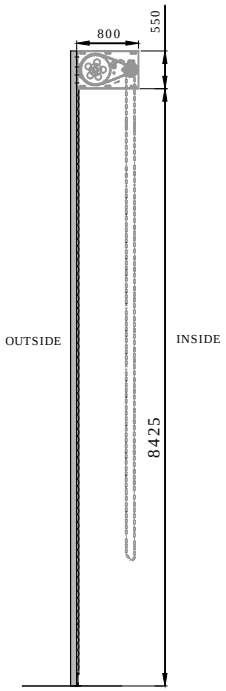

SIDE VIEW

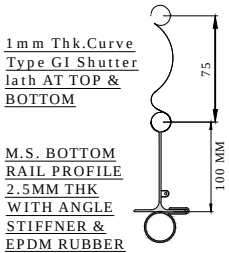

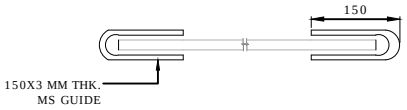

CLEAR WIDTH	CLEAR HEIGHT	QUANTITY	LOCATION
5020	8425	1	SHED 3

DIMENSION :

CLEAR WIDTH	CLEAR HEIGHT	QUANTITY
5020	8425	1

MATERIAL :

THICKNESS :

NOTE-
1.ONE COAT OF RED OXIDE WILL BE GIVEN SHUTTER (ONLY MS PART).
2. HOOD COVER WILL BE IN GI.
3.SINGLE PHASE SUPPLY SHOULD BE GIVEN TO THE SHUTTER.
4. REQUIRED STRUCTURE FOR SHUTTER SHALL BE IN CLIENT'S SCOPE.
5. ALL CIVIL WORK WILL BE IN CLIENT'S SCOPE.

REV	DATE	DESCRIPTION
1	24/08/2017	SHUTTER SIZE REVISED
2	30/08/2017	LEFT SIDE DRIVE
3	14/09/2017	HEIGHT REDUCED BY 400mm

NIHVA TECHNOLOGIES PVT. LTD. PUNE
Email:- info@nihva.com
Website:- www.nihva.com

TITLE:

MOTORIZED ROLLING SHUTTER

CLIENT'S APPROVAL :

CLIENT - SHILCHAR TECHNOLOGIES LTD.

PROJECT -

SITE LOCATION - VADODARA.

DWG. NO. :NIHVA/17-18/0166/R03

SCALE: NTS	WT:	SHEET:1 OF 1

DRAWN BY: SURAJ	DATE: 30-08-2017
CHECK : SHEKHAR	DATE: 30-08-2017
APPROVED : SHEKHAR	DATE: 30-08-2017

If any queries contact : projects@nihva.com

NOTE: ALL DIMENSIONS ARE IN mm

THIS DRAWING & DESIGN IS THE PROPERTY OF NIHVA TECHNOLOGIES. NOT TO BE SOLD OR COPY TO ANY OTHER CONCERN.