

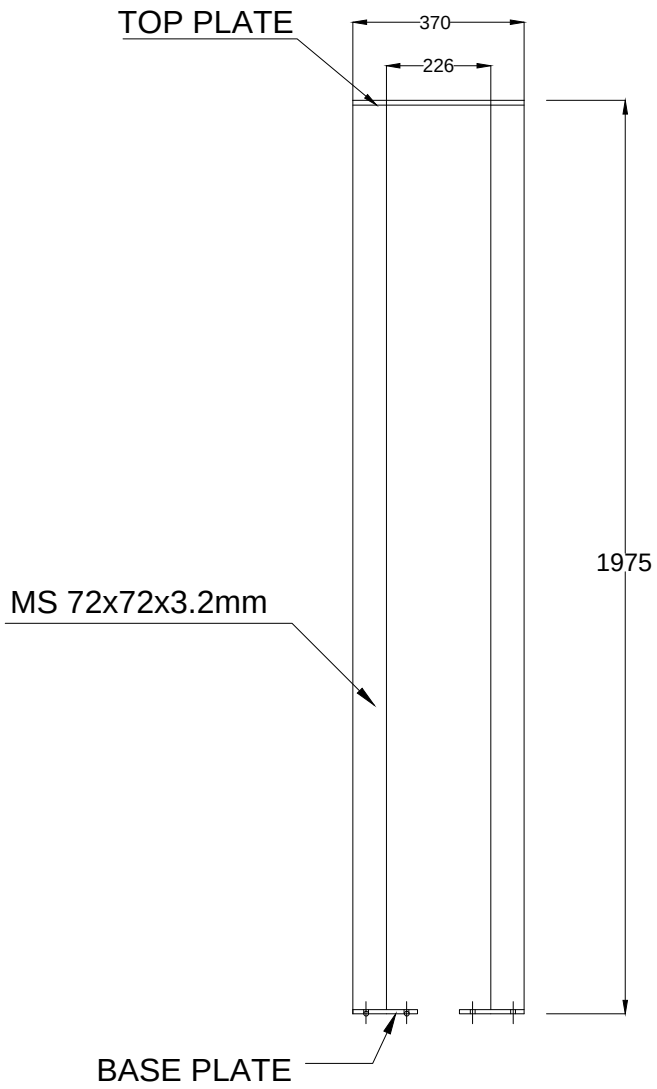


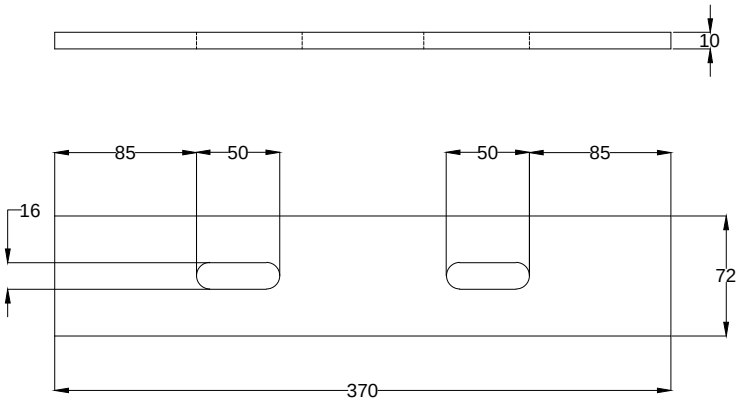


TOP PLATE

MATERIAL:-MS
THICKNESS:-10mm
QTY:- 08NOS

MATERIAL:-MS
QTY:- 08NOS

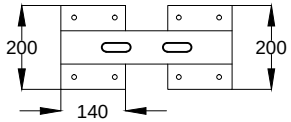

POST

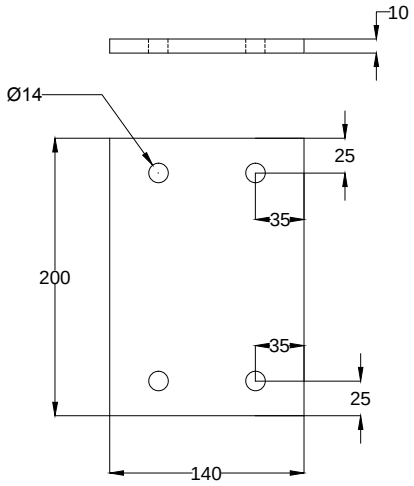

BASE PLATE

MATERIAL:-MS
THICKNESS:-10mm
QTY:- 16 NOS

NOTE:-ALL PLATE SHOULD BE LASER CUTTING

SR NO	TUBE SPECIFICATION		MATERIAL	SIZE
1	72X72X3.2mm MS TUBE	POST	MILD STEEL	1.955MTR- 16NOS
2	370X72X10mm MS PLATE	TOP PLATE	MILD STEEL	370X72X10mm- 08NOS
3	200X140X10mm MS PLATE	BOTTOM PLATE	MILD STEEL	140X200X10mm- 16NOS

This drawing & designing is the property of NIHVA TECHNOLOGIES. Not to be sold or copied to any other concern.

TITLE: SLIDING GATE POST DRAWING

NIHVA TECHNOLOGIES PVT. LTD.
NIHVA TECHNOLOGIES PVT. LTD. PUNE
Tel : 020 66304033
Email:- info@nihva.com
Website:- www.nihva.com

	Name	SIGN	DATE
DRAWN	SURAJ		04/12/18
CHECK	PRADEEP		04/12/18
APPROVAL	R.D		04/12/18

If any queries contact : design@nihva.com

ALL DIMENSION ARE IN mm

CLIENT -

PROJECT -

SITE LOCATION - WEST BENGAL.

DWG. NO. : NIHVA/18-19/VDR/246 REV.:- 0

SCALE: NTS WT: SHEET: 01 OF 01