


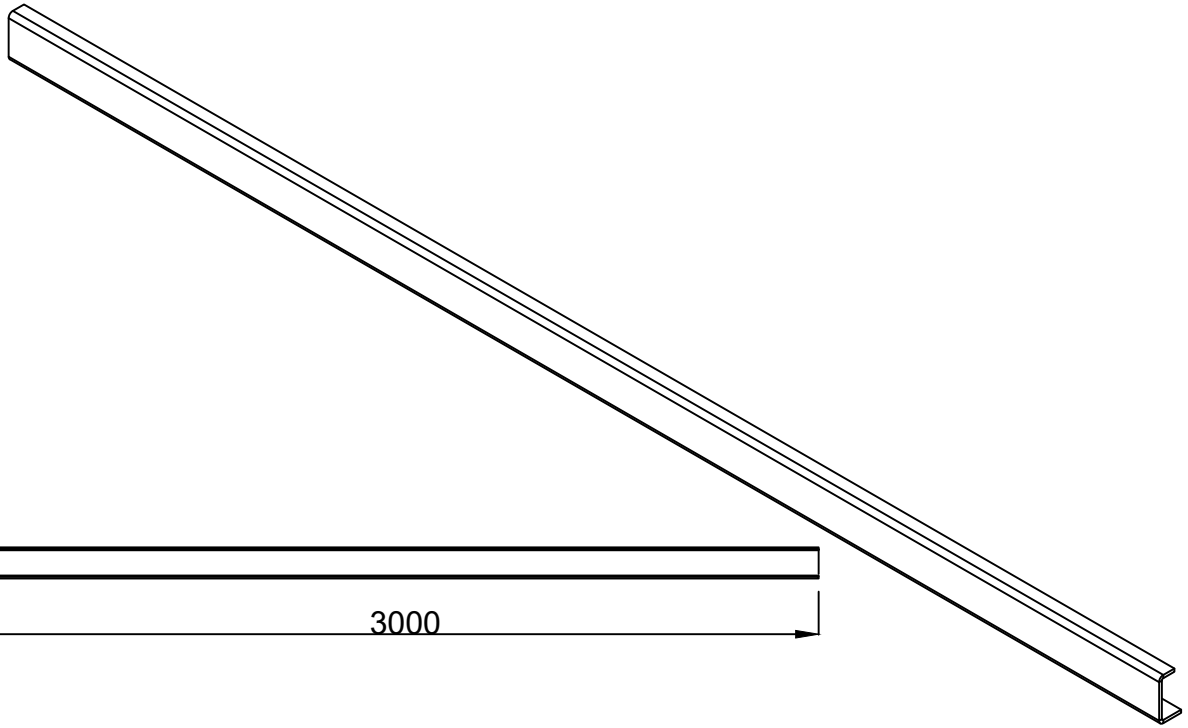


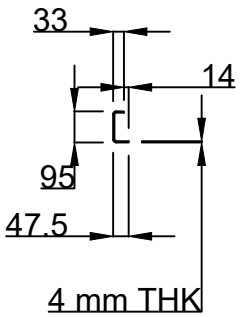

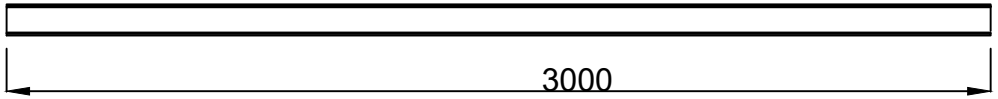

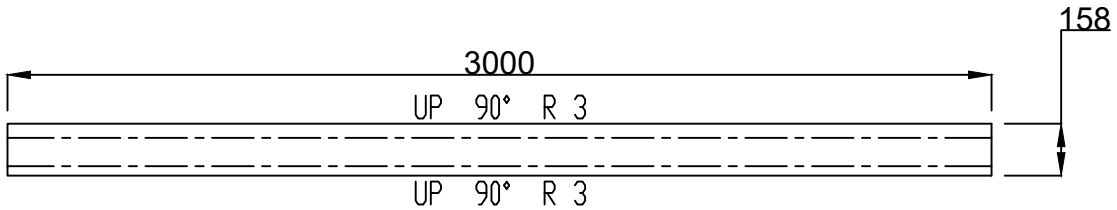


NOTE:

1) TRACK FOR ALL 11 DOORS SHOULD BE WITH 4 MM THICKESS.
2) FOR DOOR - 14 TRACK SHOULD BE WITH 6 MM THICKNESS.

This drawing & design is the property of NIHVA TECHNOLOGIES. Not to be sold or copied to any other concern.

REV.	REVISION DESCRIPTION	Date	Revised By
000	MODIFIED DUE TO RECIEVED COIL SIZE 1210 MM INSTEAD OF 1250 MM	24/05/2022	MAHESH S.

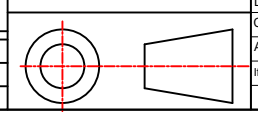

TITLE:- LEAF TRACKCRM DOOR

NIHVA TECHNOLOGIES PVT. LTD. PUNE
Tel : 020 66304033
Email:- info@nihva.com
Website:- www.nihva.com

	NAME	DATE	SIGN
DRAWN	M.SUTAR	24/05/2022	
CHECK	M.SUTAR	24/05/2022	
APPRD.			

CLIENT - NIHVA TECHNOLOGIES PVT.LTD

LOCATION -

PRODUCT - SLIDING DOOR

If any queries contact : design@nihva.com

DWG NO:-NIHVA/22-23/VDR/0015 REV- 0

ALL DIMENSION ARE IN mm

SCALE: NTS SCALE:-- 1:1 SHEET: 01 OF 02