
A1

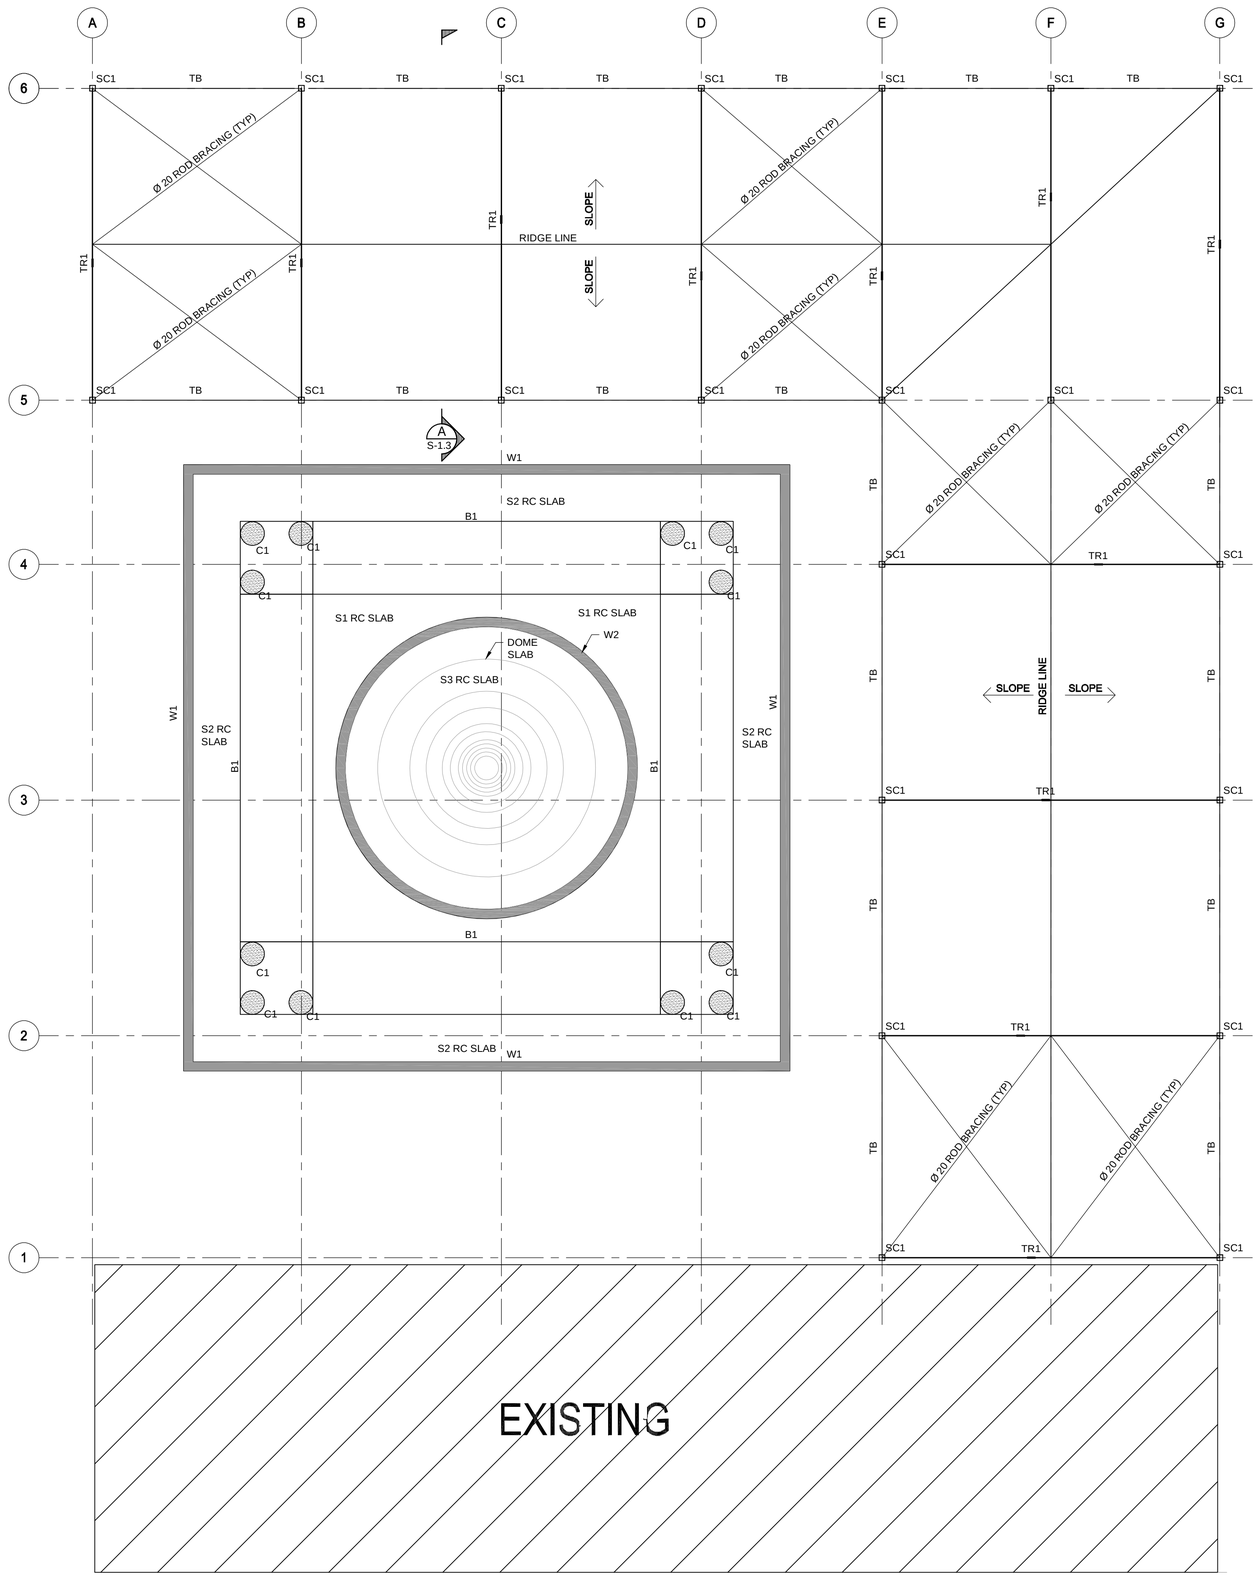

ROOF LAYOUT
SCALE = 1:75

SCHEDULE OF RC BEAM				
SR. NO.	BEAM MARK	SIZE		REMARKS
		WIDTH	DEPTH	
1	B1	1800	1250	

SCHEDULE OF RC SLAB		
SR. NO.	SLAB MARK	THICKNESS
1	S1	200
2	S2	175
3	S3	200

SCHEDULE OF WALL		
SR. NO.	WALL MARK	THICKNESS
1	W1	230
2	W2	230

© THIS DRAWING IS THE PROPERTY OF PPS PVT. LTD. AND SHALL NOT BE REPRODUCED OR USED WITHOUT THEIR WRITTEN PERMISSION.