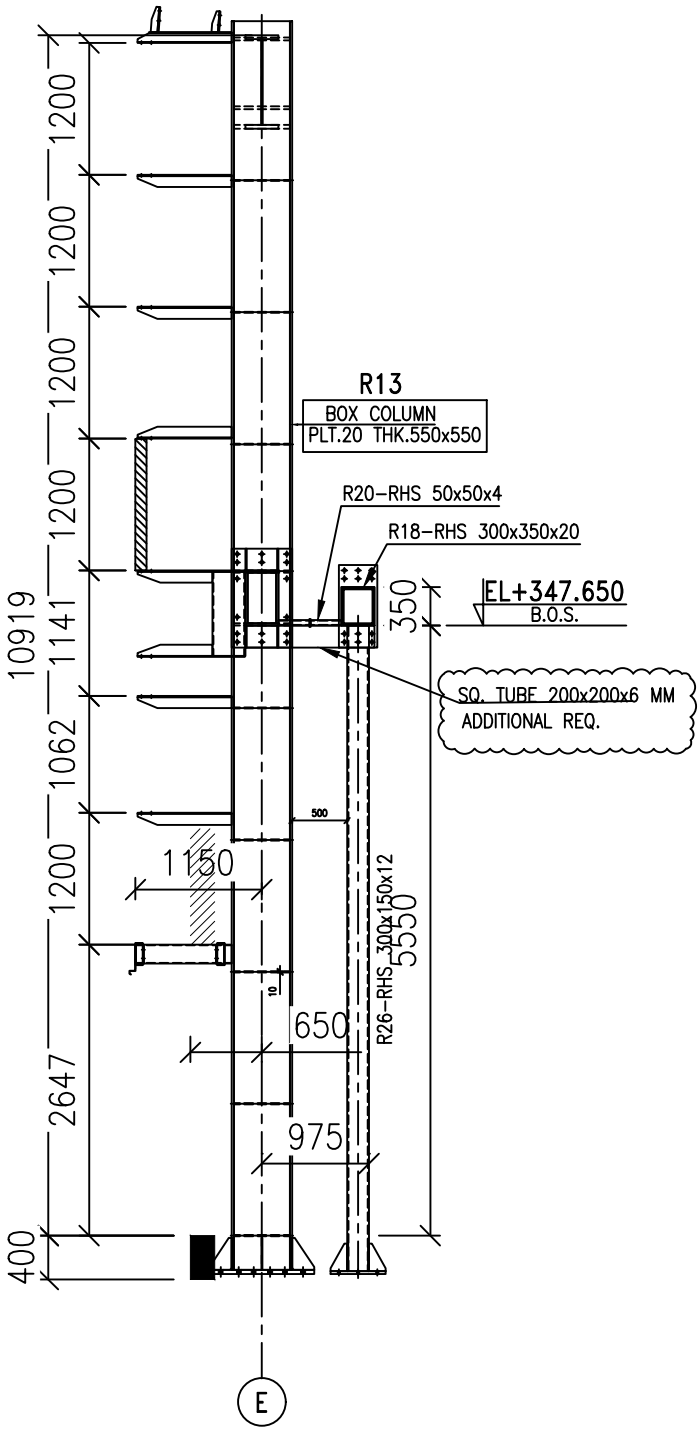
R13
BOX COLUMN
PLT.20 THK.550x550
R20-RHS 50x50x4
R18-RHS 300x350x20
EL+347.650
B.O.S.
350
SQ. TUBE 200x200x6 MM
ADDITIONAL REQ.
10919
1200
1200
1200
1200
1141
1062
1200
2647
400
500
1150
650
975
R26-RHS 300x150x12
550
E

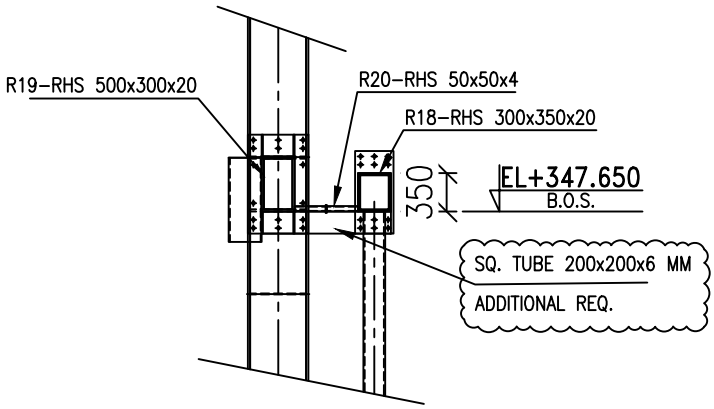
R19-RHS 500x300x20
R20-RHS 50x50x4
R18-RHS 300x350x20
EL+347.650
B.O.S.
350
SQ. TUBE 200x200x6 MM
ADDITIONAL REQ.