




SIDE VIEW

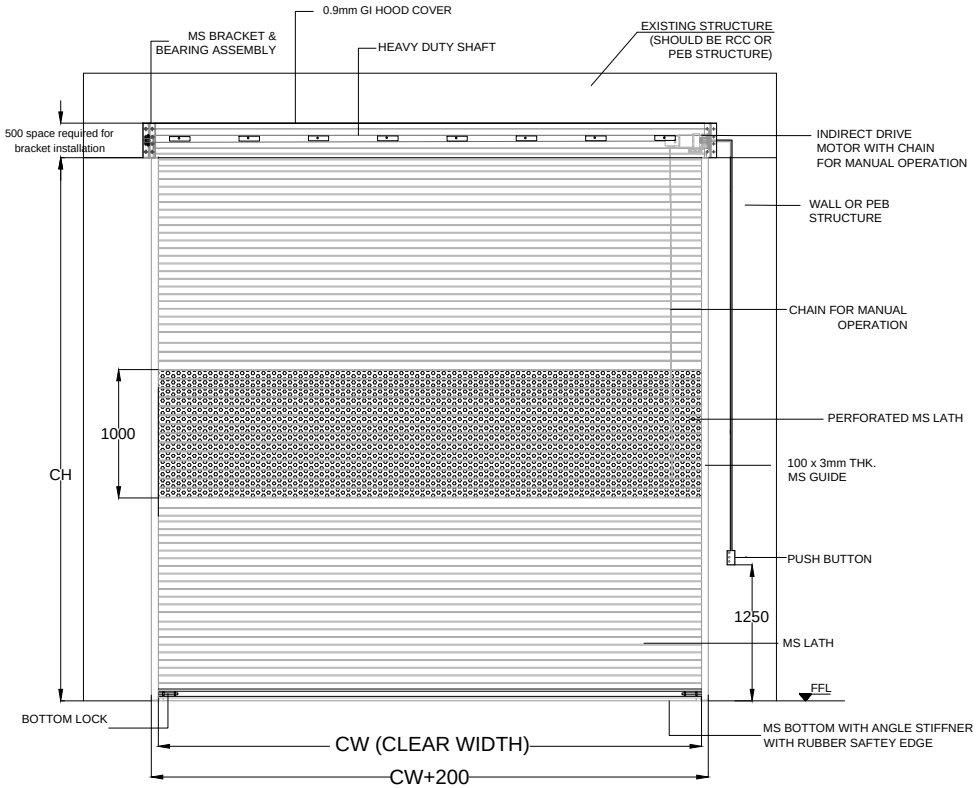


ELEVATION

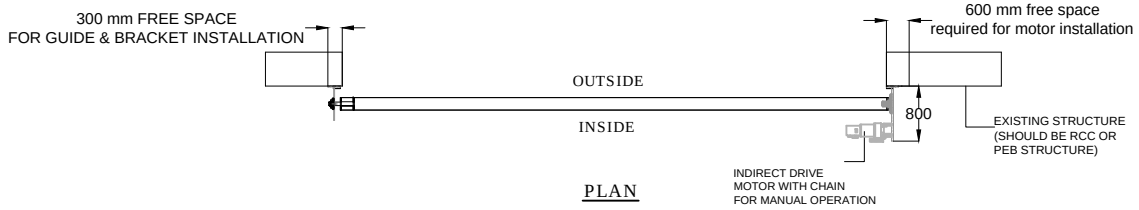

PLAN

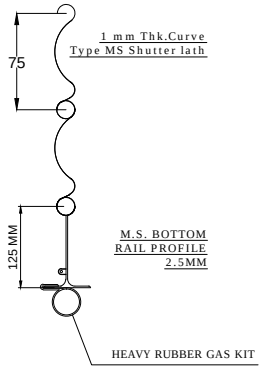

M.S. BOTTOM RAIL PROFILE 2.5MM

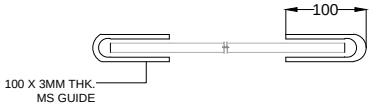

NOTE:
1 REQUIRED STRUCTURE FOR SHUTTER SHALL BE IN CLIENT SCOPE.
2.ONE COAT OF RED OXIDE PRIMER WILL BE GIVEN TO THE SHUTTER.
3.SINGLE PHASE. 3CORE 1.2SQ. CABLE REQUIRED AT SITE (CLIENT'S SCOPE)
4.COLOUR OF SHUTTER WILL BE RAL 7038 GREY

TOLERANCE - ±10mm

CLEAR WIDTH	CLEAR HEIGHT	QTY.
4000mm	4000mm	01NOS

This drawing & design is the property of NIHVA TECHNOLOGIES. Not to be sold or copied to any other concern.

TITLE
MOTORISED ROLLING SHUTTER

	NAME	SIGN	DATE
DRAWN	SURAJ		12-10-2018
CHECK	PRADEEP		12-10-2018
APPRD.	R.D		12-10-2018

NIHVA TECHNOLOGIES PVT. LTD.
NIHVA TECHNOLOGIES PVT. LTD. PUNE
Tel : 020 66304033
Email:- info@nihva.com
Website:- www.nihva.com

CLIENT -VAICHAL CONSTRUCTION PVT. LTD
PROJECT - CNH
SITE LOCATION - CHAKAN
If any queries contact : design@nihva.com
DWG. NO. : NIHVA/18-19/0144
REV- 0
ALL DIMENSION ARE IN mm
SCALE: NTS
WT:
SHEET: 01 OF 01