HANDING DETAILS

LH		LEFT HAND
RH		RIGHT HAND
LHR	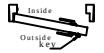	LEFT HAND REVERSE
RHR		RIGHT HAND REVERSE

ABBRIVATIONS

WOW-Wall Opening Width
FW-Frame Width
WOH-Wall Opening Height
FH-Frame Height
UC-Under Cut
FFL-Finished Floor Level

QTY	HANDING	COLOUR

	Date	Sign
DWG For Approval.		
DWG For Construct.		

NOTES:

1:All Dimensions are in mm
2:Tolerances - All linear dimensions +/- 3mm, others +/- 0.5mm
3:Drawings are indicative for type of hardware, location. For details please refer product catalog.
4: All electrified hardware the scope of power supply, including interface with the security system and fire alarm in not in our scope of supply & installation .
5:Design Parameters are Subjected to change without Notice for Betterment.
6:Hardware Must be Full Fill Fire Rating Standards(if Fire Doors)
7:These are Conceptual Drawings only.
8:Need Exact Templates / Samples for Client Scope/Provisional Hardware's ,if Newly Added Hardware (Which are Not used on Earlier)for Making the Provisions.

ELEVATION

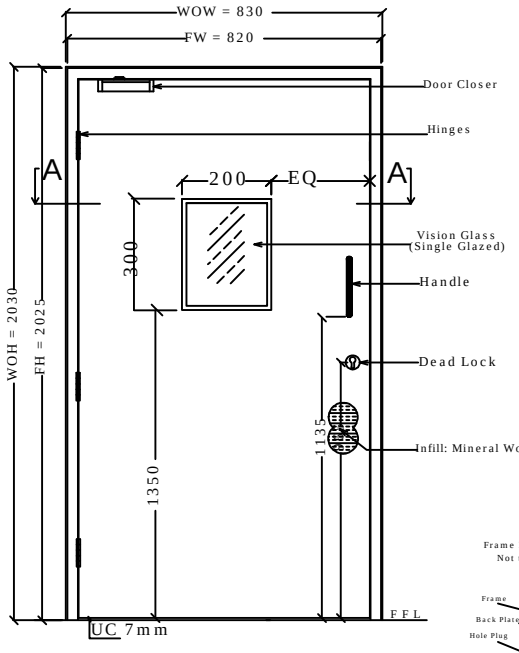

POS	Supply Description	Qty
1	HMPS Door Steel Set: 820.00 x 2,025.00 mm Single leaf door	06
	Door Code : Wall Opening (W x H) : 830.00 mm x 2,030.00 mm Material Specifications: Frame : GI 1.20 mm Shutter : GI 0.80 mm Shutter Width / Active Shutter Width : 734.00 mm Frame Profile (D x H): 100.00 mm x 57.00 mm Frame Profile type : Kerf Frame Joint Type: Bolting Frame Rebate : Single Under Cut: 7.00 mm Door type : Single leaf door Leaf type : NA. Infill Material : Minerl wool (Density 96 Kg/M3) Handing : NA Key Box: No Fixing Shield: Universal Anchor Shutter thickness : 40.0mm Finish : Paint Finsih (As per Clients desired shade) Type of Fixing : On solid brick plastered wall with anchors	
	Frame Set:	1
	Shutter: Single leaf door	1
	Ball bearing butt hinge, SS304, of size 100 x 75 x 3mm with screws in SSS	3
	Dead lock with Cylinder	1
	S.S. "D" Type Handle (1 Set)	1
	Surface Heavy Door Closer with Standard Arm	1
	Standard Clear Non Fire Glass 6mm - Size: 200 x 300mm	1

Frame Profile & Fixing Details
Not to scale

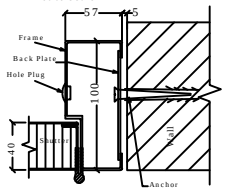

zero		02.08.21	K.P	MBG	KMP
Revisions	Reference	Date	Drn	Ckd	Apprd

SIZE : A4 SCALE :1:20
DRAWING NO: RSPL/220309/01

PROJECT:

Client : M/s. Nihva Technologies Pvt. Ltd.

TITLE: HMPS STEEL DOORS